

预制轻钢龙骨内隔墙

批准部门 中华人民共和国建设部 批准文号 建质[2003]17号
主编单位 中国建筑标准设计研究所 统一编号 GJBT-601
实行日期 二〇〇三年二月十五日 图集号 03J111-2

主编单位负责人 王艳
主编单位技术负责人 马洪
技术审定人 马洪
设计负责人 曹颖奇 胡珊

目 录

目录	1	墙板骨架构造	15
说明	2	角板连接节点	17
平面索引图	5	末板安装节点	18
剖面索引图	6	墙板与主体墙、柱连接节点	19
墙板龙骨及连接件	7	双层墙板与主体墙、柱连接节点	20
墙板固定连接件	8	双层隔声、保温墙与主体墙体连接节点	21
板型图	9	墙板与结构梁、板连接节点	22
单、双层墙板组装平面图	10	墙板悬空与结构梁板连接节点	24
普通墙板规格	12	墙板与楼地面连接、踢脚做法节点	25
墙板组装轴测图	13	墙板连接节点	27

墙板与风管结合示意图 35

风管下部墙板龙骨拼装示意图 36

电气开关插座安装节点 37

设备吊挂件安装节点 38

墙板内置线管结构 39

脸盆、吊柜安装图 40

墙板内置水管结构 41

附录一 预制轻钢龙骨内隔墙施工要求 42

附录二 墙体选用表 46

说 明

1 编制依据

本图集是根据建设部建质[2002]156号《二〇〇二年国家建筑标准设计编制工作计划》的通知中有关项目要求进行编制。

2 适用范围

适用于新建、改建、扩建的民用和工业建筑非承重内隔墙。

3 设计依据

房屋建筑制图统一标准 GB/T 50001-2001

建筑制图标准	GB/T 50104-2001
建筑抗震设计规范	GB 50011-2001
建筑防火设计规范(2001版)	GBJ 16-87
建筑内部装修设计防火规范	GB 50222-1995
民用建筑隔声设计规范	GBJ 118-88
民用建筑工程室内环境污染控制规范	GB 50325-2001
建筑装饰装修工程质量验收规范	GB 50210-2001
建筑工程施工质量验收统一标准	GB 50300-2001
建筑用轻钢龙骨	GB/T 11981-2001
建筑用轻钢龙骨配件	JG/T 558-1994

4 编制内容

本图集列入的预制轻钢龙骨内隔墙(以下简称预制墙板或墙板)有两种:硅酸钙板与轻钢龙骨组合;硅酸钙板与轻钢龙骨及防火、隔声材料组合。

4.1 墙板主要规格(mm)

长度	2440~6100
宽度	400、600、1220
厚度	76、80、100、150

4.2 墙板板型:共有9种

普通板、调节板、首板、末板、角板、洞板、槛板、线管板、水管板。

说 明								图集号	03J111-2
审核	李长发	徐畅	校对	徐畅	设计	熊火生	页	2	

5 设计要求

- 5.1 抗震措施: 预制墙板与主体结构连接采用柔性连接, 与梁、板、柱接缝处增设钢板抗震卡 (角龙骨、固定件) 固定。
- 5.2 隔声设计: 预制墙板隔声性能要求较高时, 可加大预制墙板内的玻璃棉密度、厚度及硅酸钙板层数; 或做双层墙板, 板距 20mm 或 40mm 作为空气隔声层。根据设计需要其间也可填充玻璃棉、岩棉、聚苯板等材料。
- 5.3 吊挂设计: 墙上吊挂物品须注意, 竖龙骨部位单点吊挂力 $\leq 1200\text{N}$, 硅酸钙板部位单点吊挂力 $\leq 300\text{N}$ 。若需吊挂 $> 1200\text{N}$ 重物时, 可将一根角龙骨横向固定在墙板内的竖龙骨上。
- 5.4 电气设计: 使用线管板, 现场将电线接入。线路、开关及插座可作露明设计。
- 5.5 给排水设计: 使用水管板, 现场将墙体外的铝塑复合水管和龙头安装上。给排水管线也可作露明设计。
- 5.6 防潮、防水设计: 沿内隔墙设计水池、水箱、盥洗设备时, 墙面应涂刷防水涂料或做防水饰面。潮湿部位 (如厨房、卫生间等) 可做瓷砖 (瓷板) 饰面。安装底板时每隔 200mm 钻一孔, 再贴瓷砖 (瓷板)。
- 5.7 门窗、踢脚设计: 位于门窗两边及上下部的墙板, 安装时注意内置加强竖龙骨的朝向。设计采用水磨石、大理石踢

- 脚板可直接粘贴, 安装时每隔 200mm 钻一孔再粘贴。设计采用木质或塑料踢脚板可采用射钉或胶粘剂等固定。
- 5.8 墙面装修: 墙面装修根据设计要求, 可选用抹灰、喷浆、油漆、涂料、壁纸以及其他特殊饰面。
- 5.9 墙板安装使用金属胀锚螺栓固定, 间距 $\leq$ 竖龙骨间距。
- 5.10 预制轻钢龙骨内隔墙施工要求详见本图集附录。

6 预制轻钢龙骨内隔墙物理性能指标


详见表1

7 预制轻钢龙骨内隔墙防火、隔声性能指标


详见表2

8 详图索引符号选用方法:

选用整页详图:

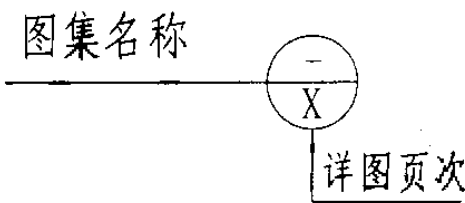

选用部分详图:

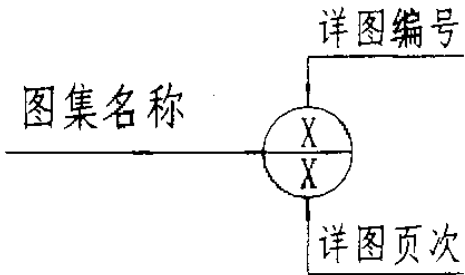


说 明								图集号	03J111-2
审核	李长发	校对	徐畅	设计	熊火生	页	3		

表1 预制轻钢龙骨内隔墙物理性能指标

序号	项目	厚度（mm）			检测单位
		76	100	150	
1	抗冲击性能，次	砂袋 30kg，6 次冲击，板面无裂纹，无破损			江西省建材产品质量监督检验站 数据为双面单层硅酸钙板，厚度为 6mm 时检测结果。
2	单点吊挂力	龙骨位置单只螺钉 1200N		板面位置单只螺钉 300N	
3	抗折破坏荷载（800mm 跨距）	10000N	-	-	
4	干燥收缩值（mm/m）	≤ 0.7	-	-	
5	气干面密度（kg/m²）	21.0	24.9	30.0	
6	空气声计权隔声量（dB） （玻璃棉）	41	-	-	国家防火建筑材料质量监督检验中心
7	耐火极限（h） （25 厚玻璃棉，密度 20Kg/m³）	1.1	-	-	国家建筑工程质量监督检验中心
8	燃烧性	非燃烧体			

表2 预制轻钢龙骨内隔墙防火、隔声性能指标

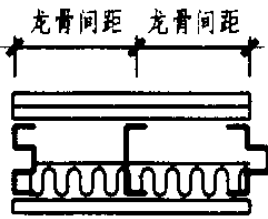图示	墙体尺寸 mm					耐火极限 min	隔音性能 dB	墙体自重 (计算值)		适用范围
	面板厚	面板排板方式	层数	龙骨宽度	墙厚			kN/m ²	kg/m ²	
	6	6+6	1+1	64	76	67min(玻璃棉)	41 (玻璃棉)	0.167	17	厨房 盥洗室 壁橱墙 分室墙
						1.1h				

本图集参加编制单位

南昌中环新型墙体装璜材料厂

说 明

图集号

03J111-2

审核

李长发

校对


徐畅

设计

熊火生

页

4

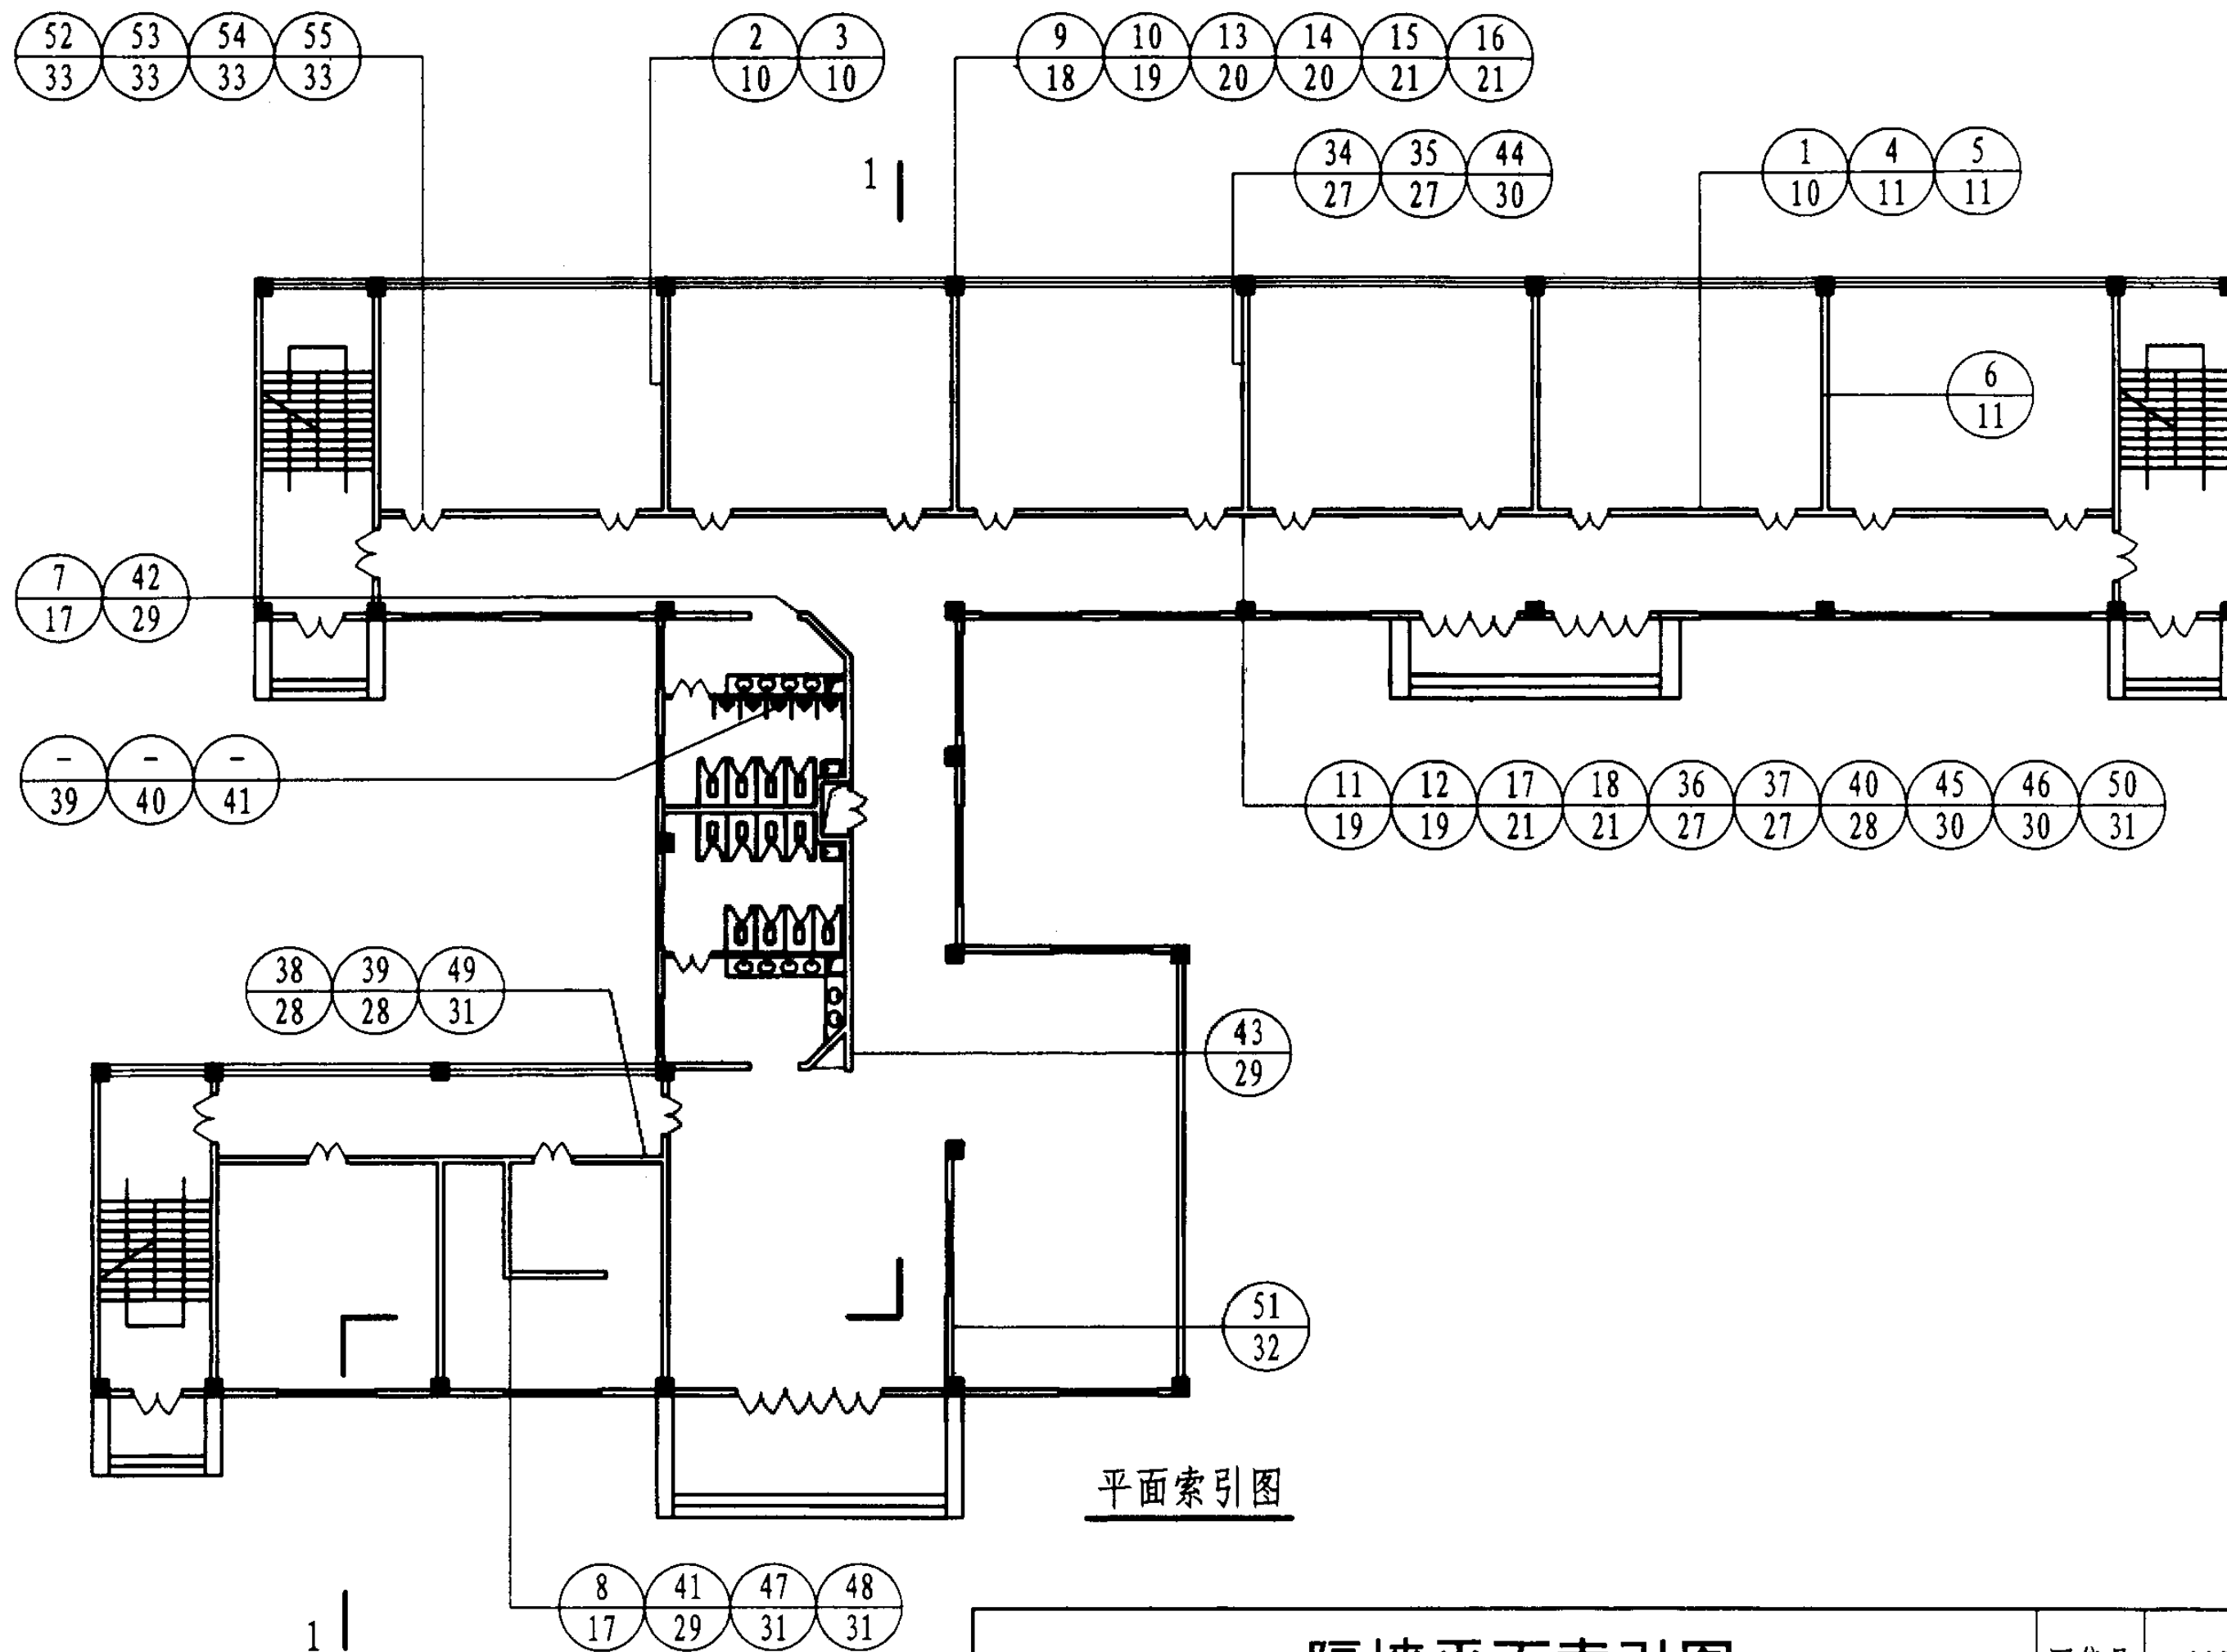

平面索引图

隔墙平面索引图

图集号

03J111-2

审核

李长发

校对

徐畅


徐畅

设计

熊火生

页

5

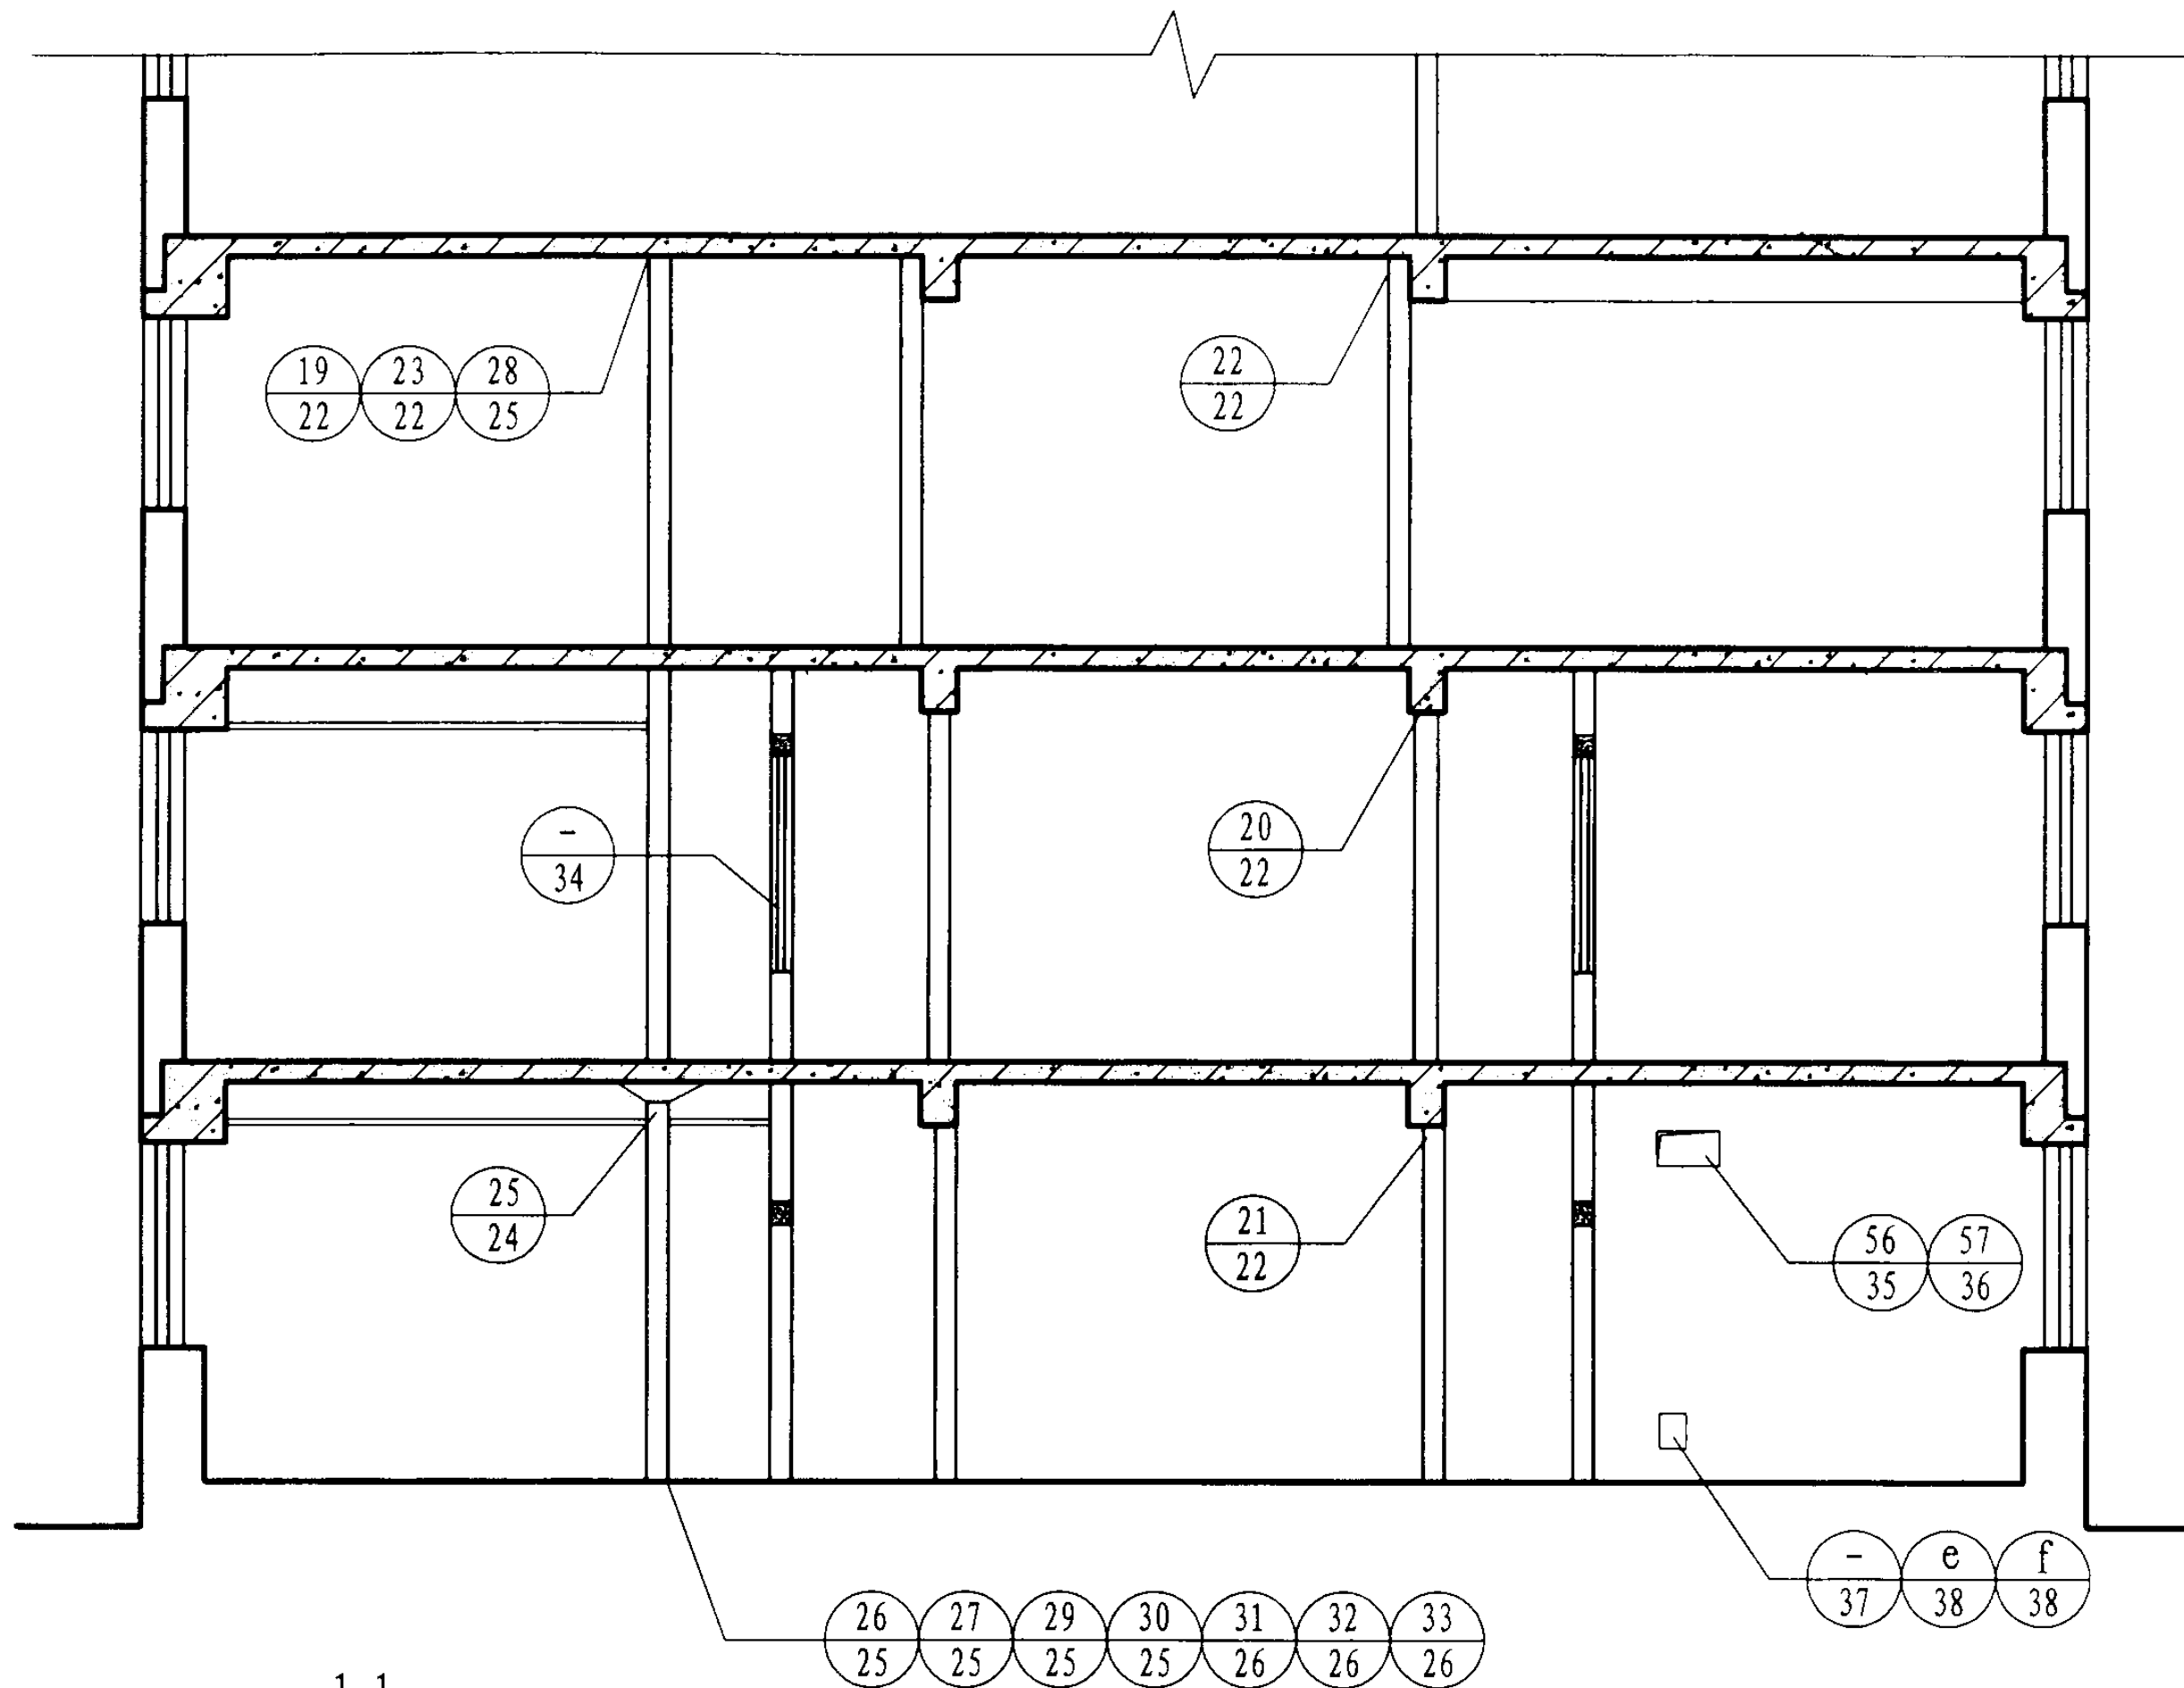


1-1

剖面索引图

图集号 03J111-2

审核 李长发 校对 徐畅 设计 熊火生

页 6

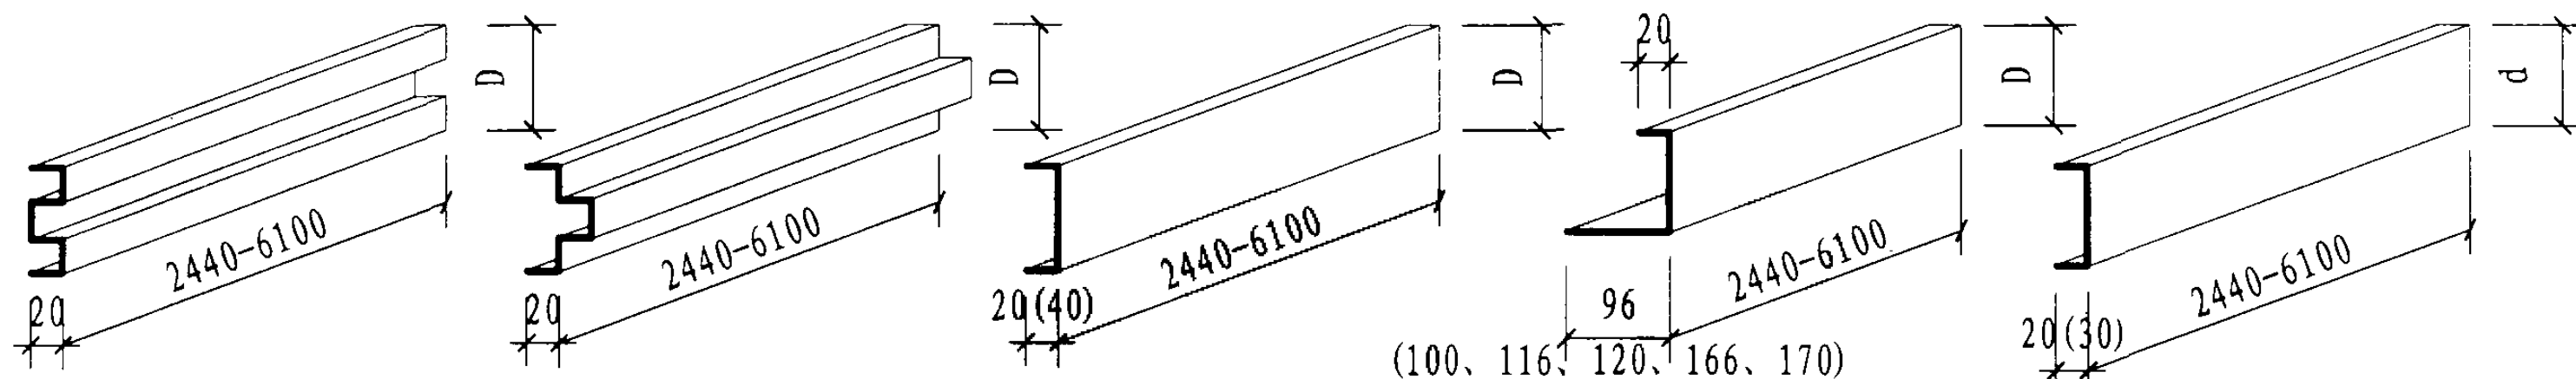


凹形竖龙骨

凸形竖龙骨


竖龙骨

边龙骨


加强竖龙骨

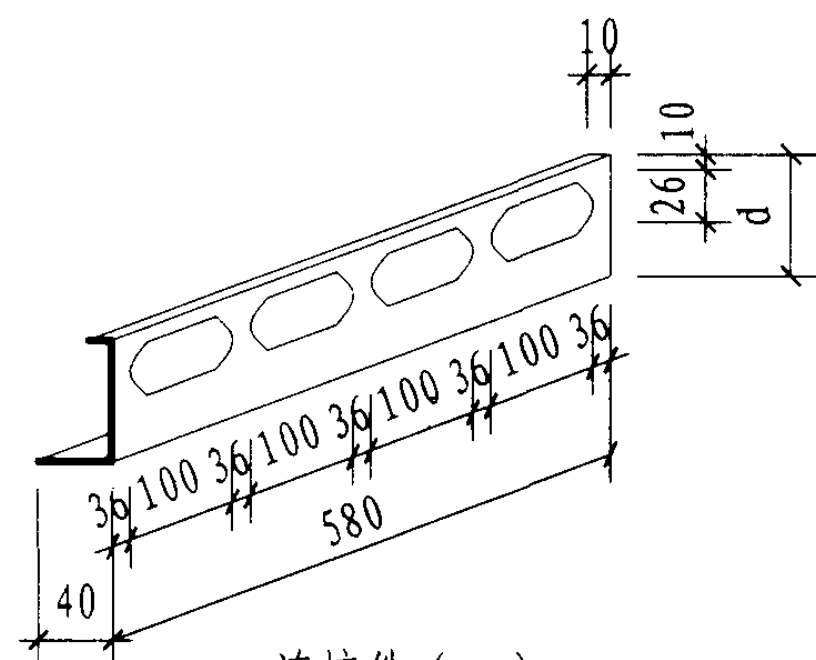


连接件 (一)

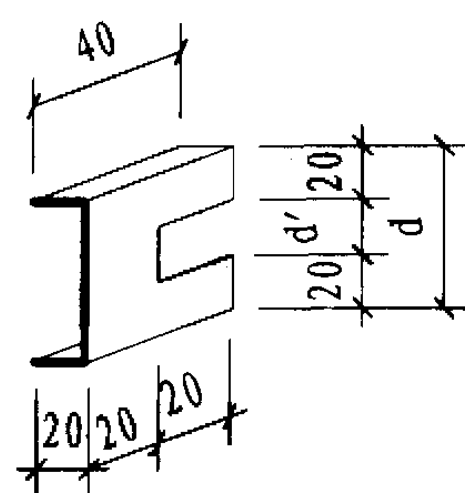


连接件 (二)

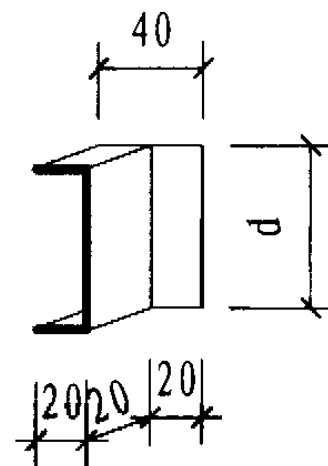

连接件 (三)

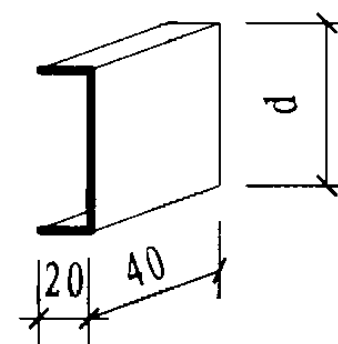

连接件 (四)

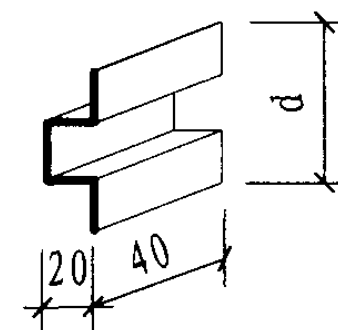

连接件 (五)

注: 1. 龙骨及连接件均为0.8厚

2. D为64 (84、134)

3. d为62 (82、132)

4. d'为22 (42、92)

墙板龙骨及连接件

图集号

03J111-2

审核

李长发

校对


徐畅

设计


熊火生

页


7

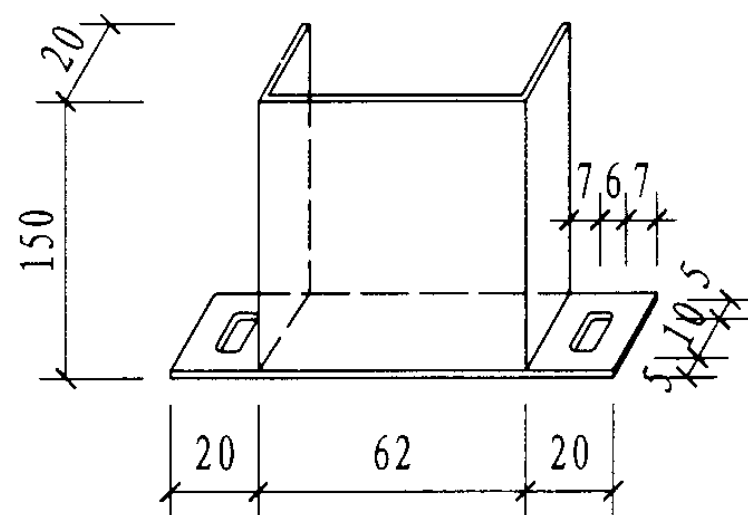

1#固定件

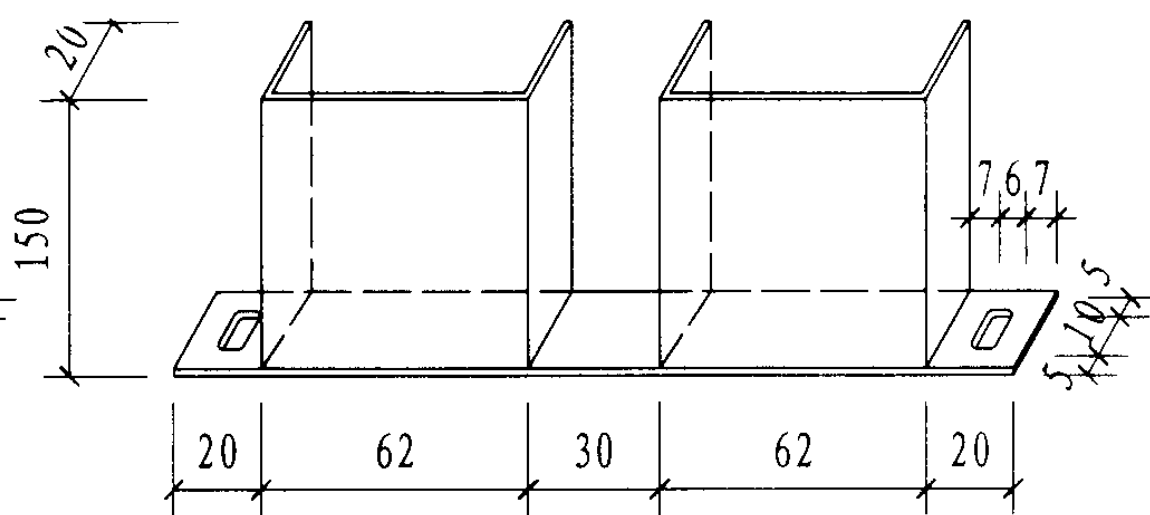


3#固定件

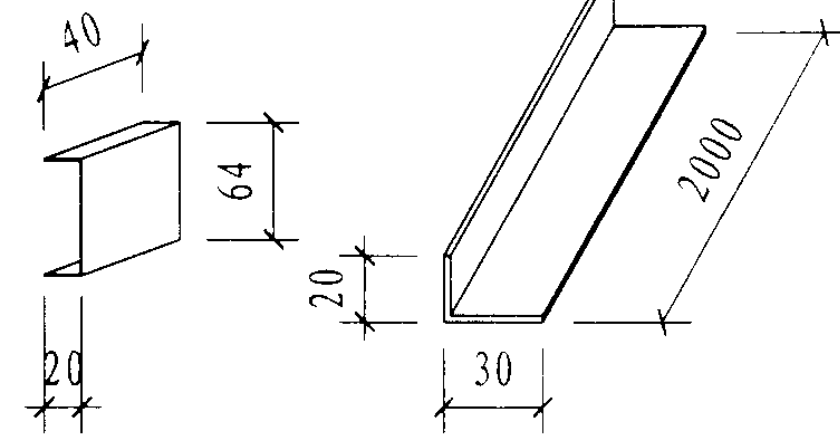


5#固定件


角龙骨

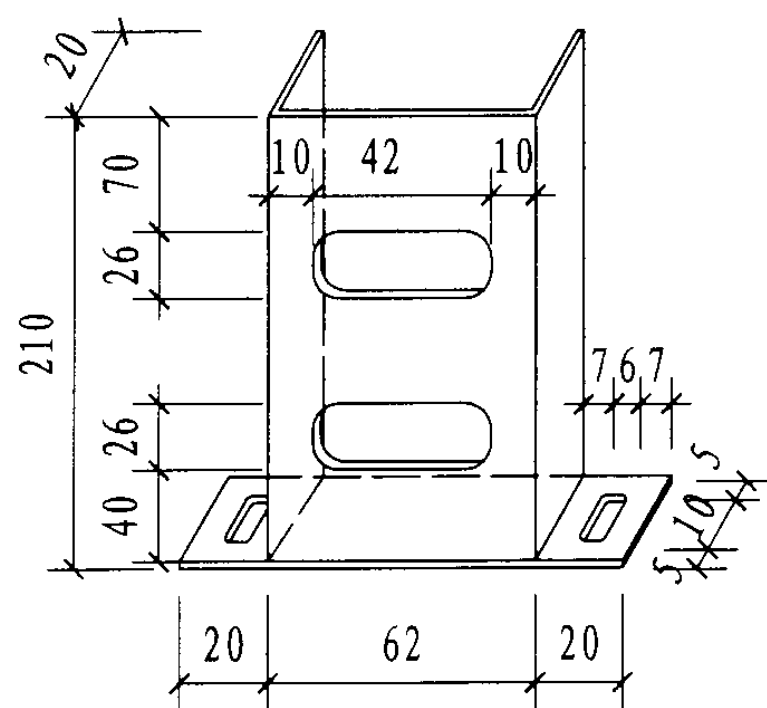

2#固定件

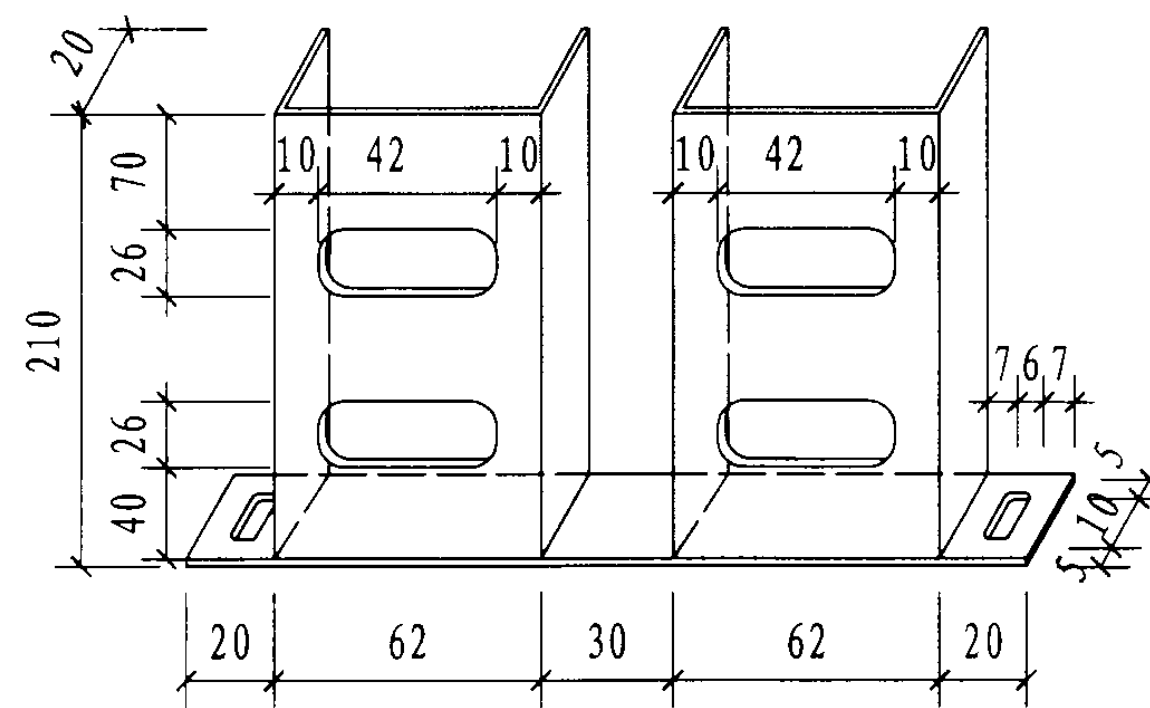

4#固定件

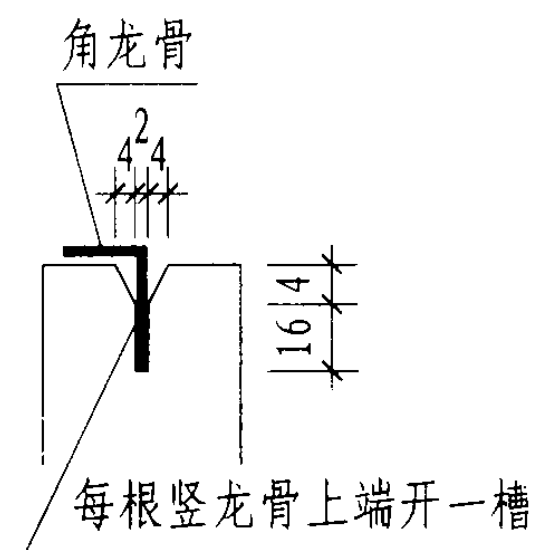

端头节点

注：1. 用在楼板顶使用镀锌板或冷轧板连接件，其厚度为1.6

用在楼地面需使用不锈钢固定件，其厚度为0.8

2. 固定件板厚为1.6

3. 角龙骨厚度为2.0

墙板固定连接件

图集号

03J111-2

审核

李长发

校对

徐畅

徐畅

设计


熊火生

熊火生


页

8


首板

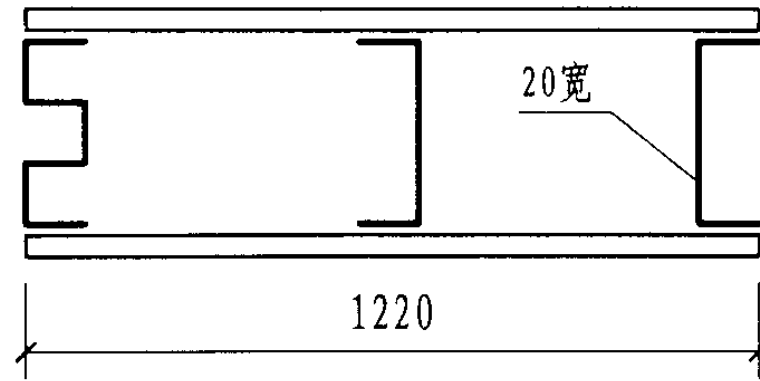


调节板

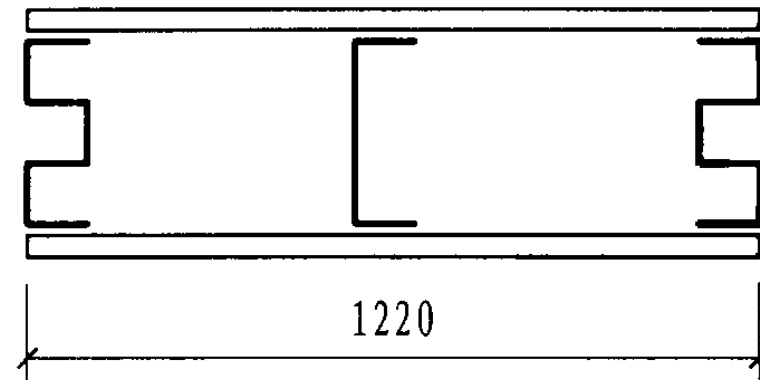


橦板

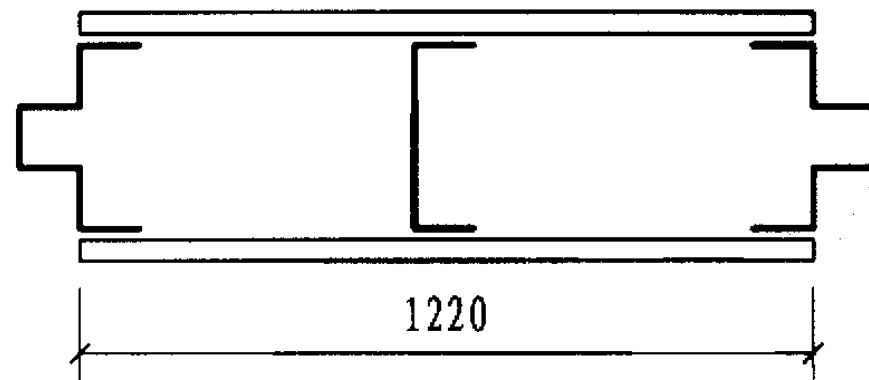


水管板

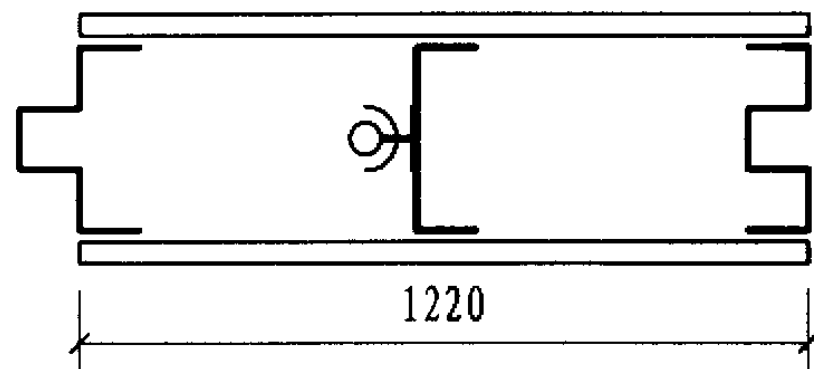


角板

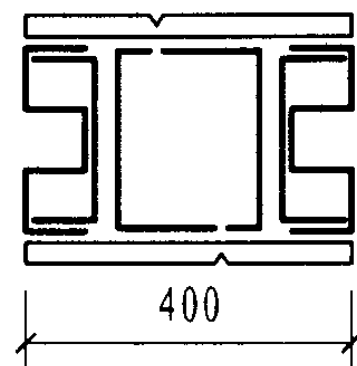


末板

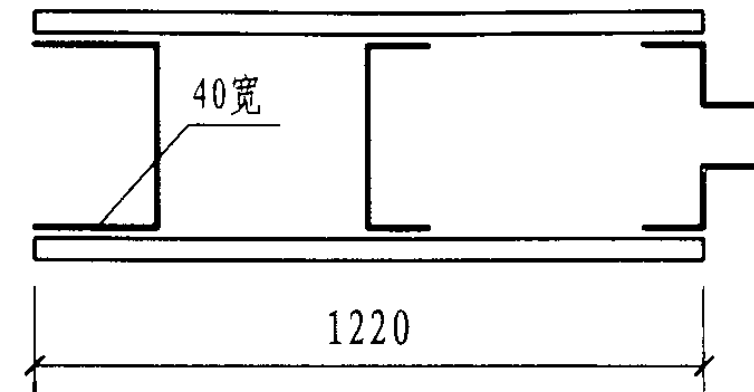


普通板

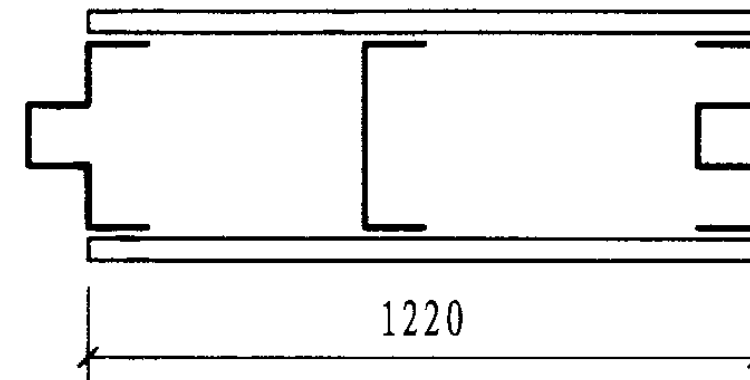

洞板

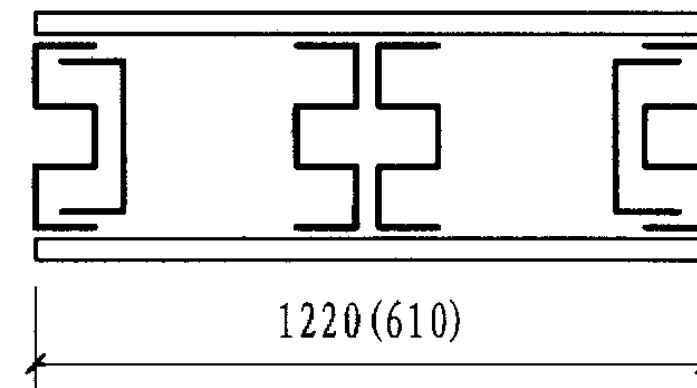

线管板

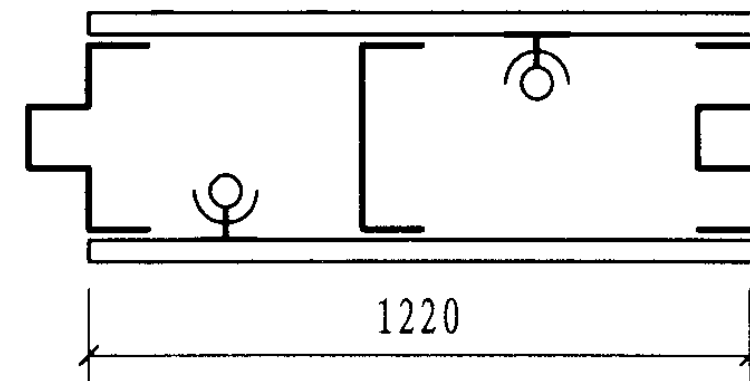

板型图

图集号


03J111-2

审核 李长发

校对 徐畅

设计 熊火生

页 9

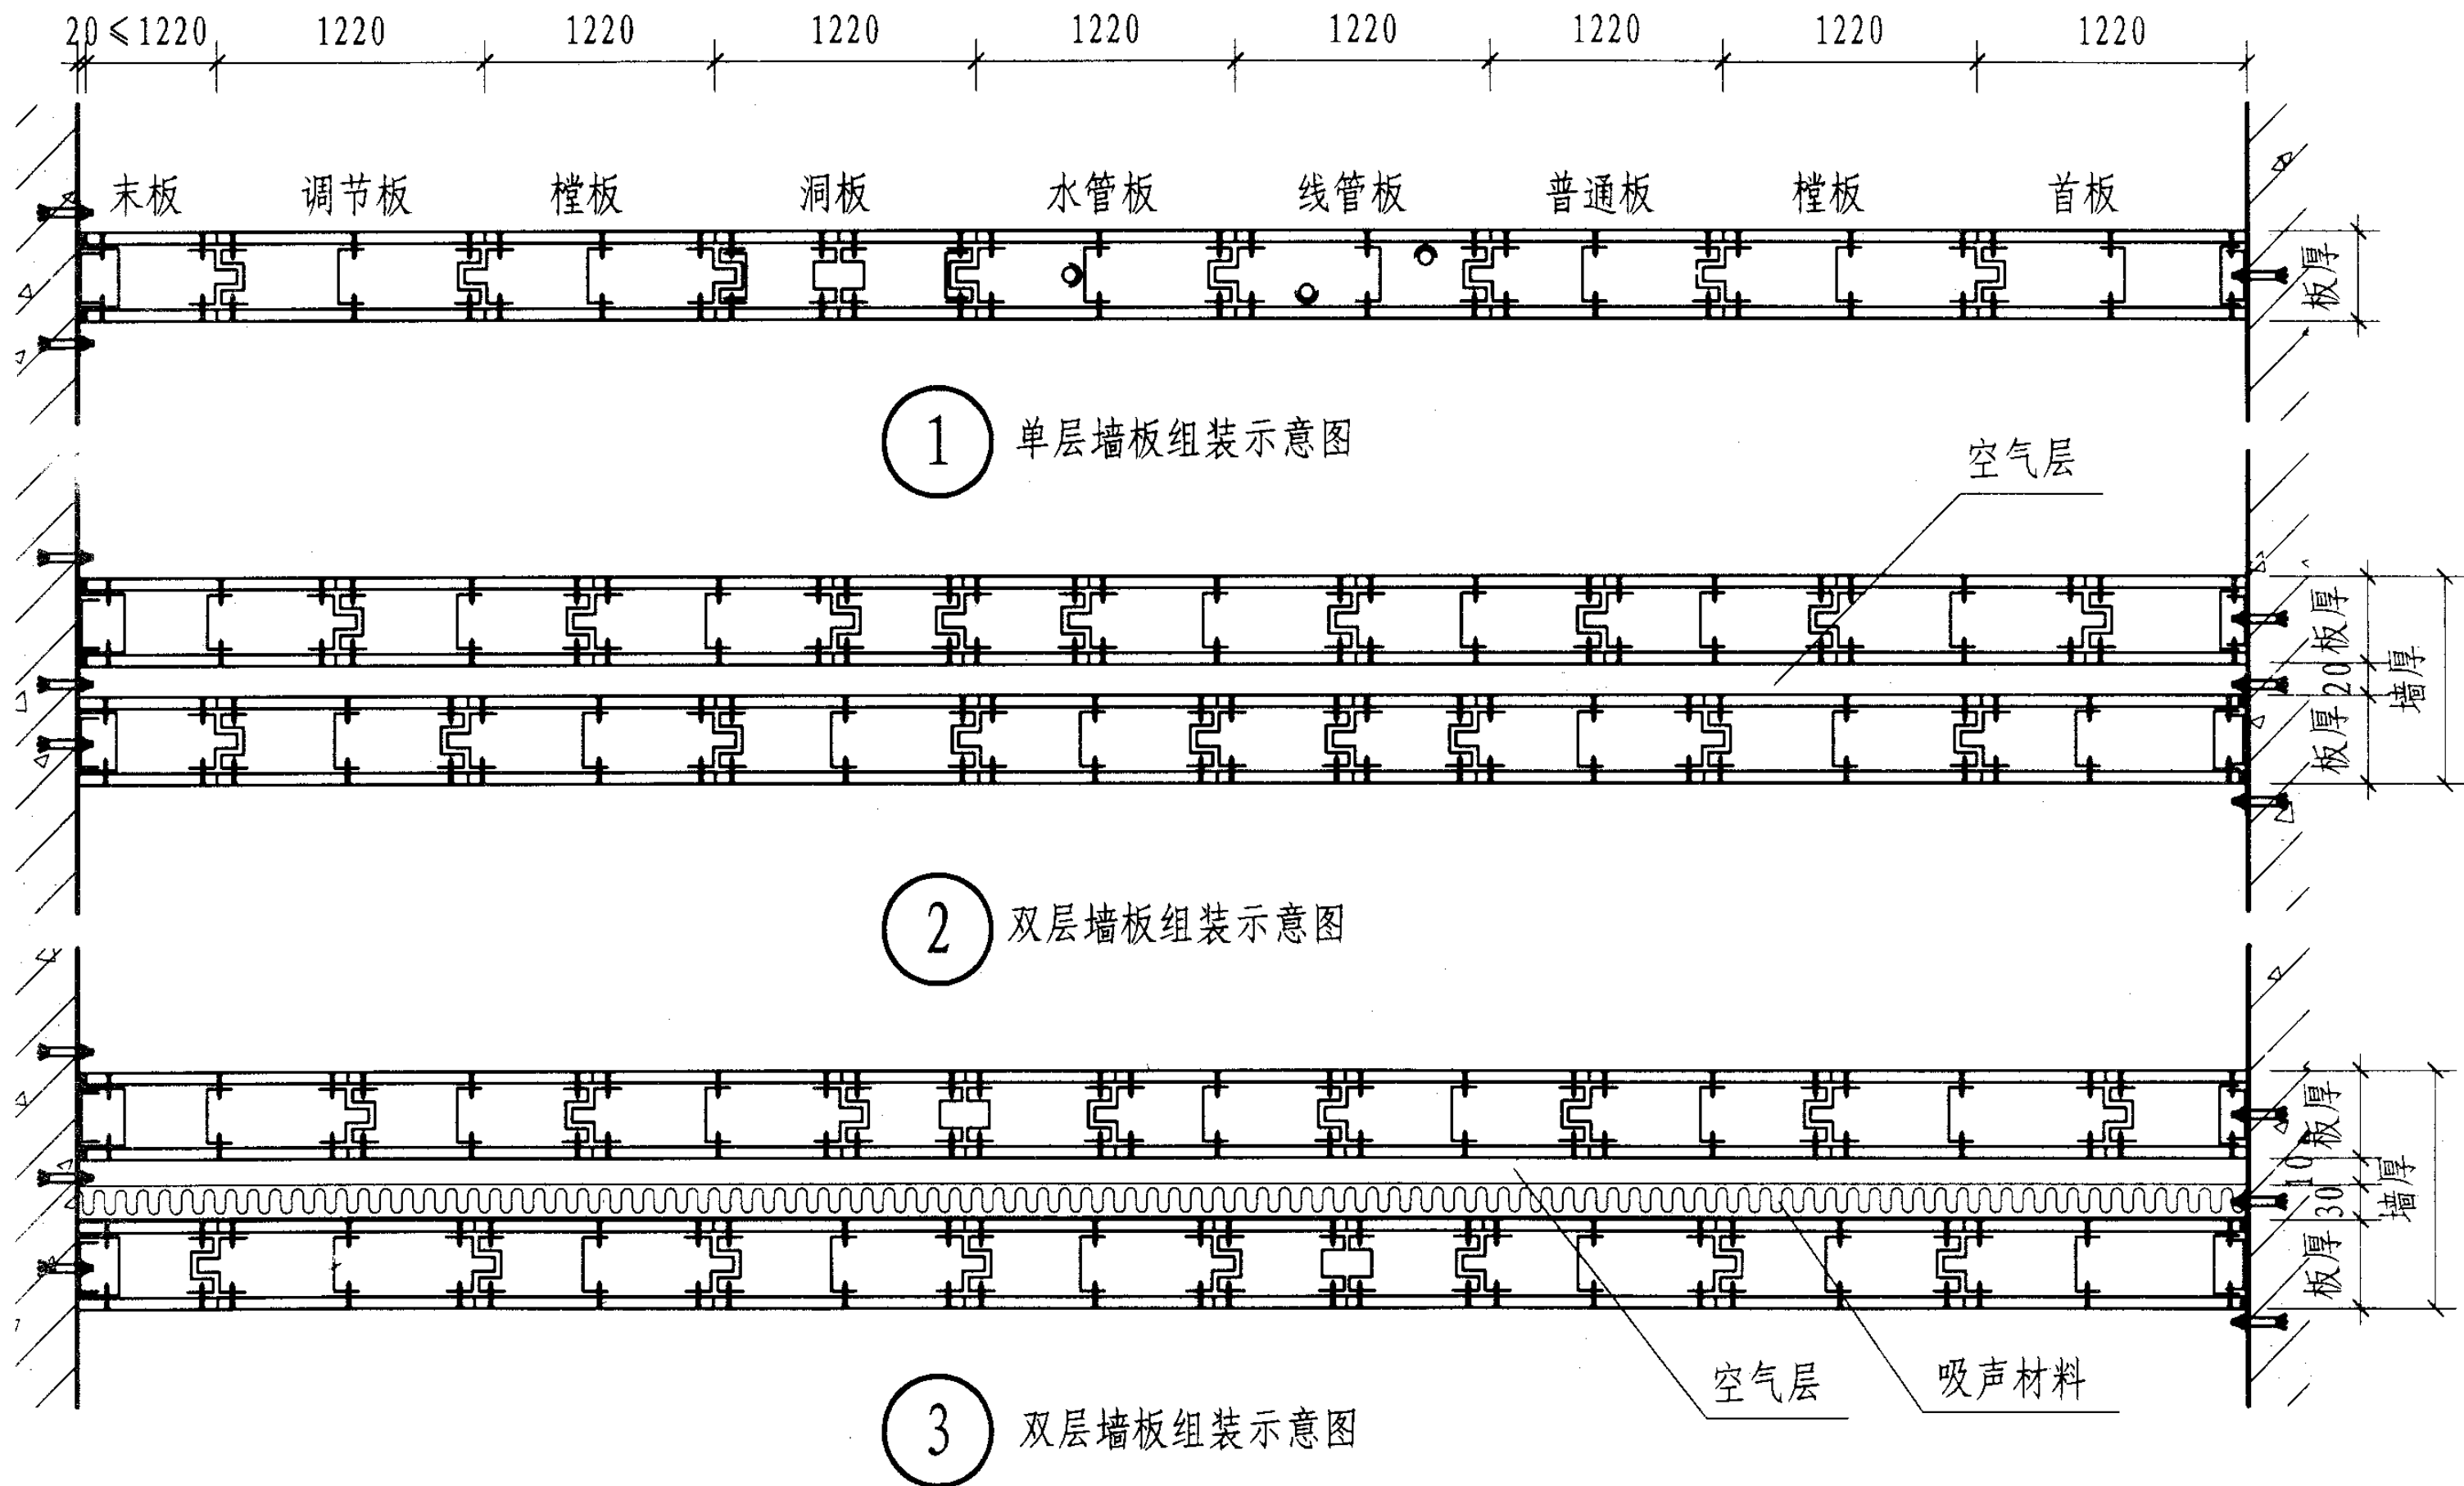

注：末板安装见

9
18

单、双层墙板组装平面图（一）

图集号

03J111-2

审核

李长发

校对


徐畅

设计


熊火生

页


10

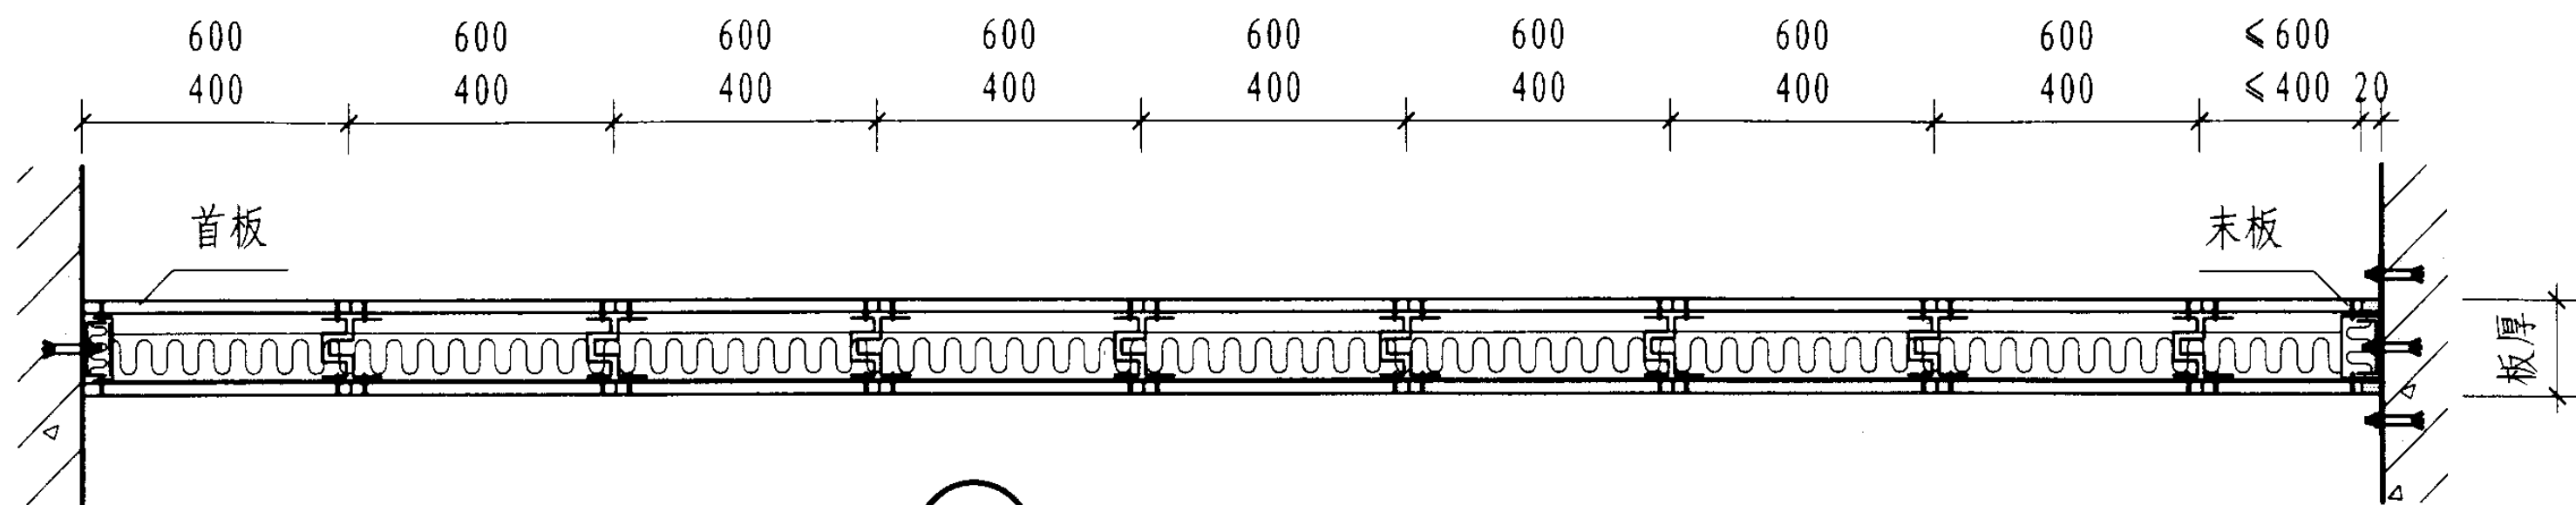

4 单层墙板组装示意图

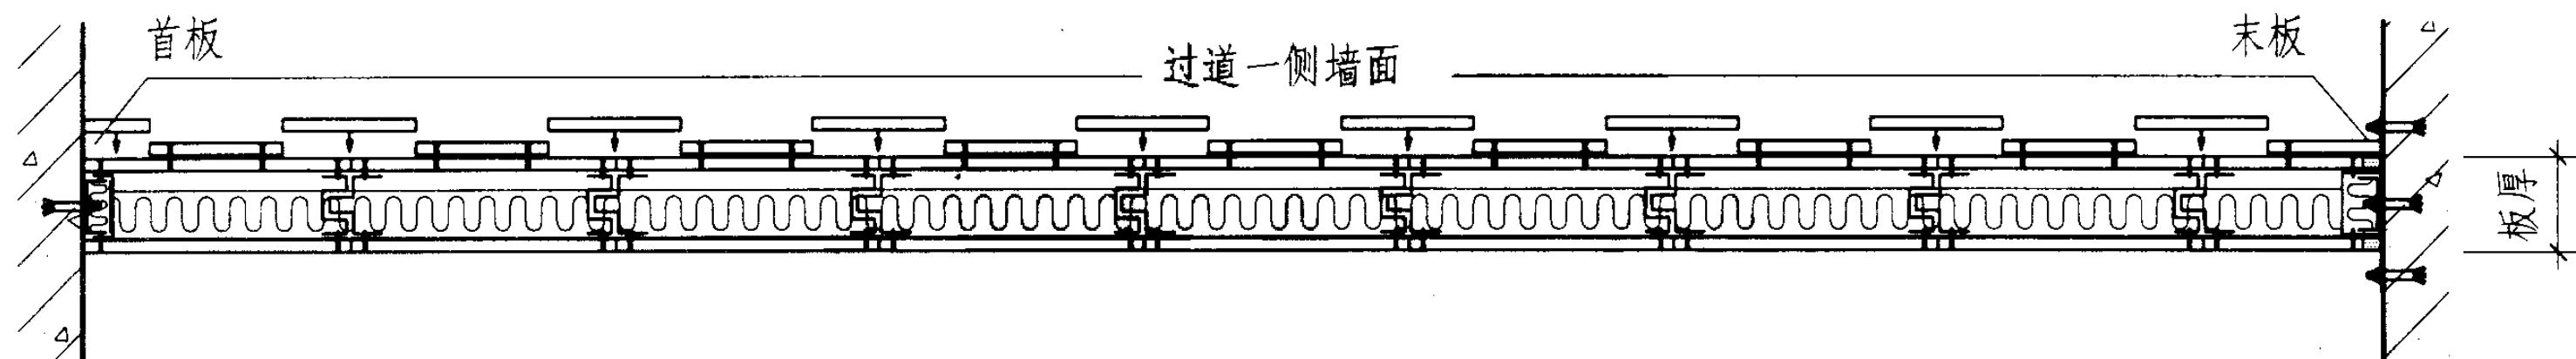

5 过道板组装示意图

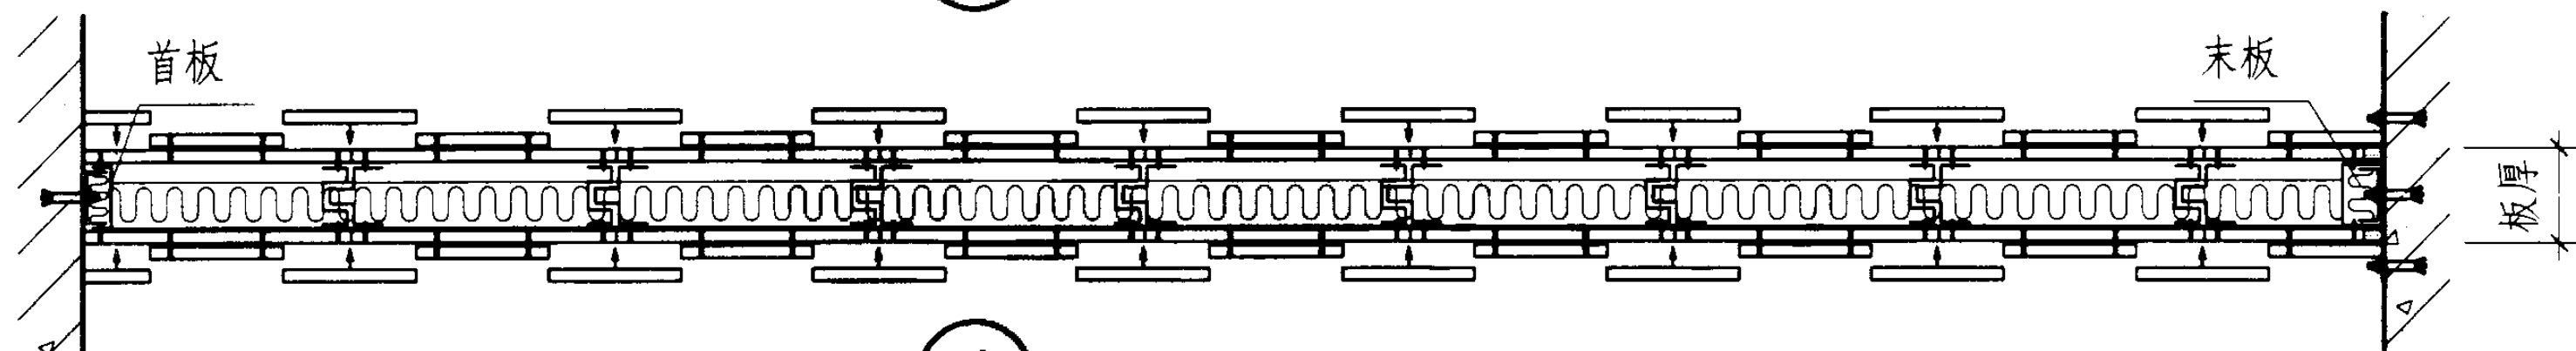

6 分户墙板组装示意图

- 注: 1. 宽度为1220mm的墙板内竖龙骨间距 $\leq 600\text{mm}$
 2. 轻钢龙骨的宽度为64、84、134mm
 3. 硅酸钙板厚度为6、8、10、12mm

4. 末板安装见

9
18

单、双层墙板组装平面图 (二)

图集号 03J111-2

审核 李长发

校对

徐畅



徐畅

设计

熊火生

页


11

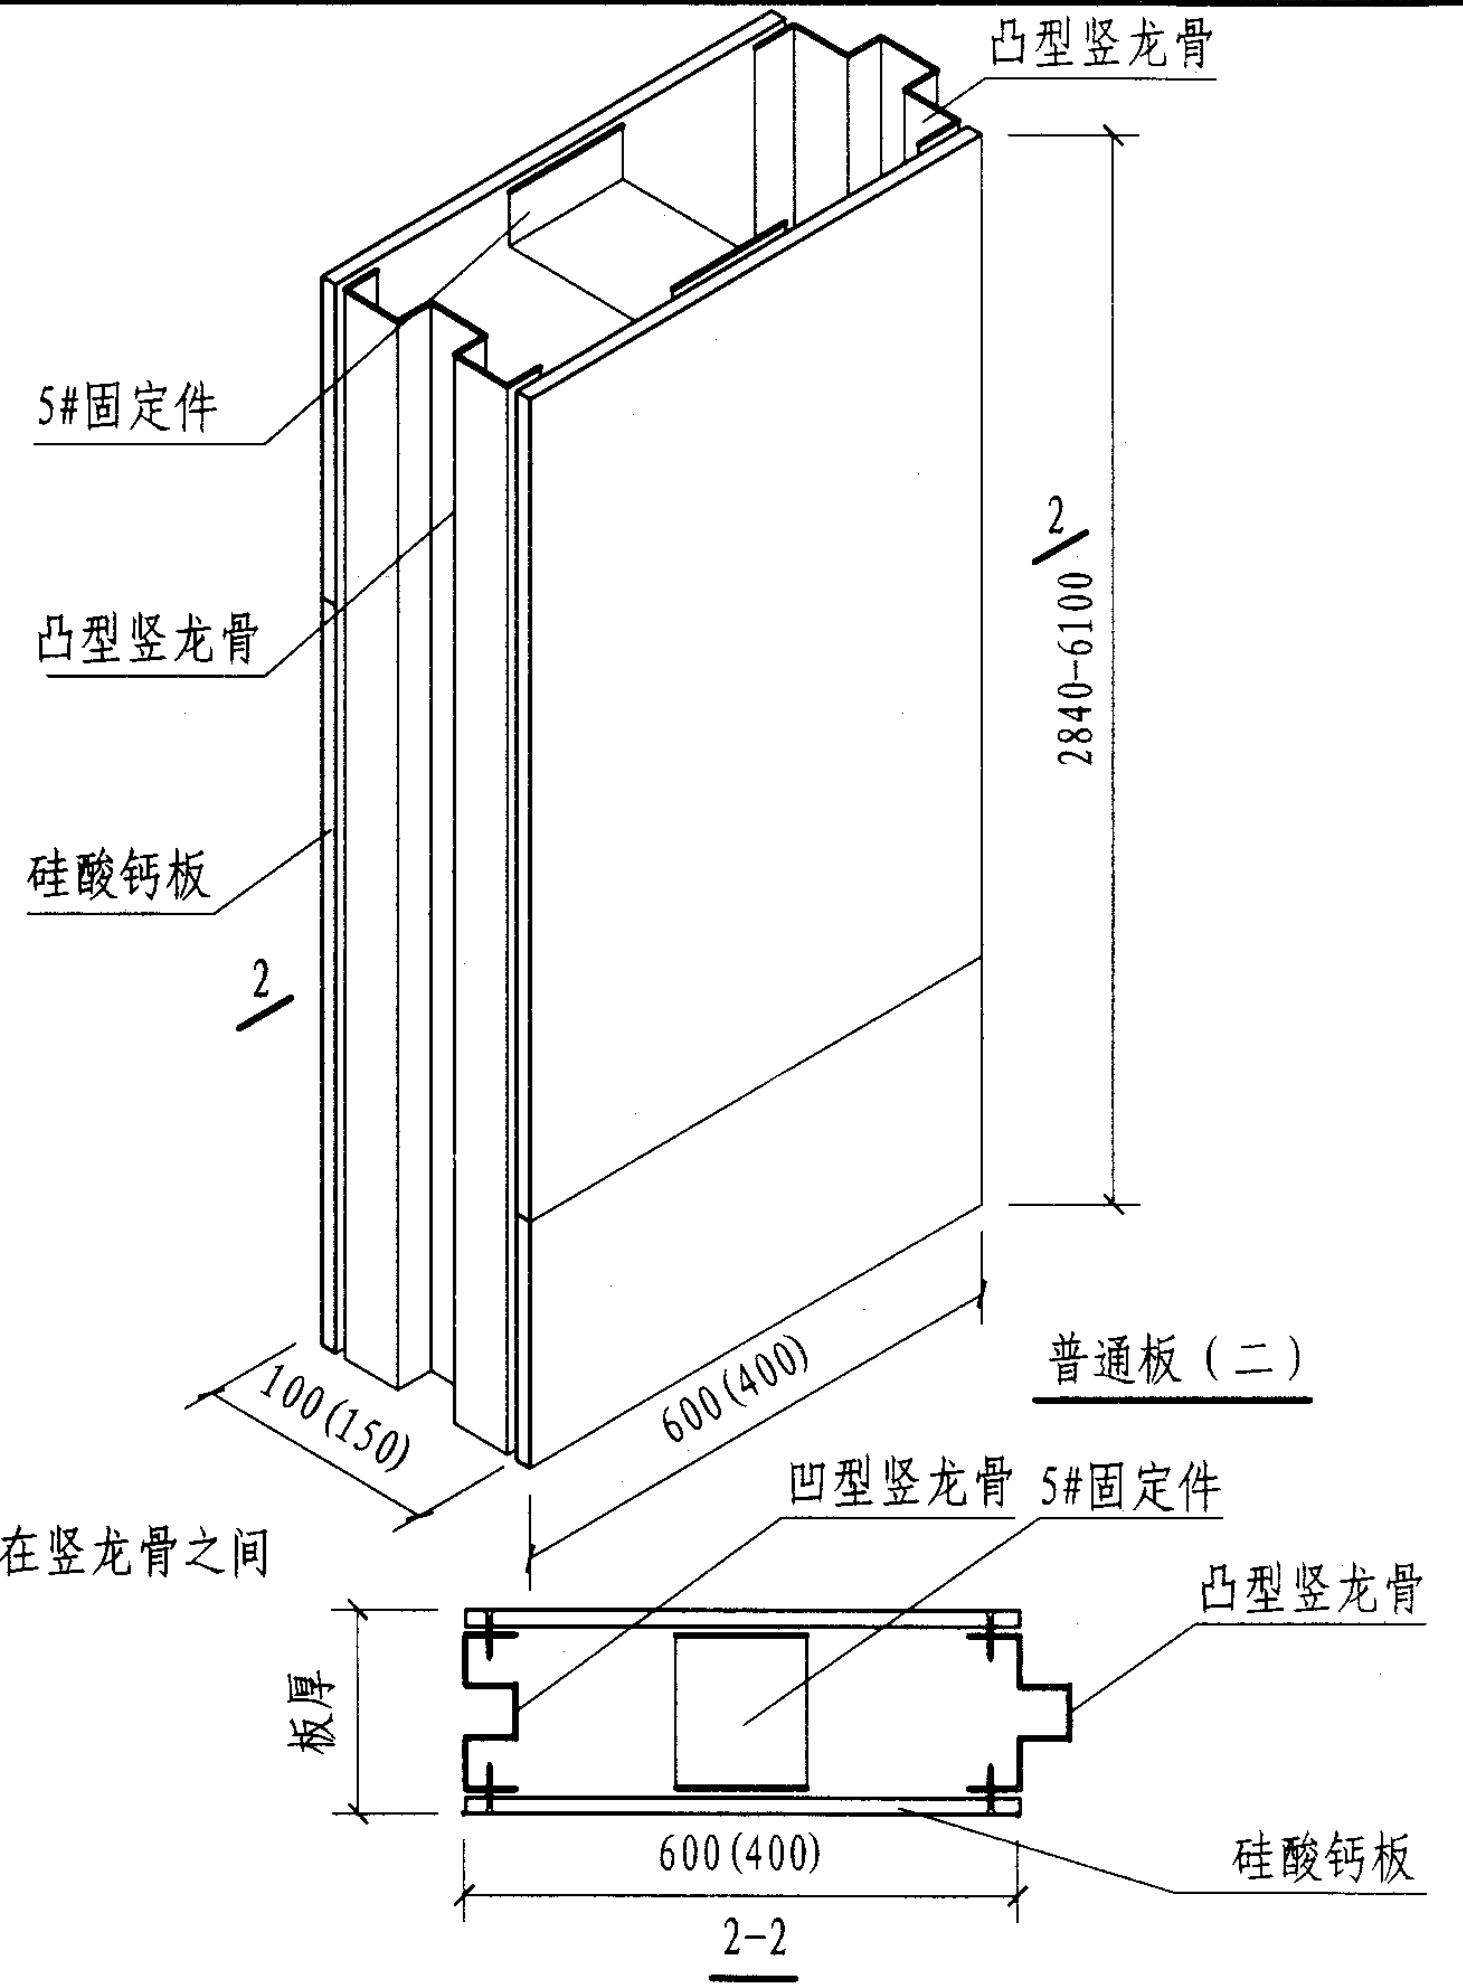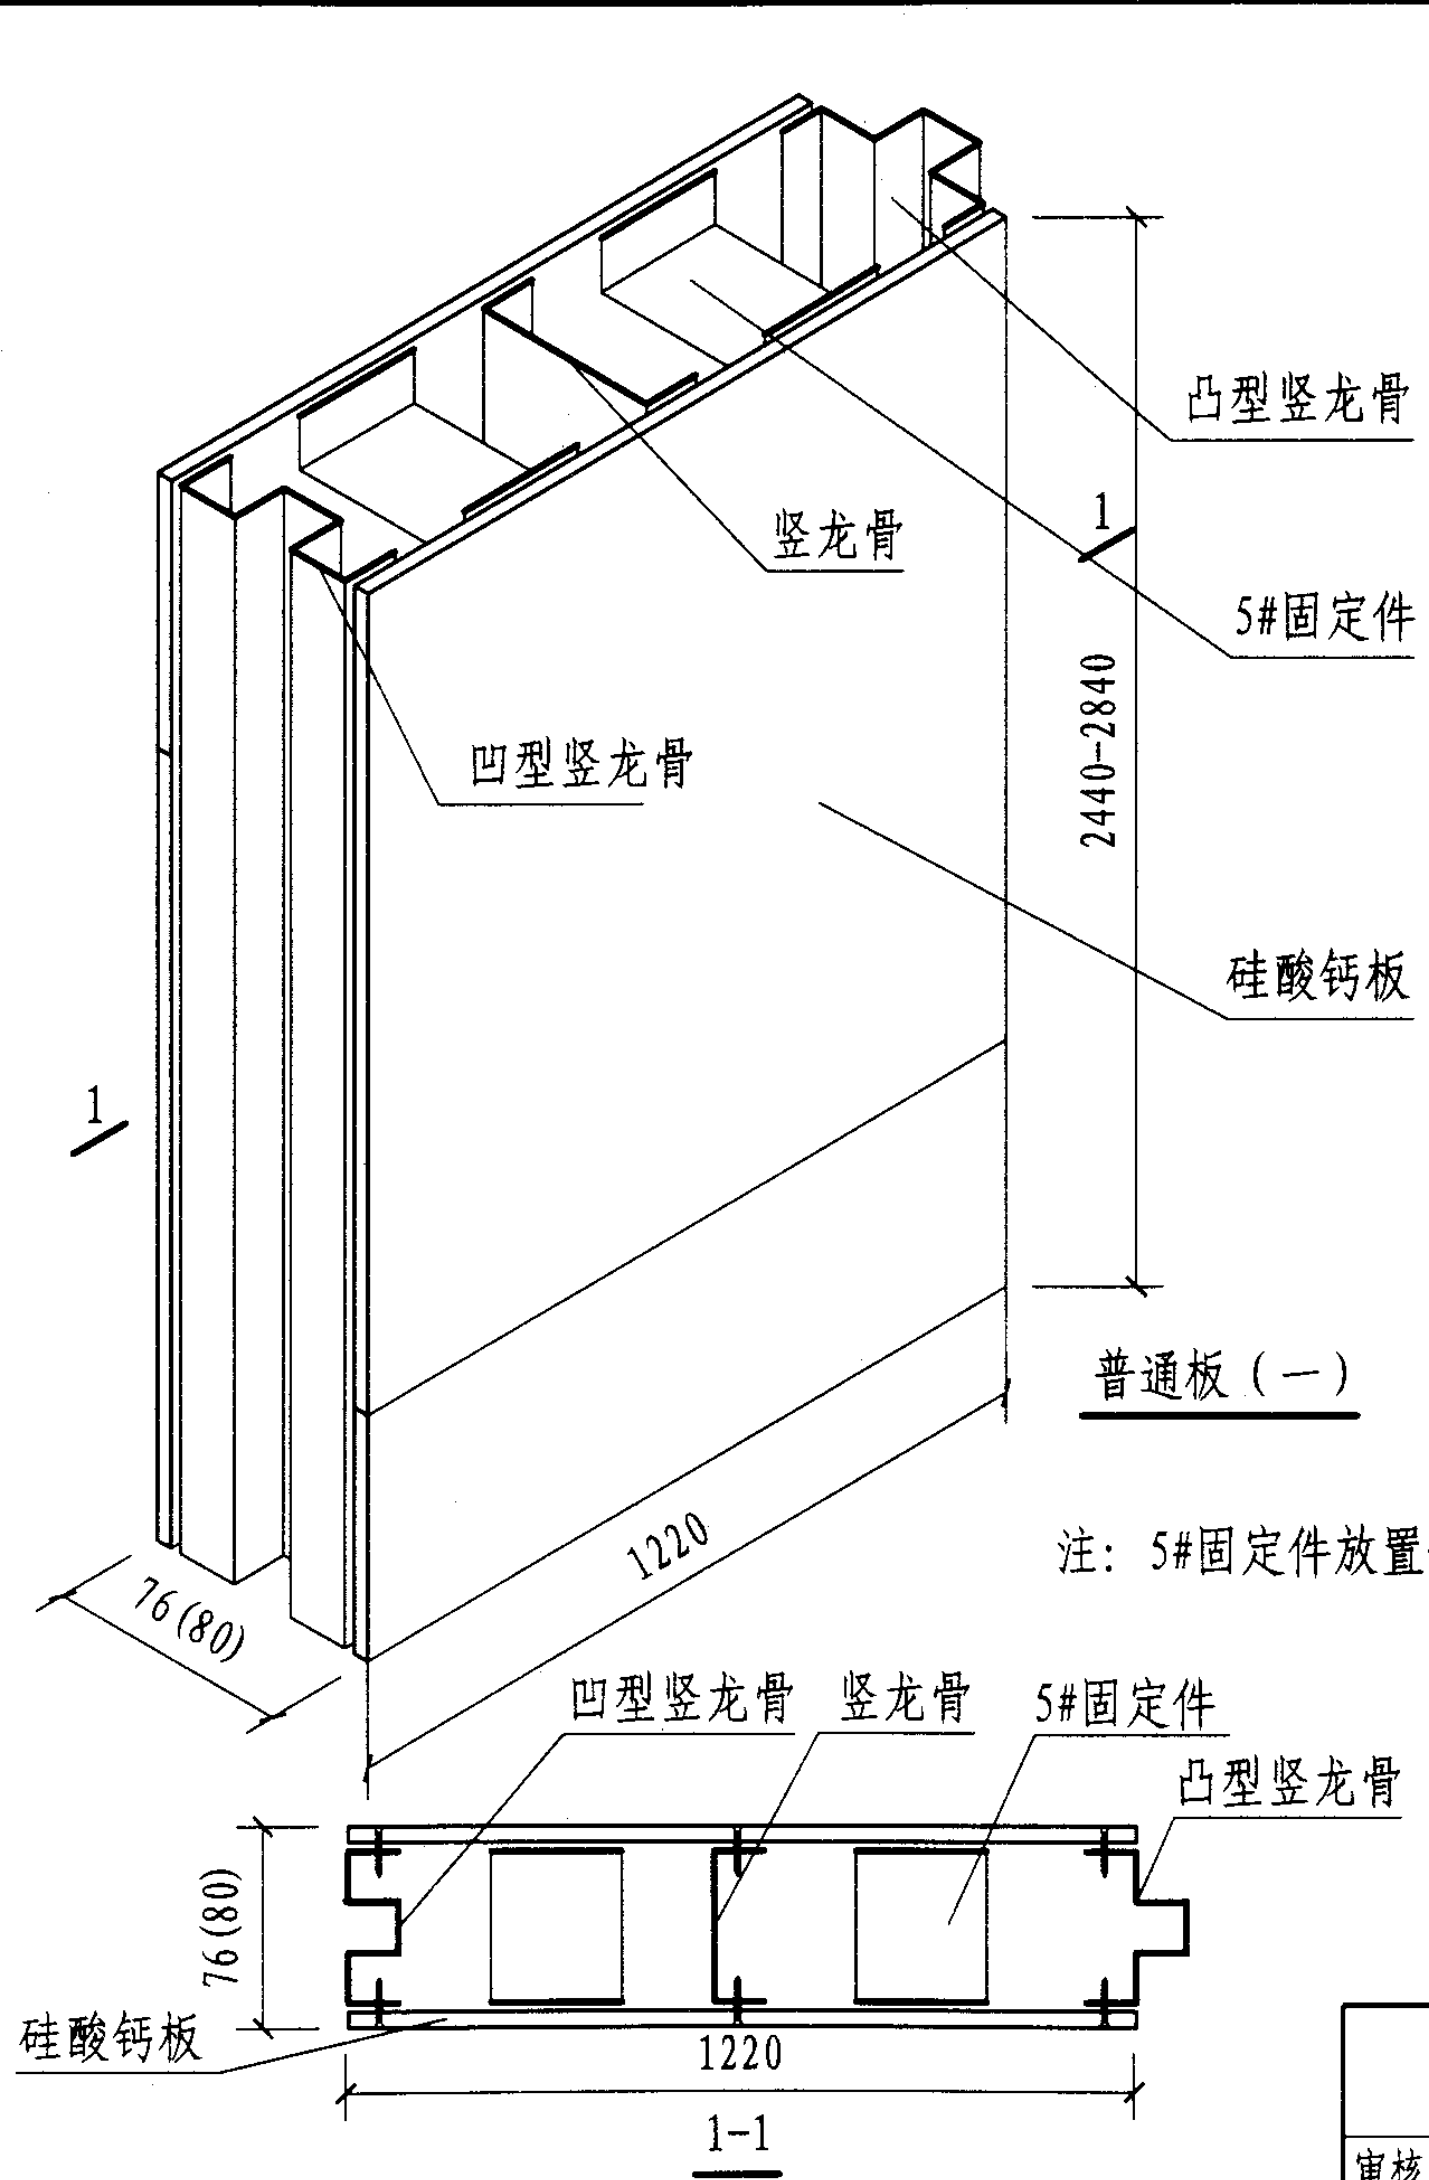

注: 5#固定件放置位置在竖龙骨之间

普通墙板规格


普通墙板规格								图集号	03J111-2
审核	李长发	徐畅	徐畅	设计	熊火生	页	12		

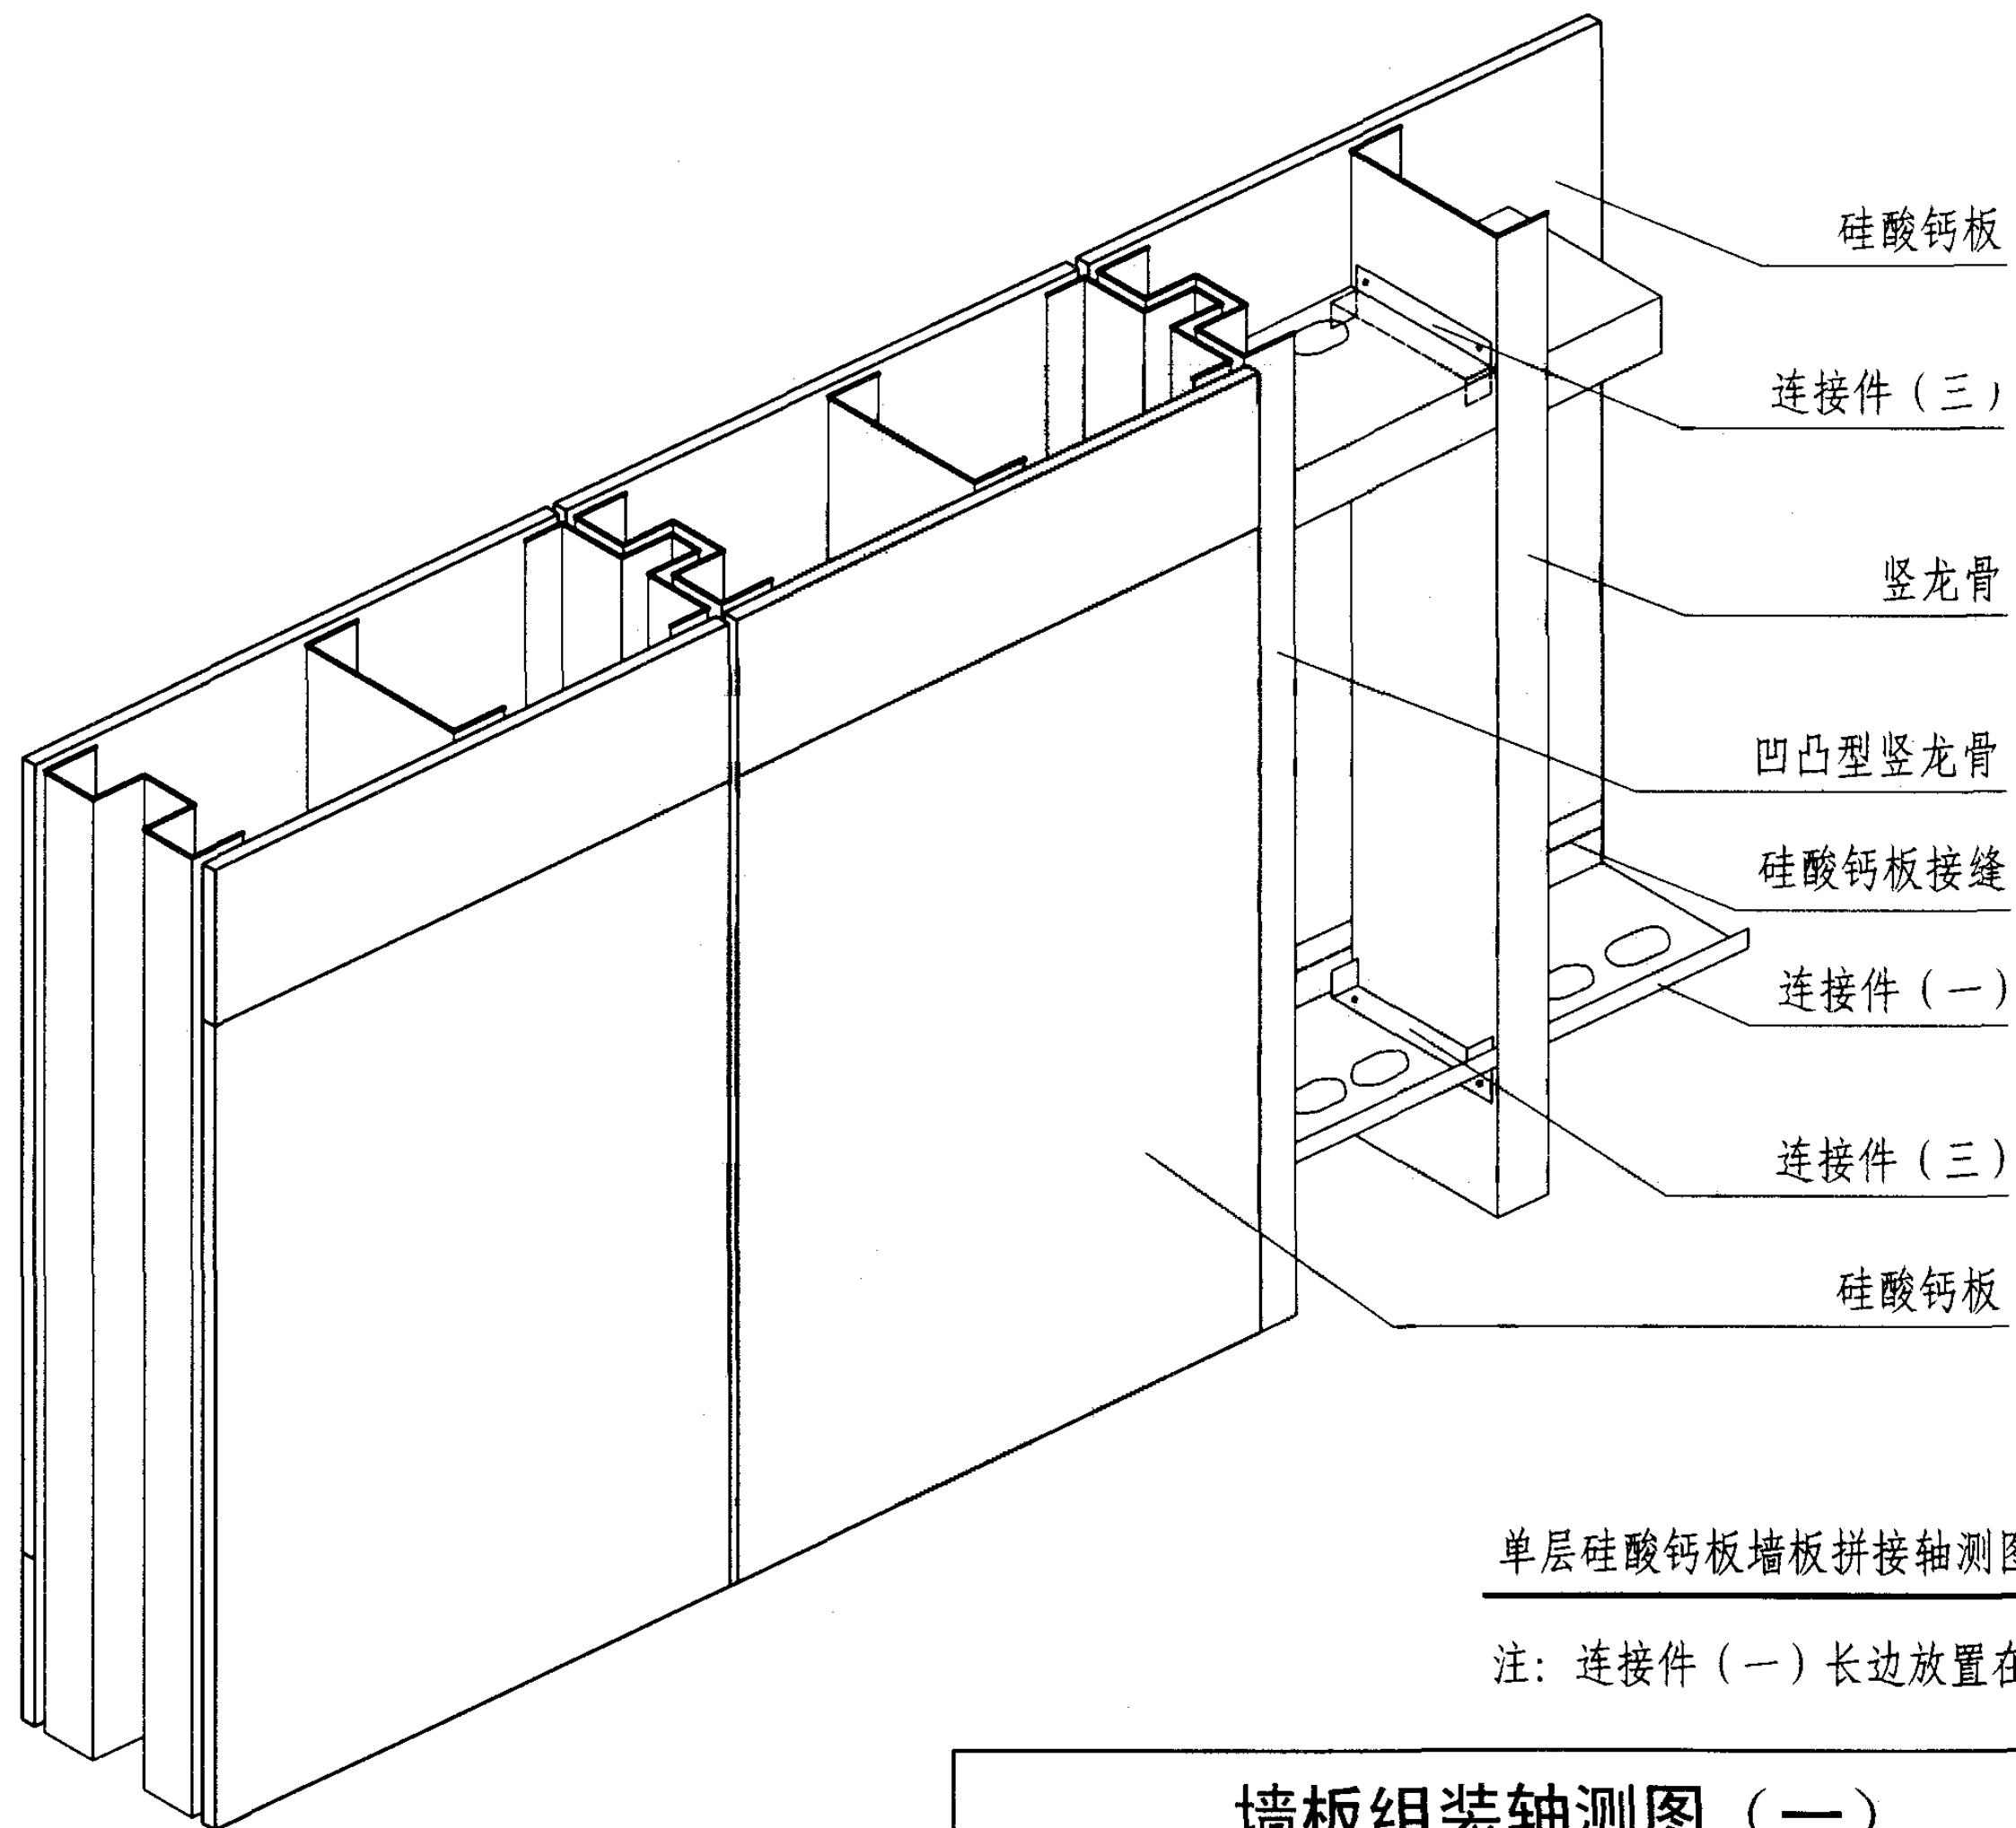

单层硅酸钙板墙板拼接轴测图

注：连接件（一）长边放置在硅酸钙板接缝处

墙板组装轴测图（一）								图集号	03J111-2
审核	李长发		校对	徐畅		设计	熊火生	页	13

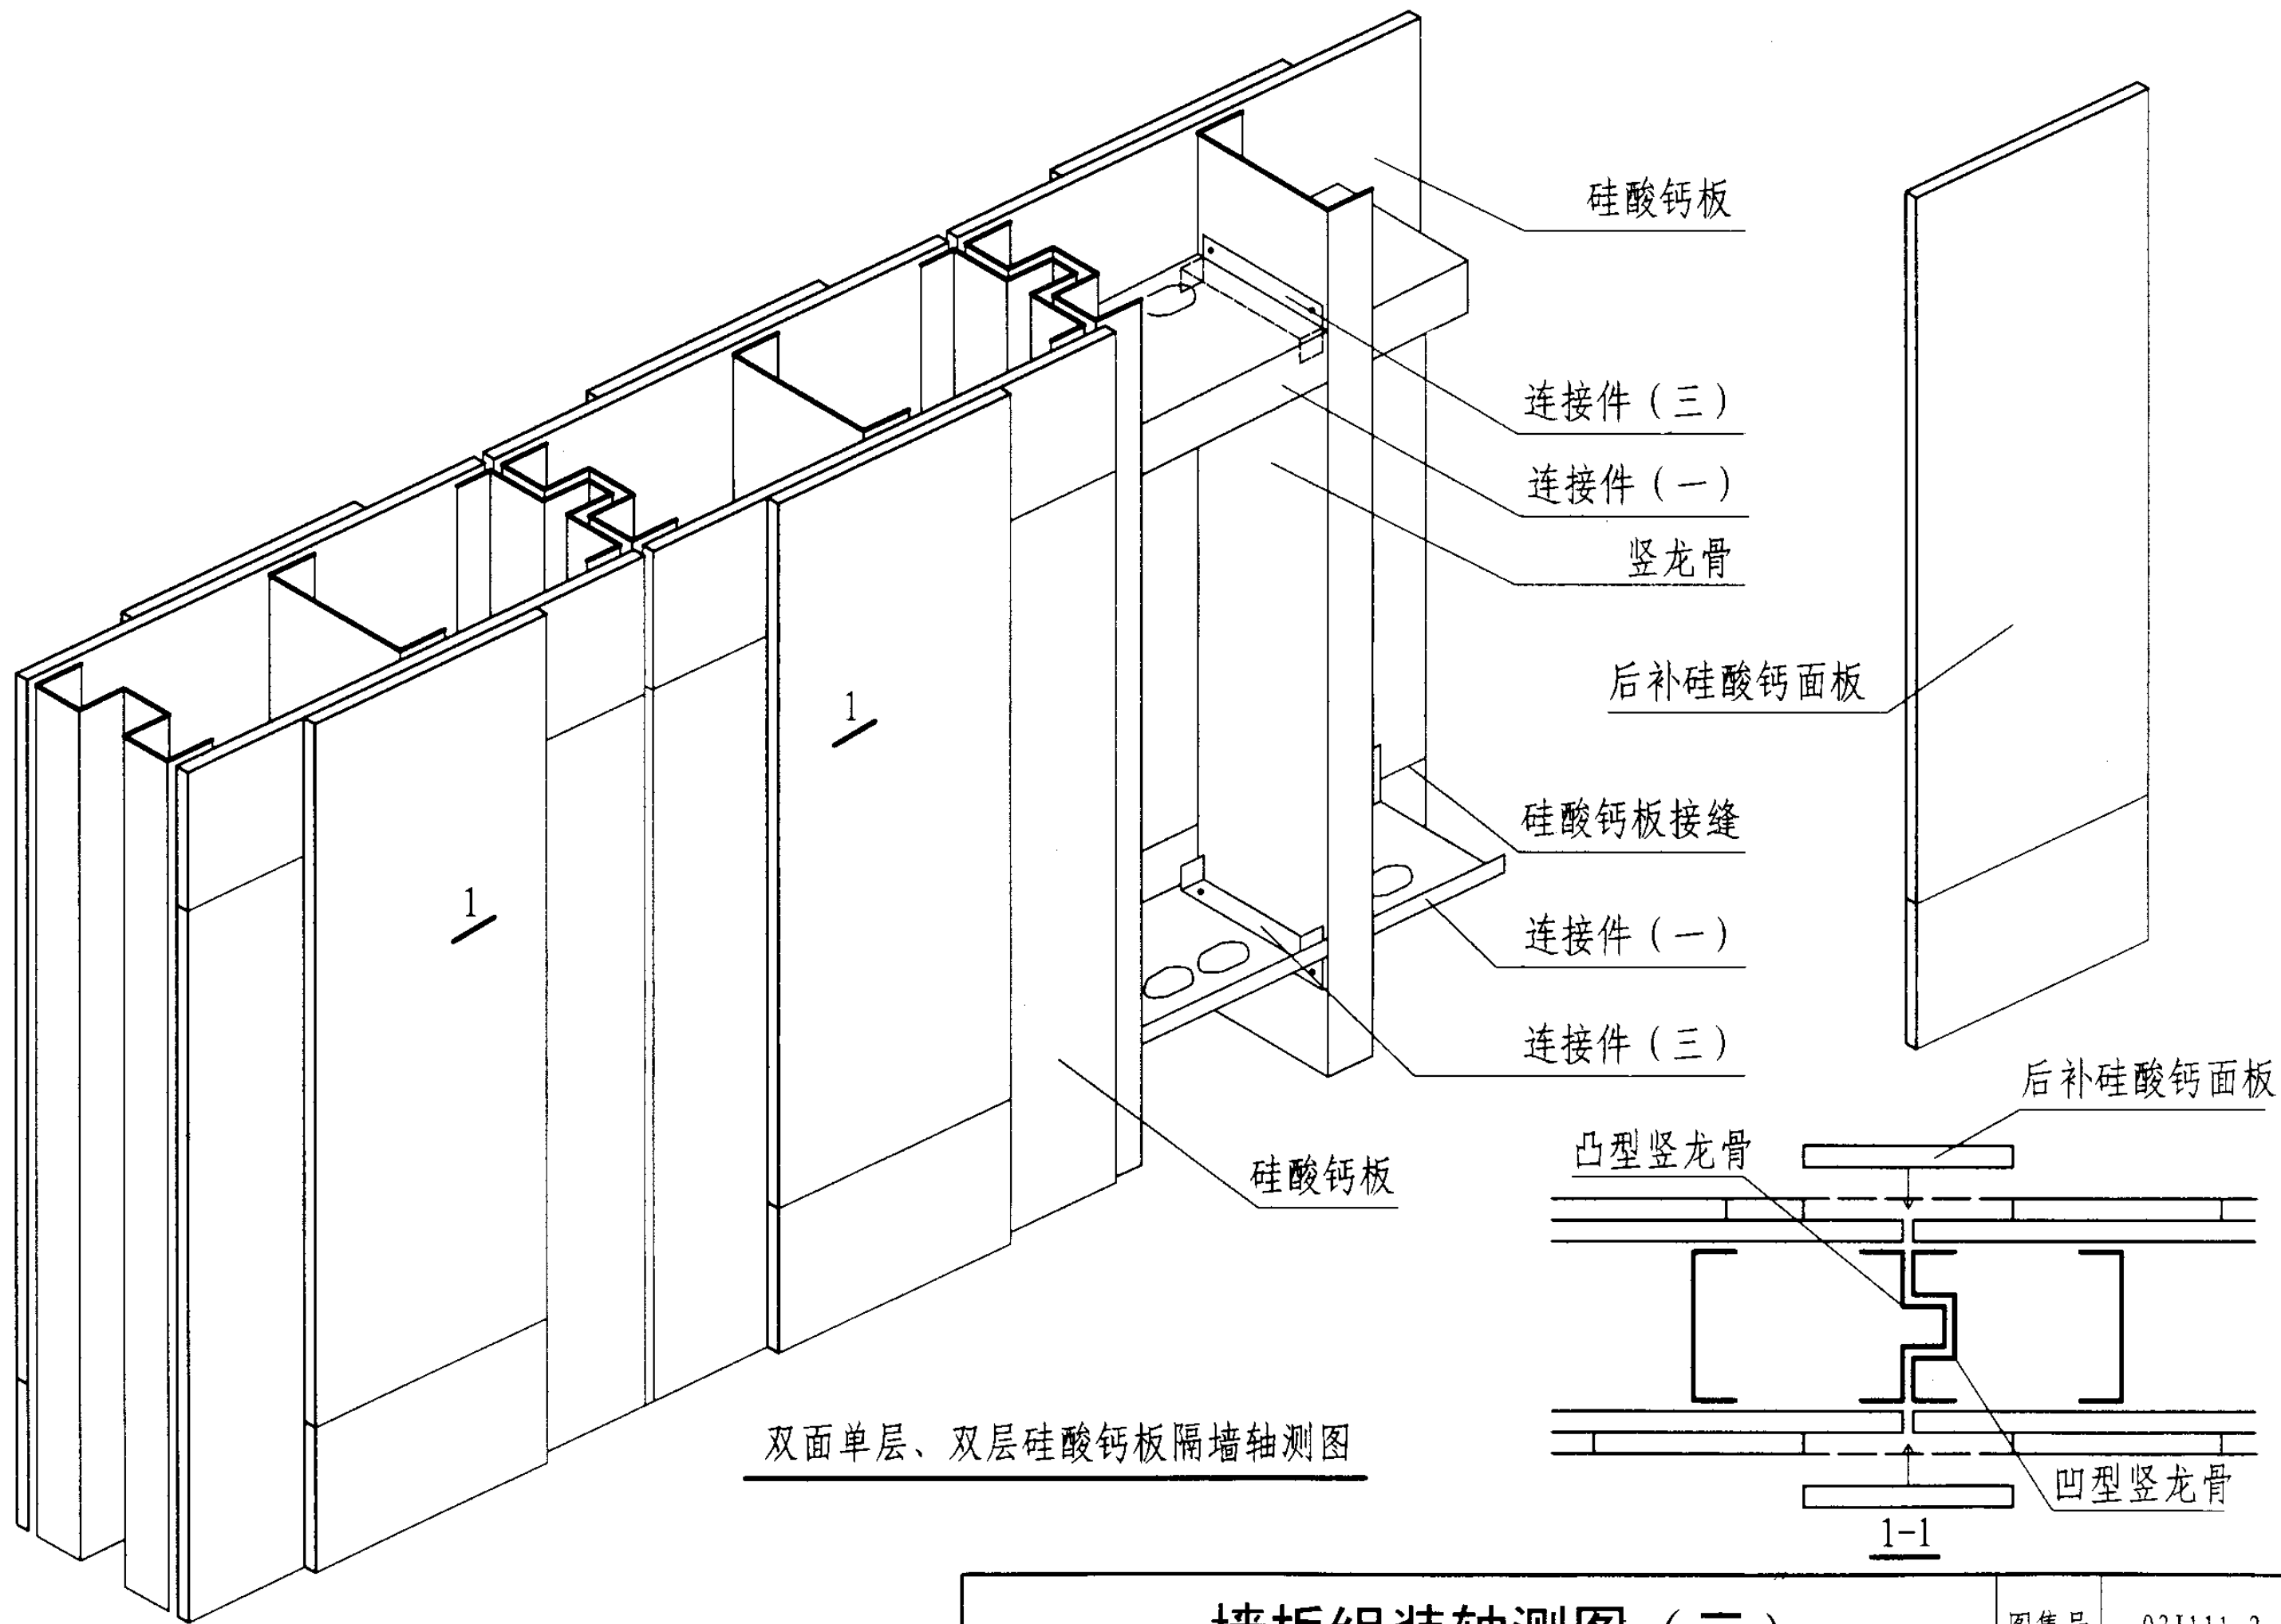



双面单层、双层硅酸钙板隔墙轴测图

墙板组装轴测图 (二)

图集号 03J111-2



审核 李长发 徐畅 设计 熊火生

页 14

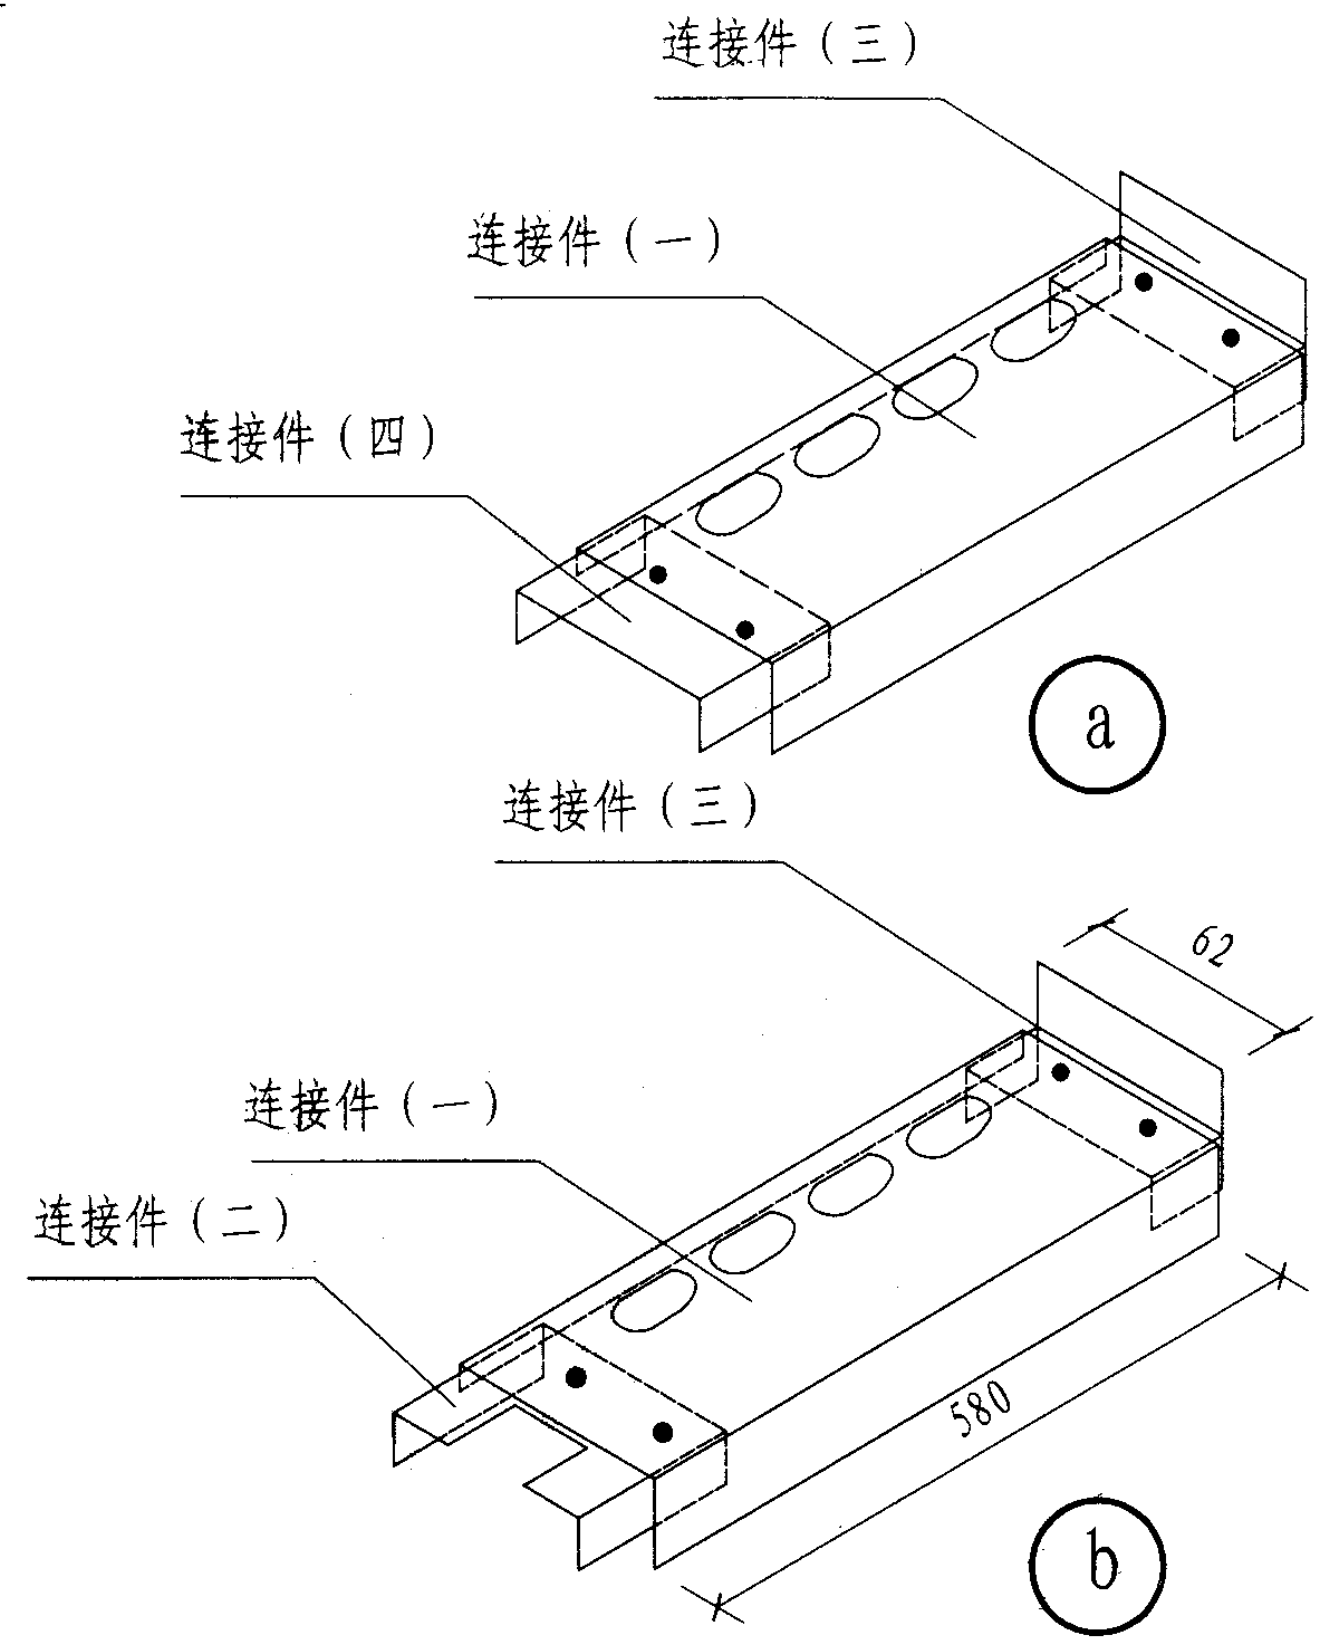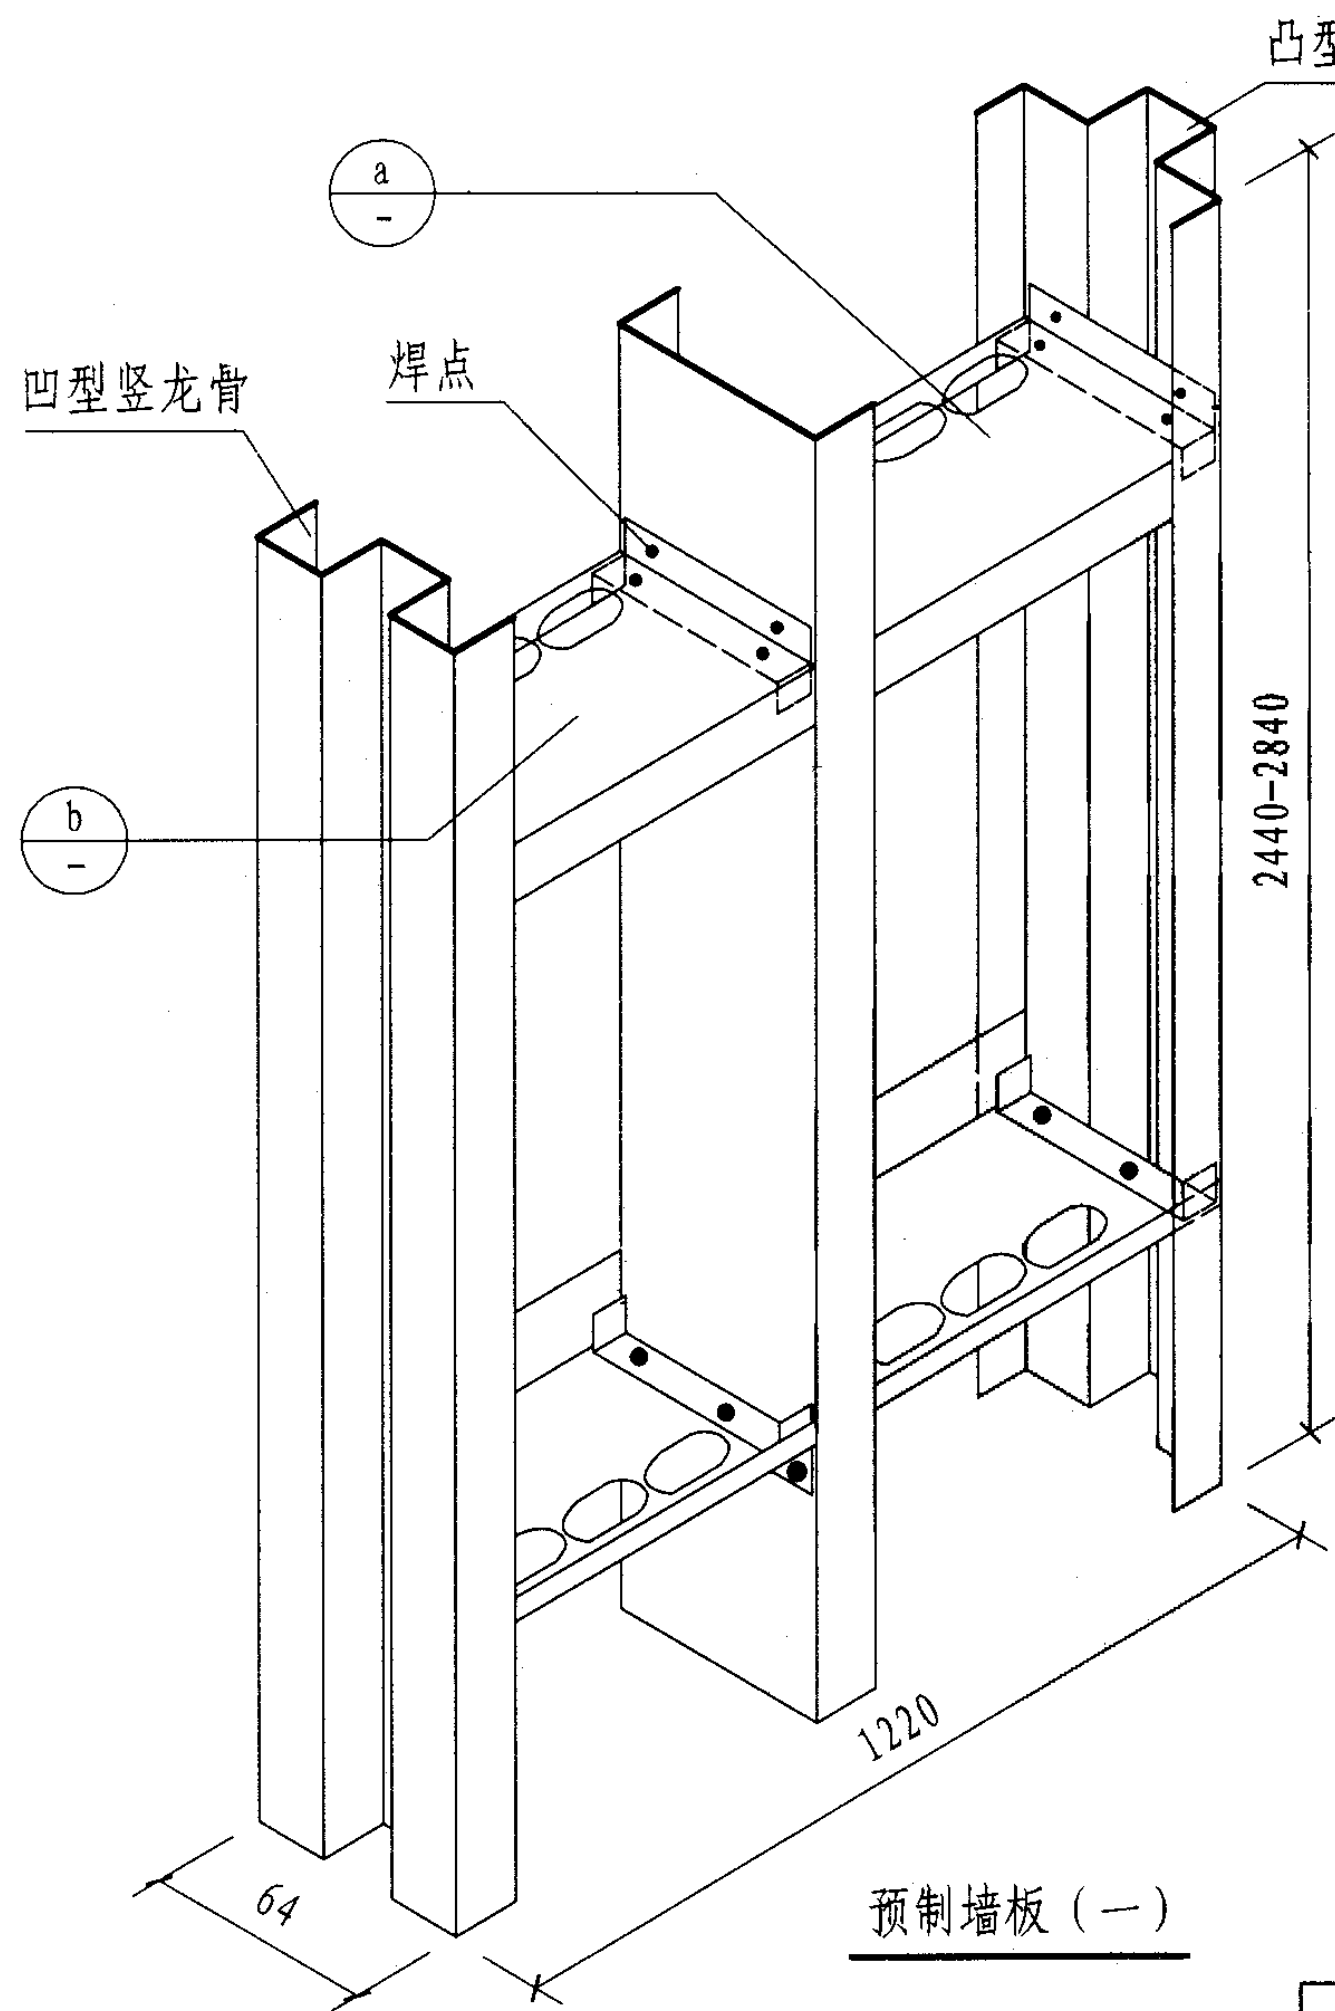

注：龙骨骨架均使用点焊连接。

墙板骨架构造（一）								图集号	03J111-2
审核	李长发	徐畅	校对	徐畅	设计	熊火生	页	15	

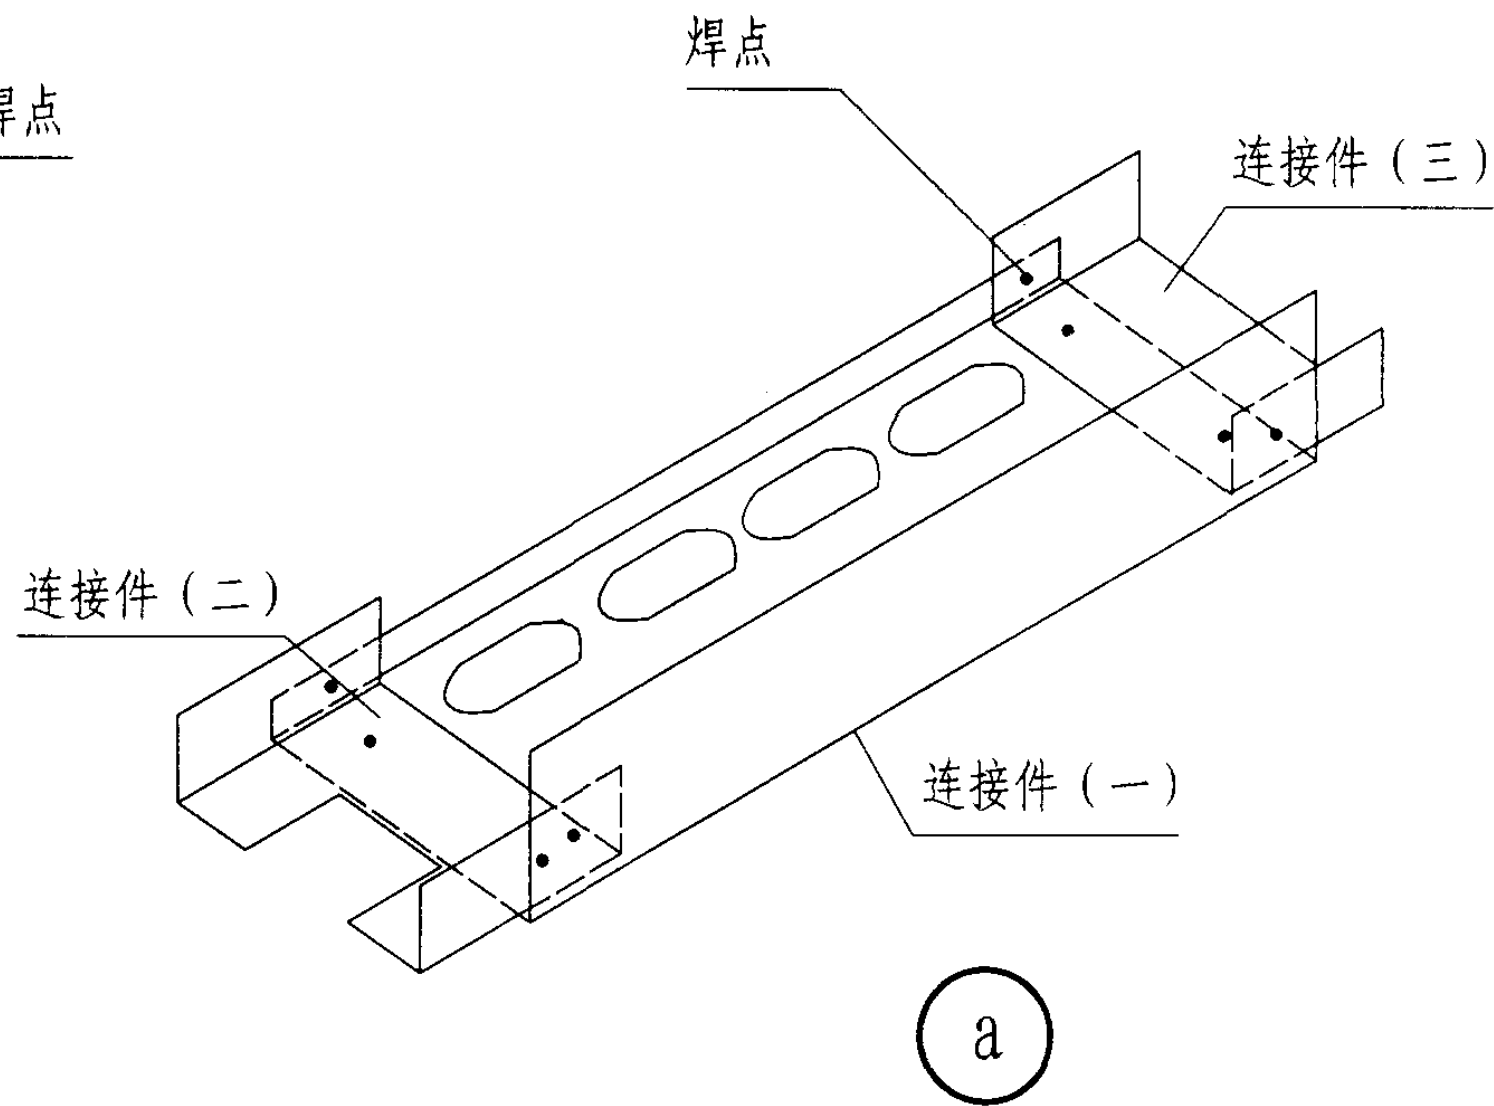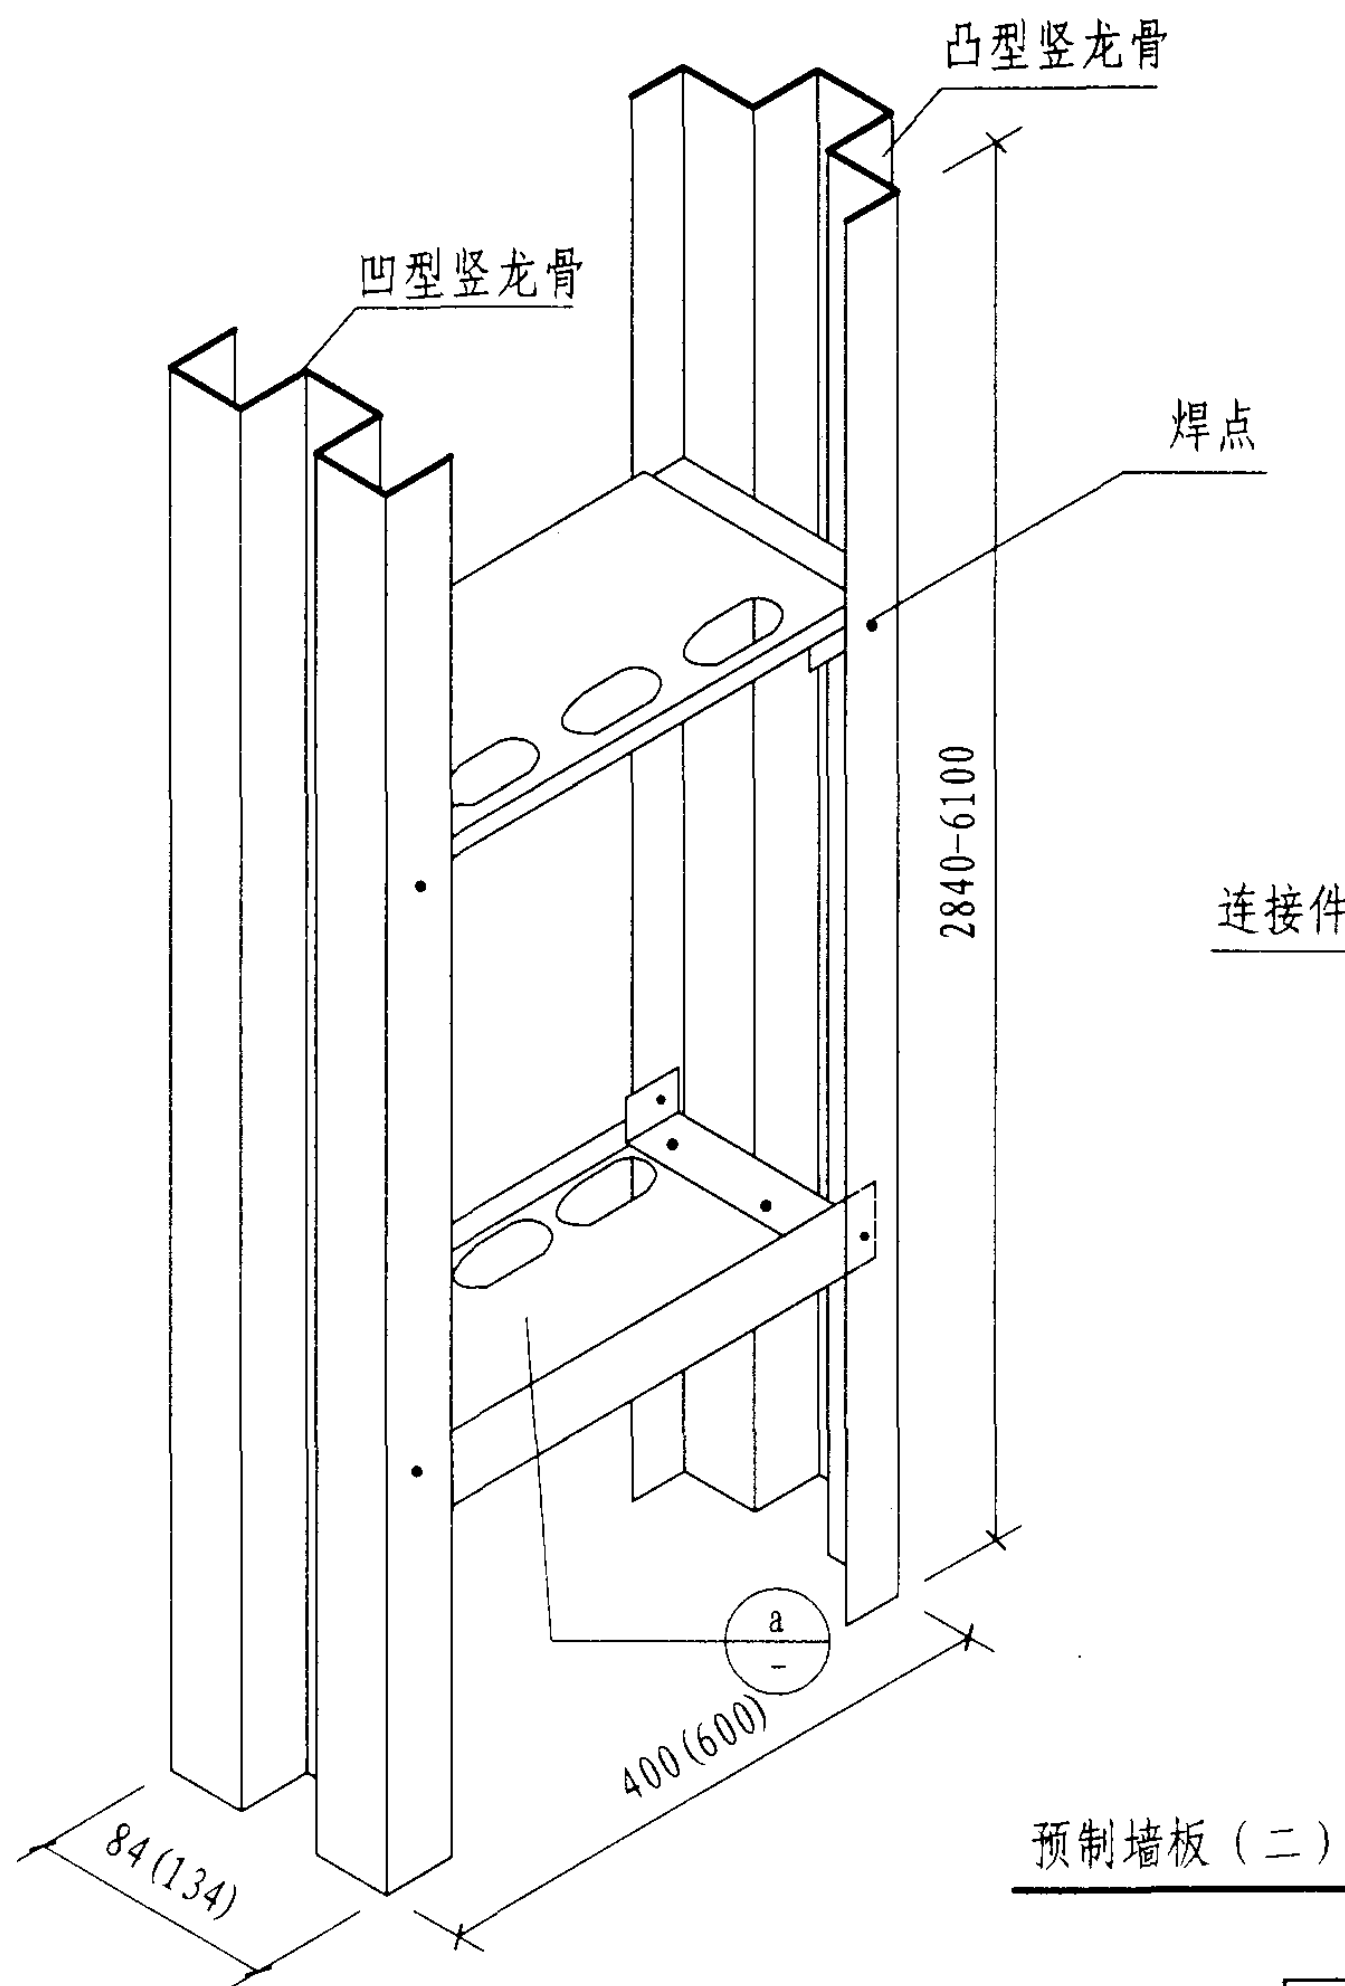

注：龙骨骨架均使用点焊连接

墙板骨架构造 (二)

图集号

03J111-2

审核

李长发

校对

徐畅

徐畅

徐畅

徐畅

徐畅



徐畅

徐畅


徐畅

页

16

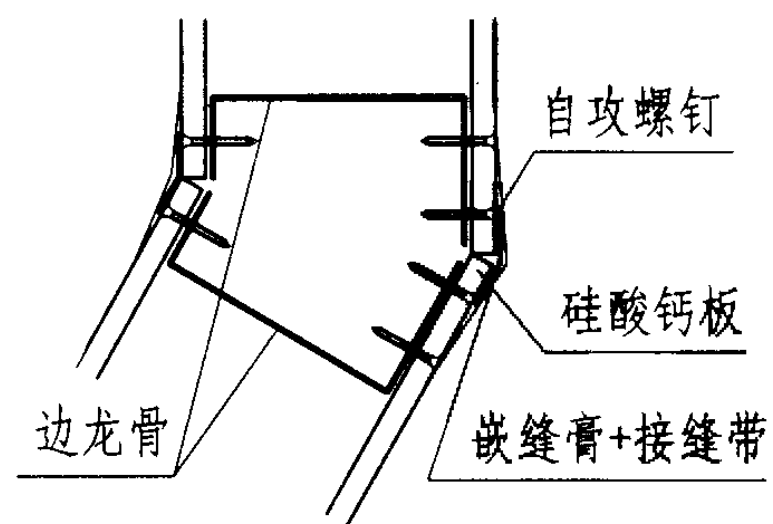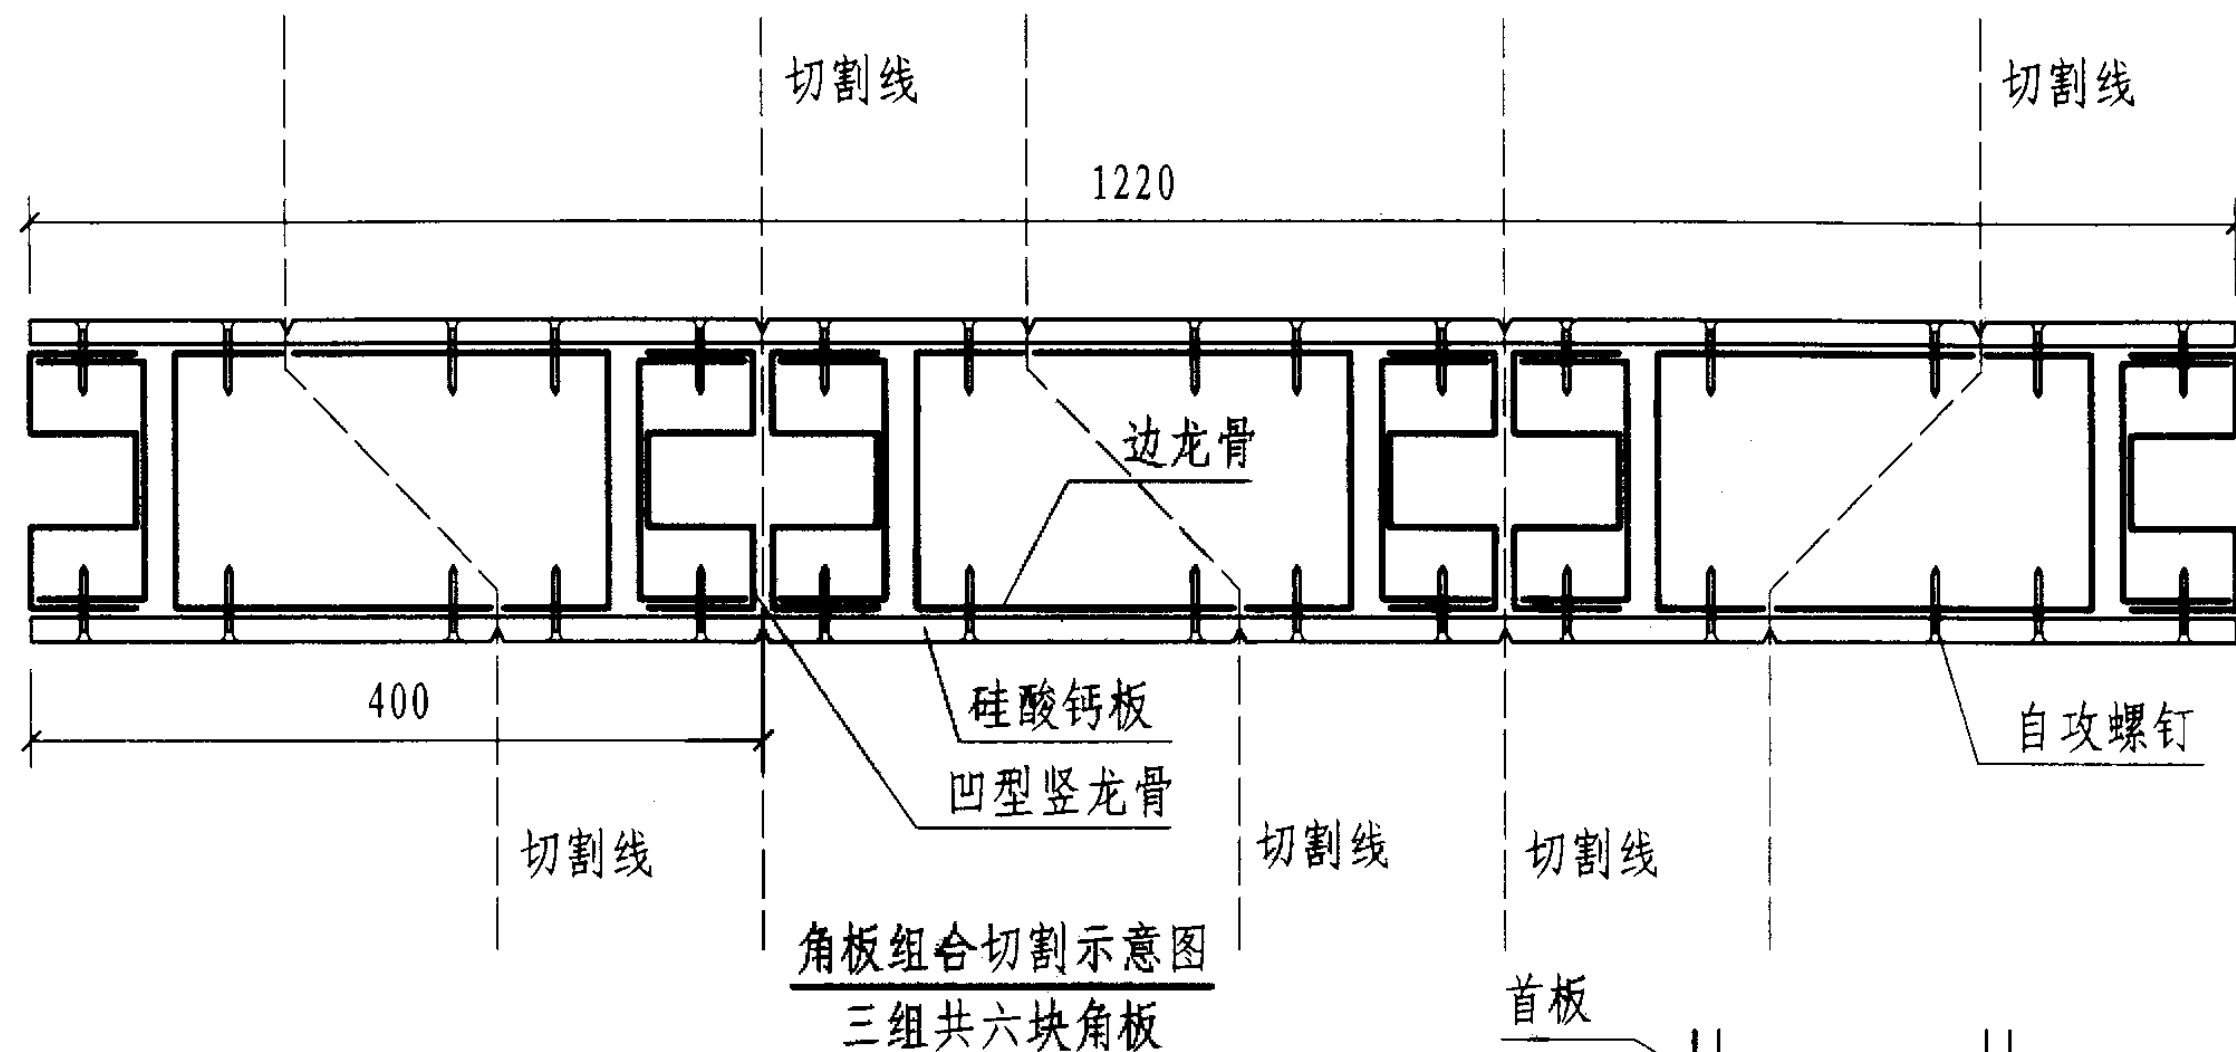

7 角板对接示意

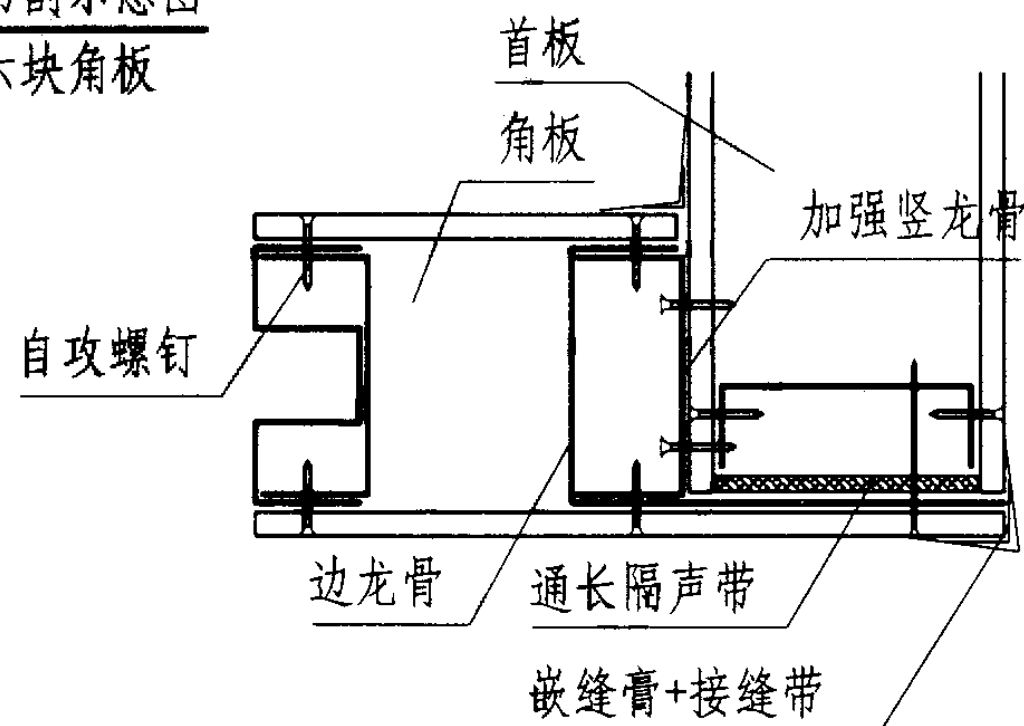

8 角板与首板连接

角板连接节点

图集号

03J111-2

审核

李长发

校对




徐畅

设计


熊火生

页

17

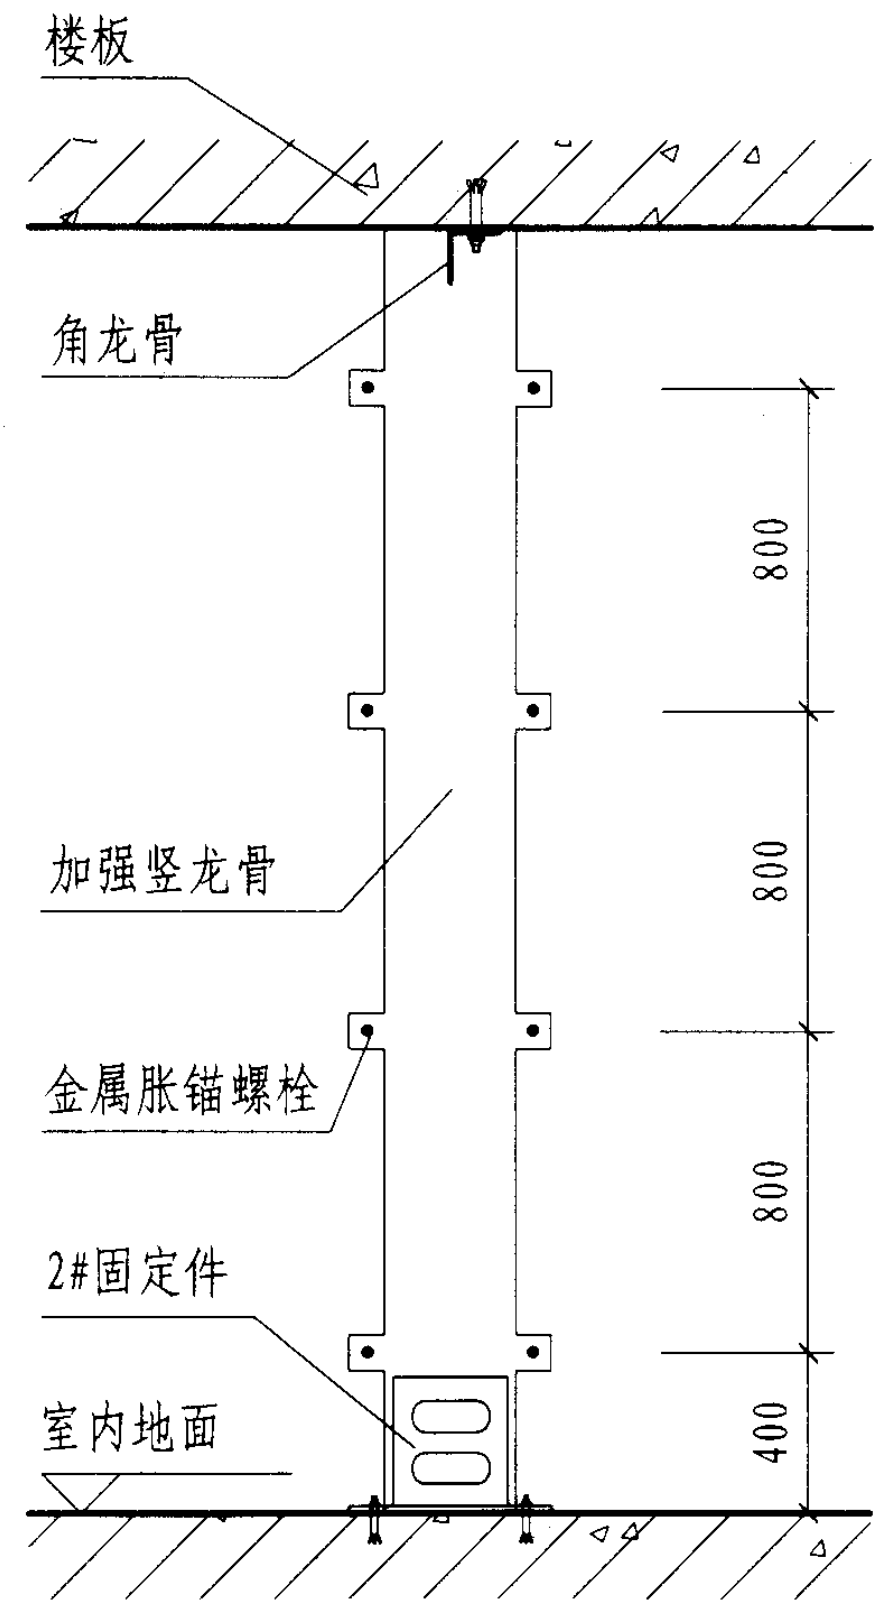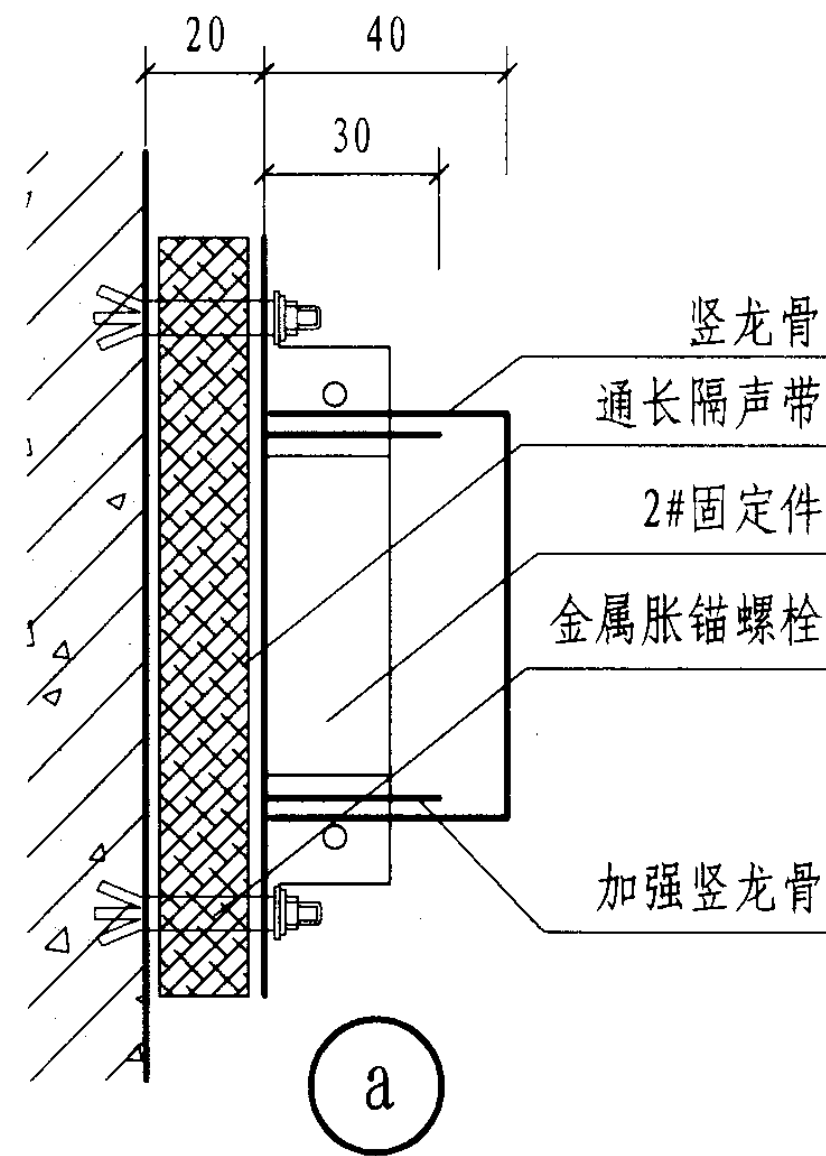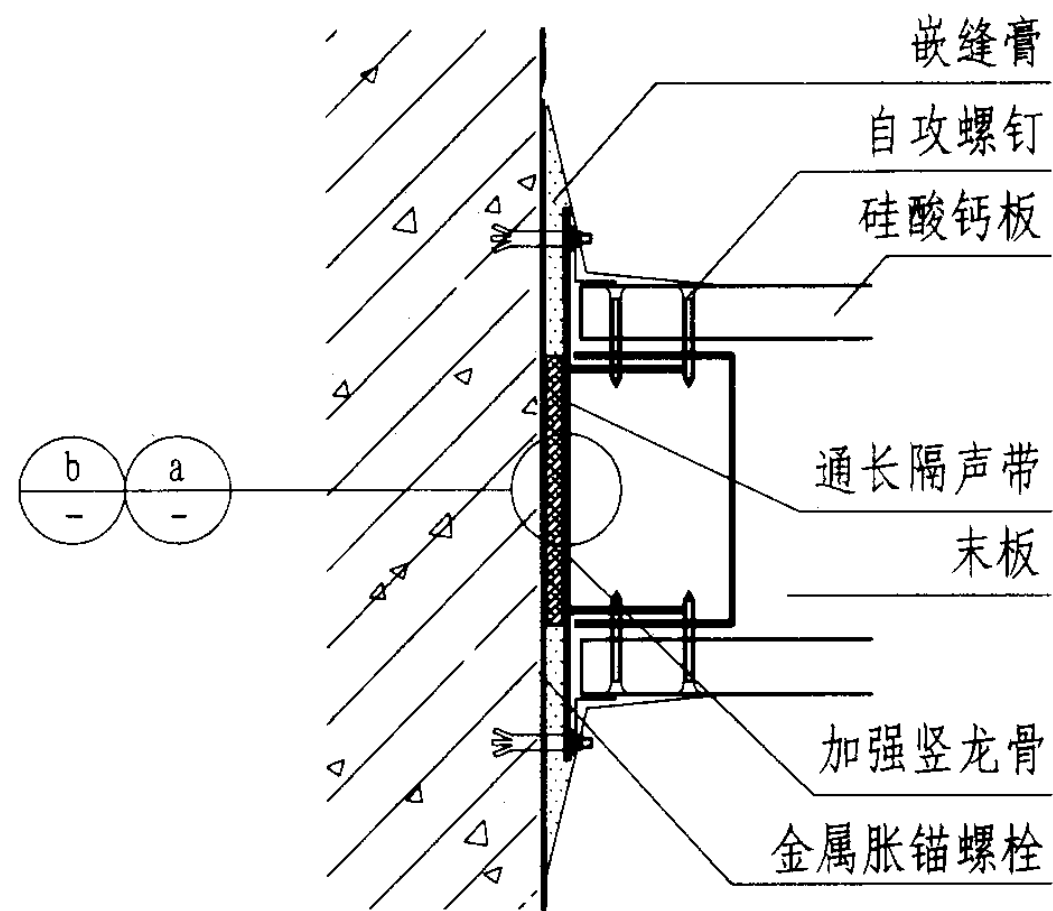

b 加强竖龙骨立面图

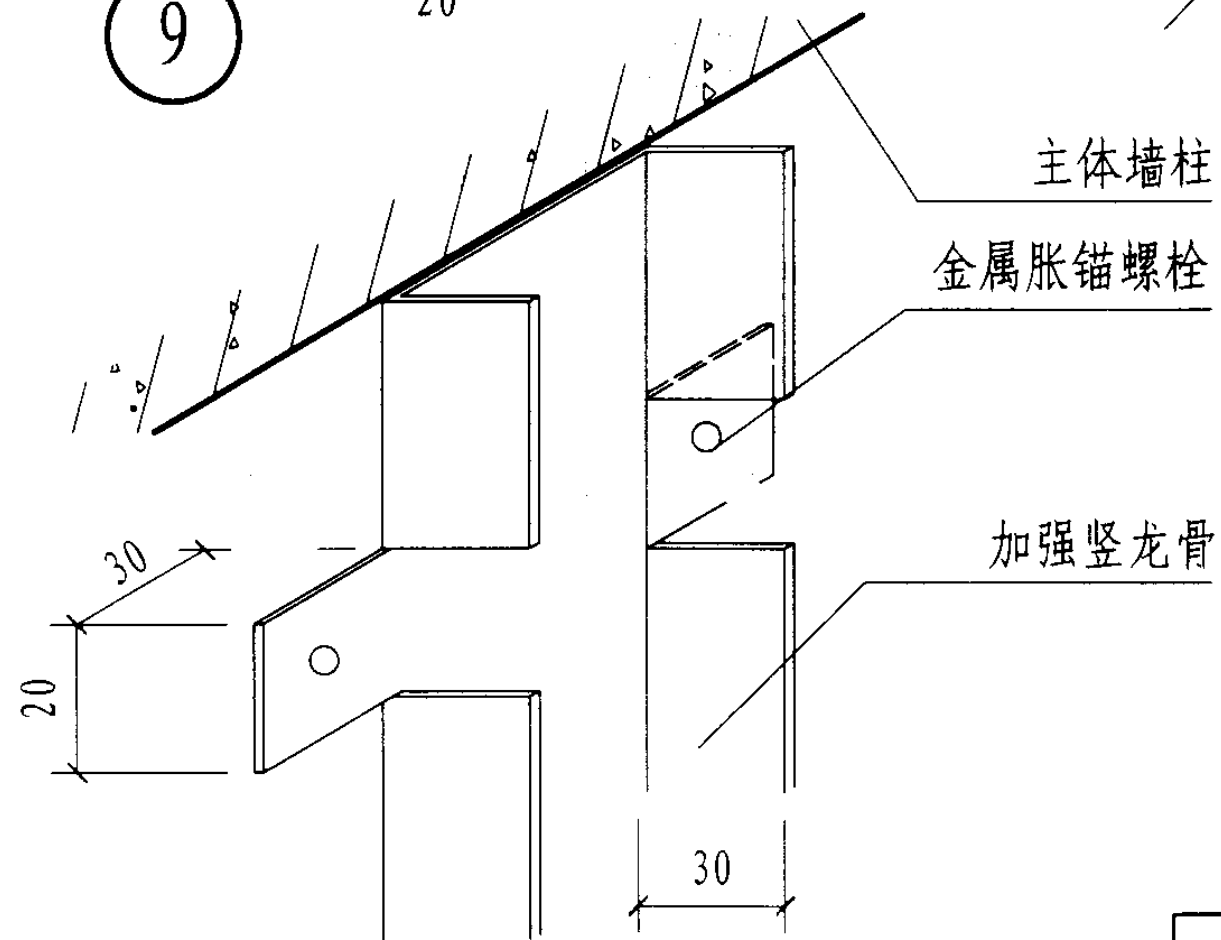


加强竖龙骨安装示意图

末板安装节点


图集号 03J111-2

审核 李长发 徐畅 徐畅 设计 熊火生


页 18

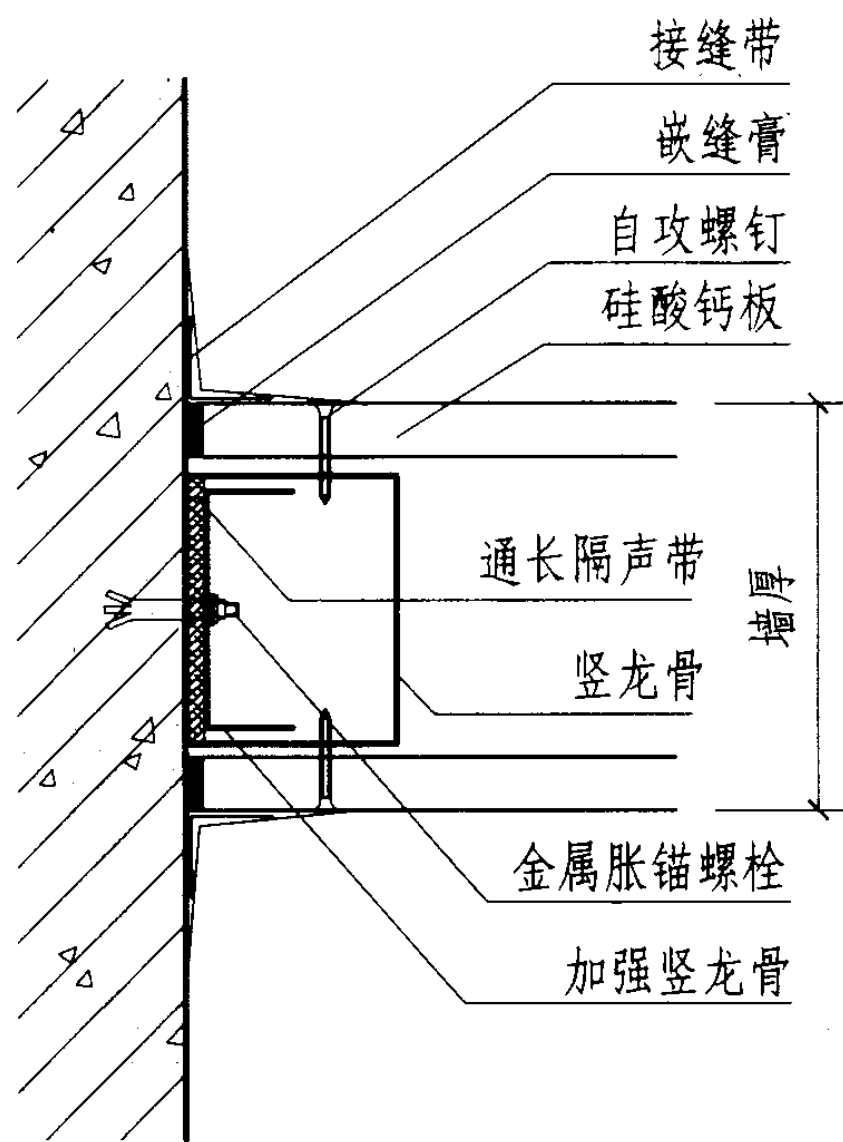

10 首板与主体墙柱连接

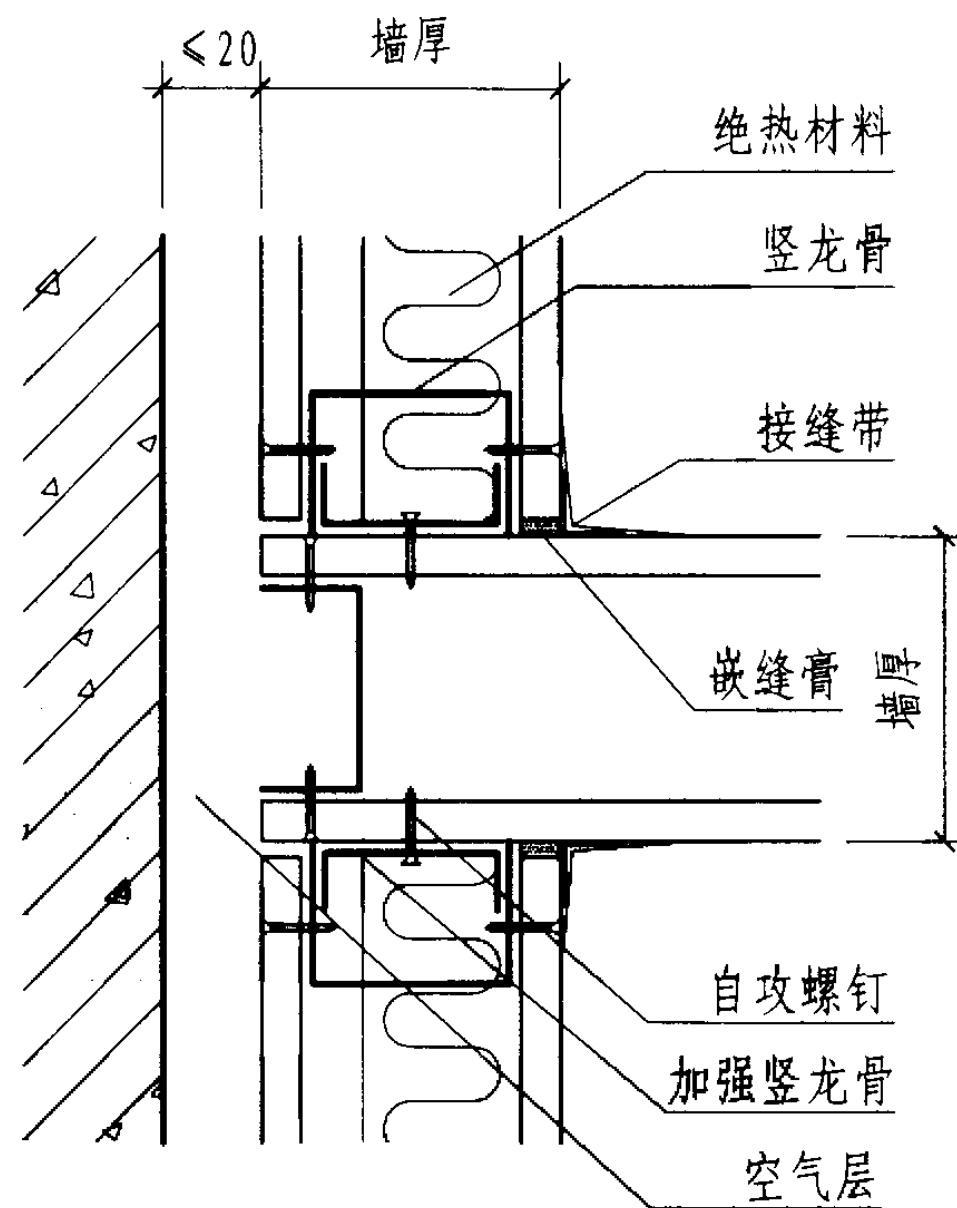

11 墙板与保温墙连接

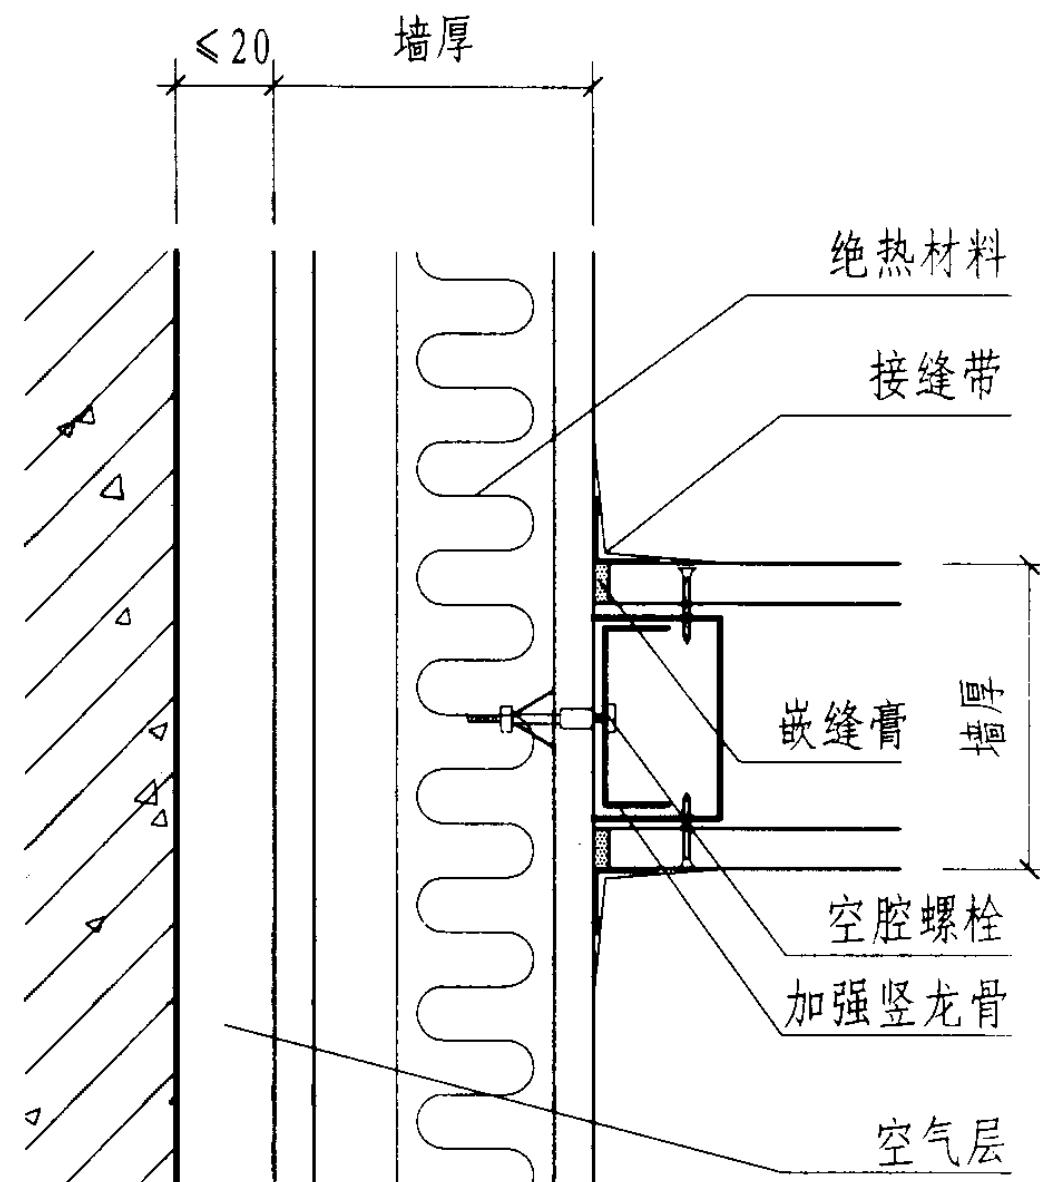


12 墙板与保温墙连接

墙板与主体墙、柱连接节点


图集号 03J111-2

审核 李长发 校对 徐畅 设计 熊火生

页 19

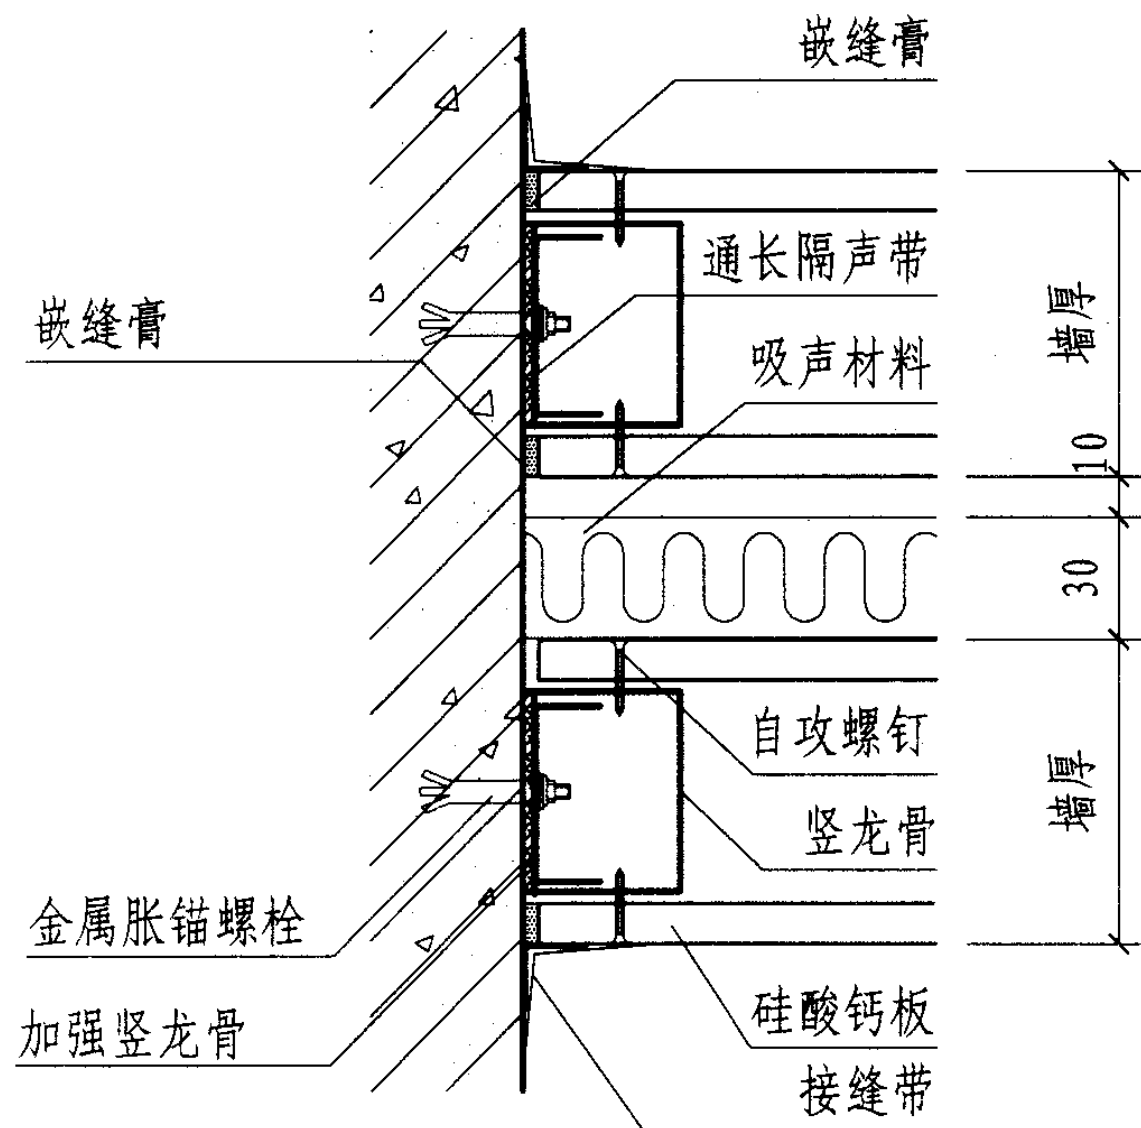

13

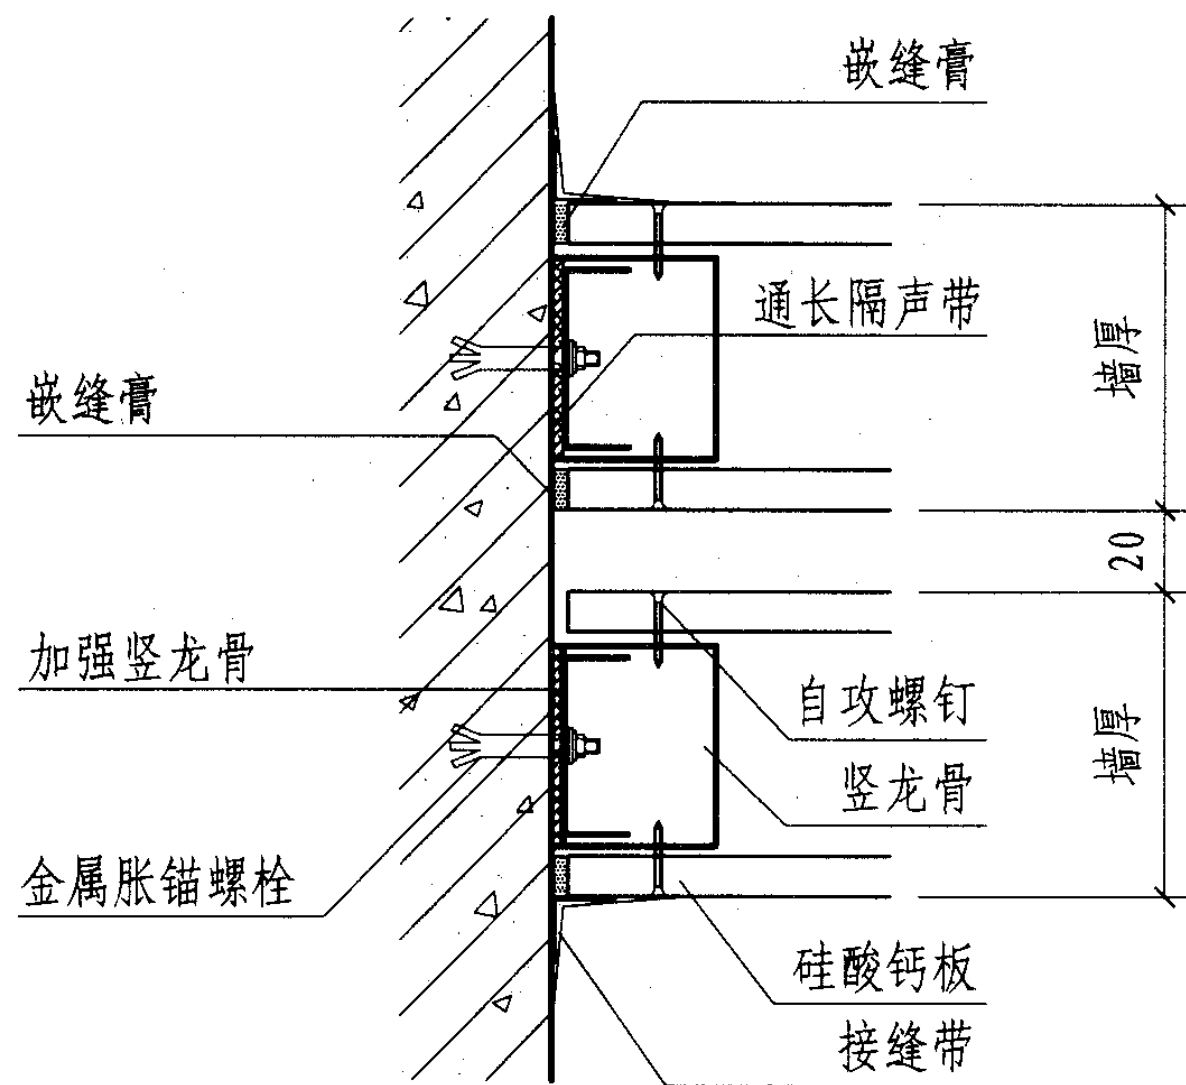

14

双层墙板与主体墙、柱连接节点

图集号

03J111-2

审核

李长发

校对


徐畅

设计


熊火生

页


20

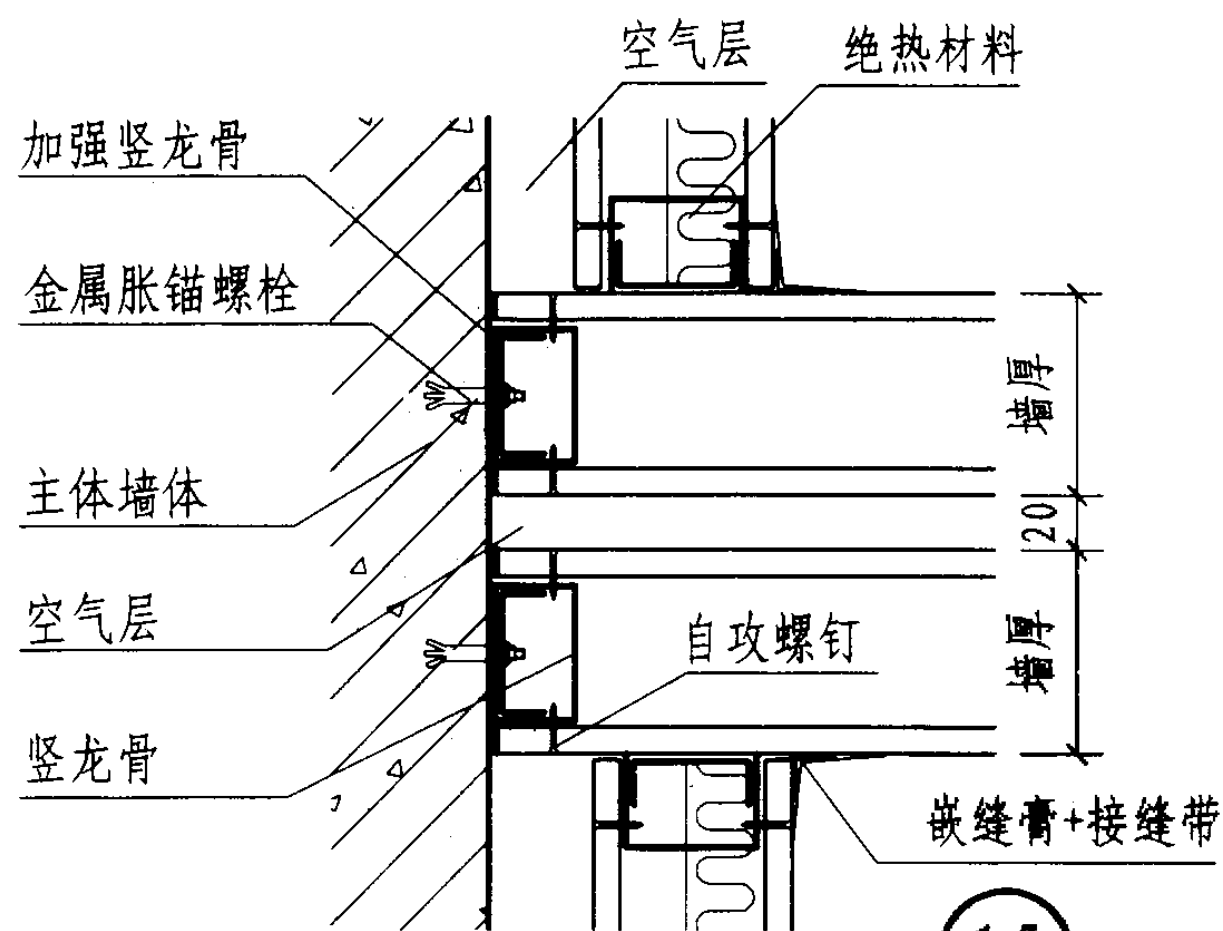


15

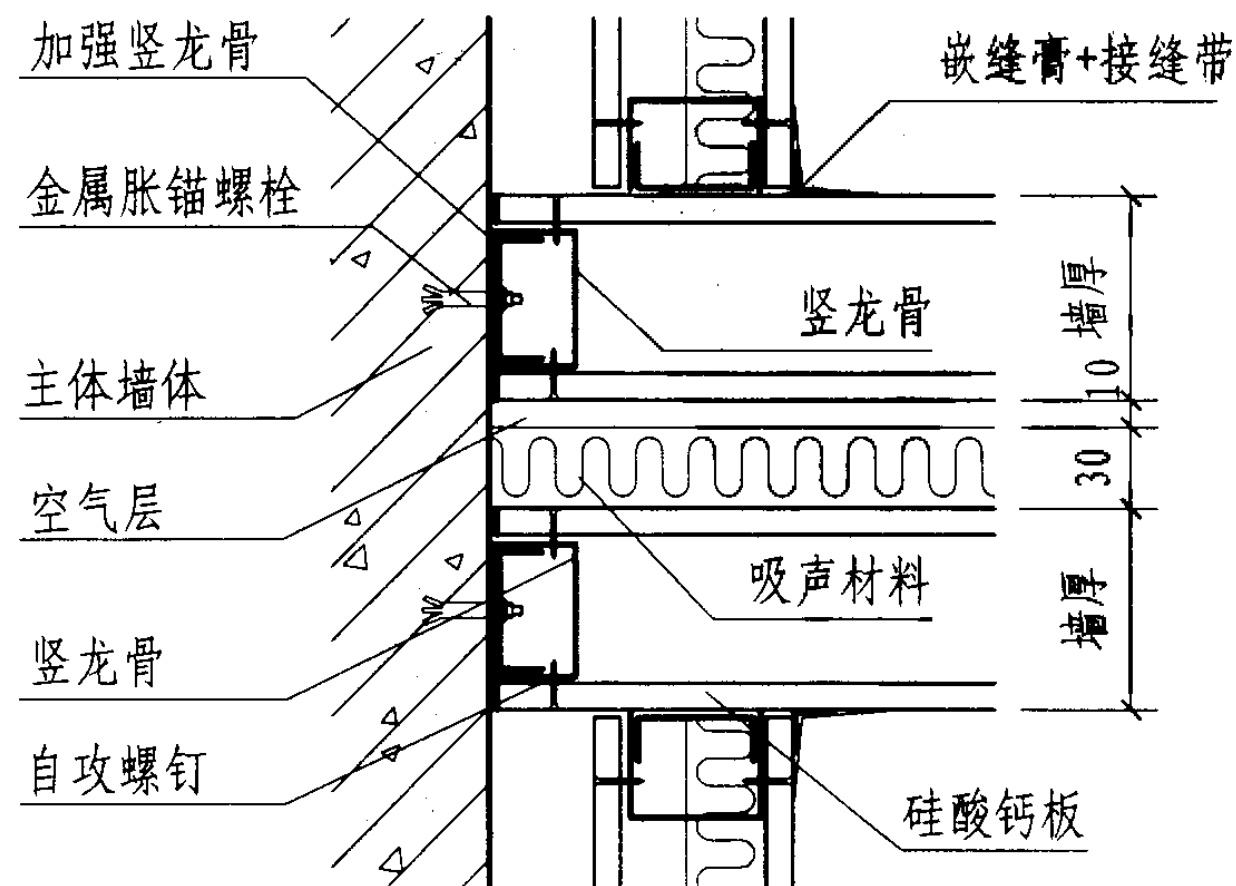

16

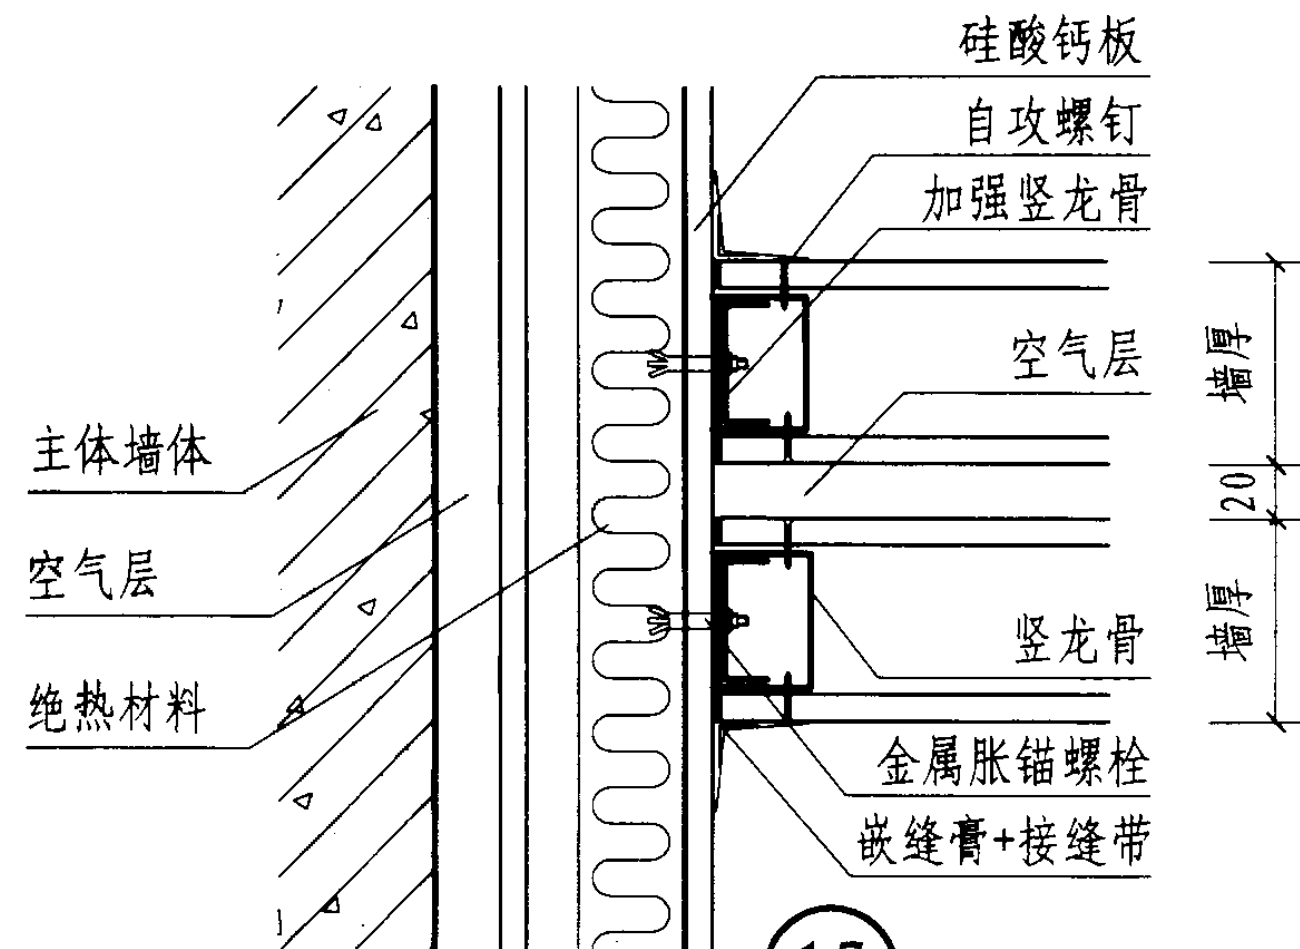

17

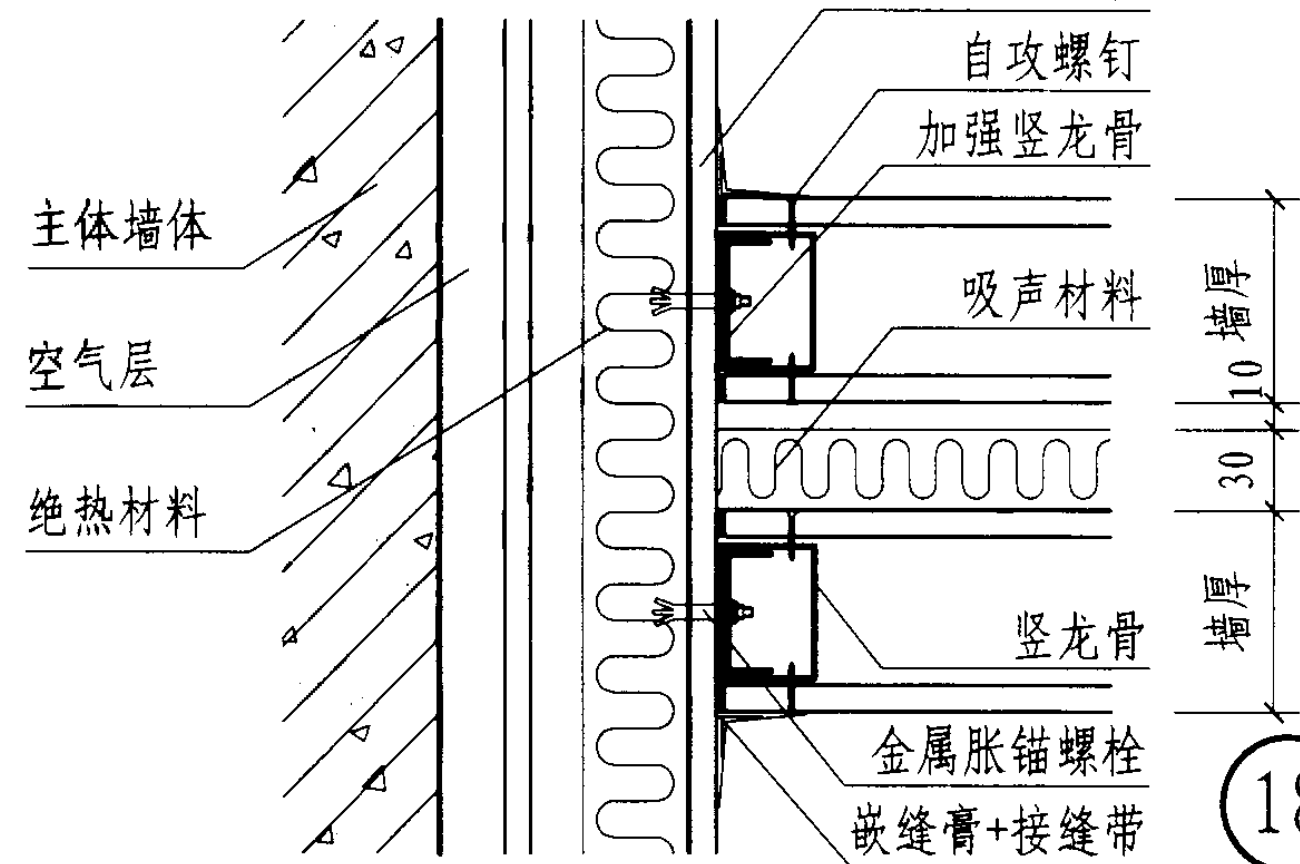

18

双层隔声、保温墙与主体墙体连接节点


图集号

03J111-2


审核 李长发 徐畅 设计 熊火生

页


21

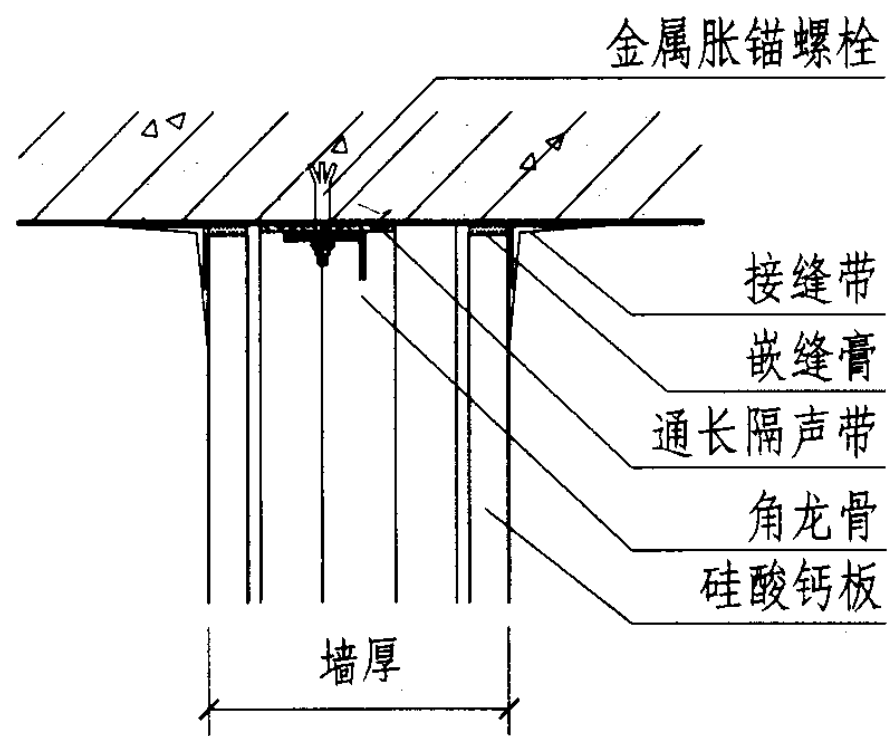


19 墙板与楼板顶面连接

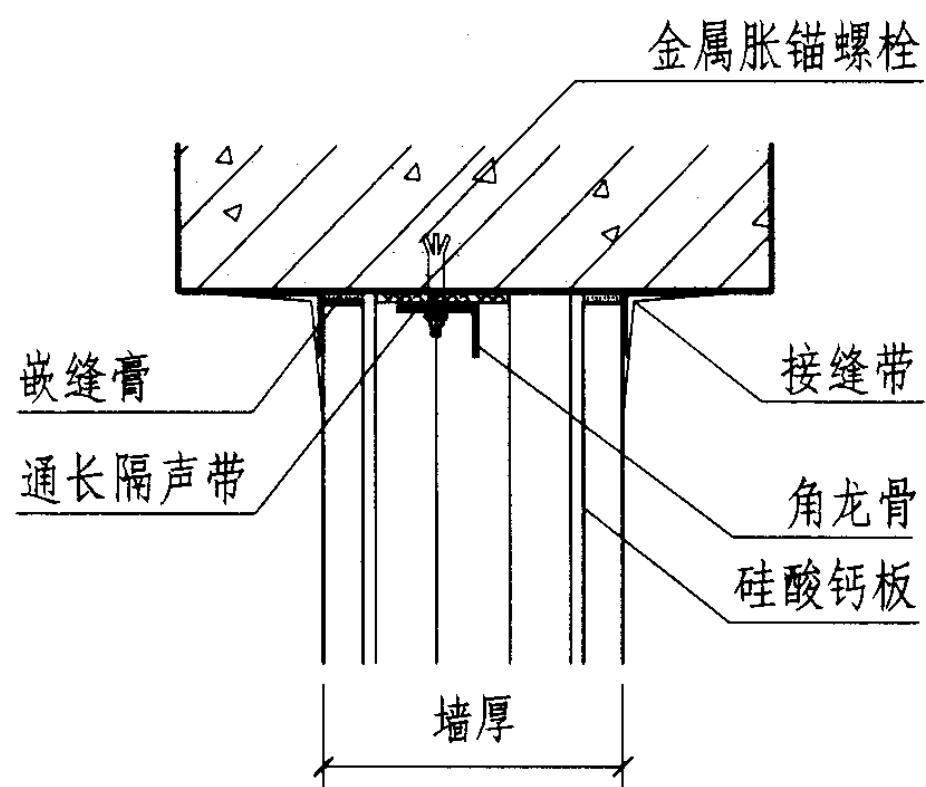


20 墙板与梁底连接

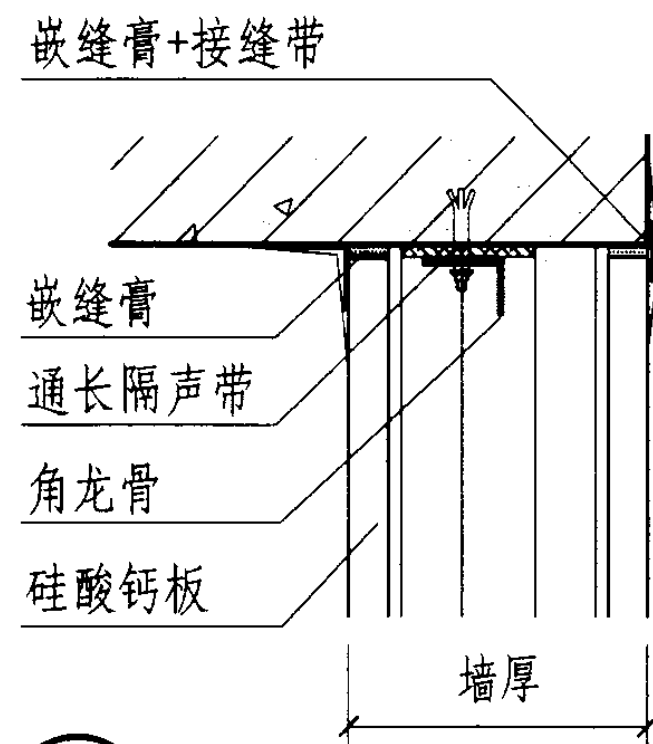

21 墙板与梁底一侧平齐连接




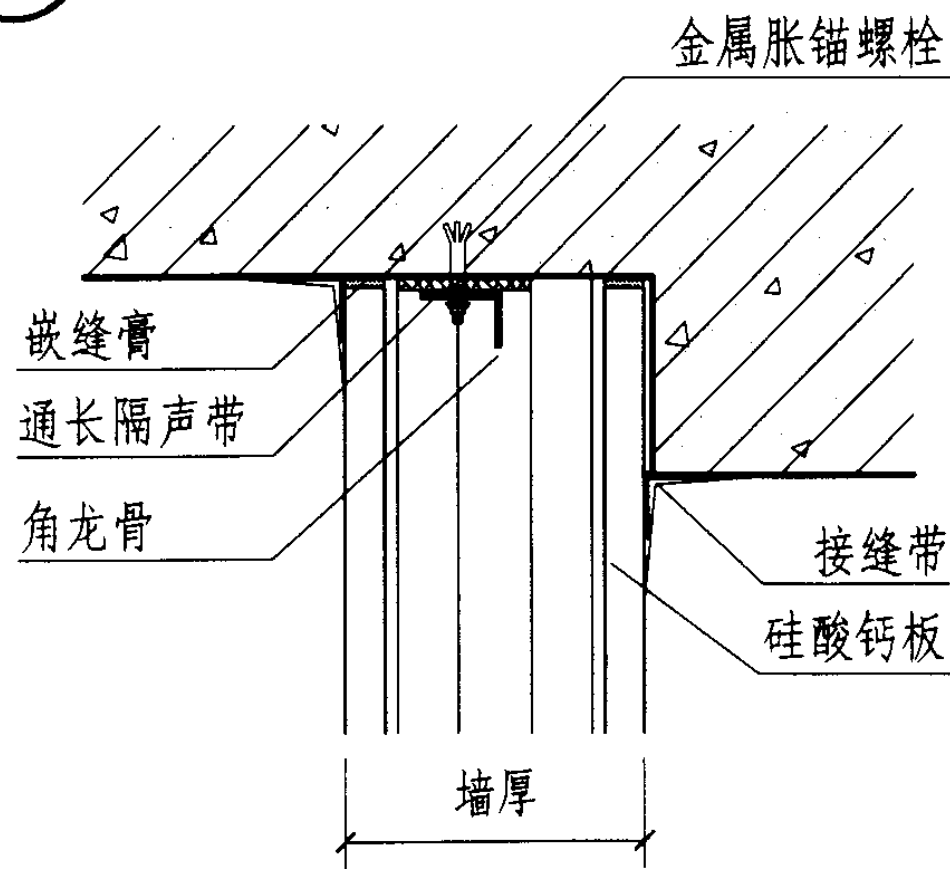


22 墙板沿梁与楼板顶面连接

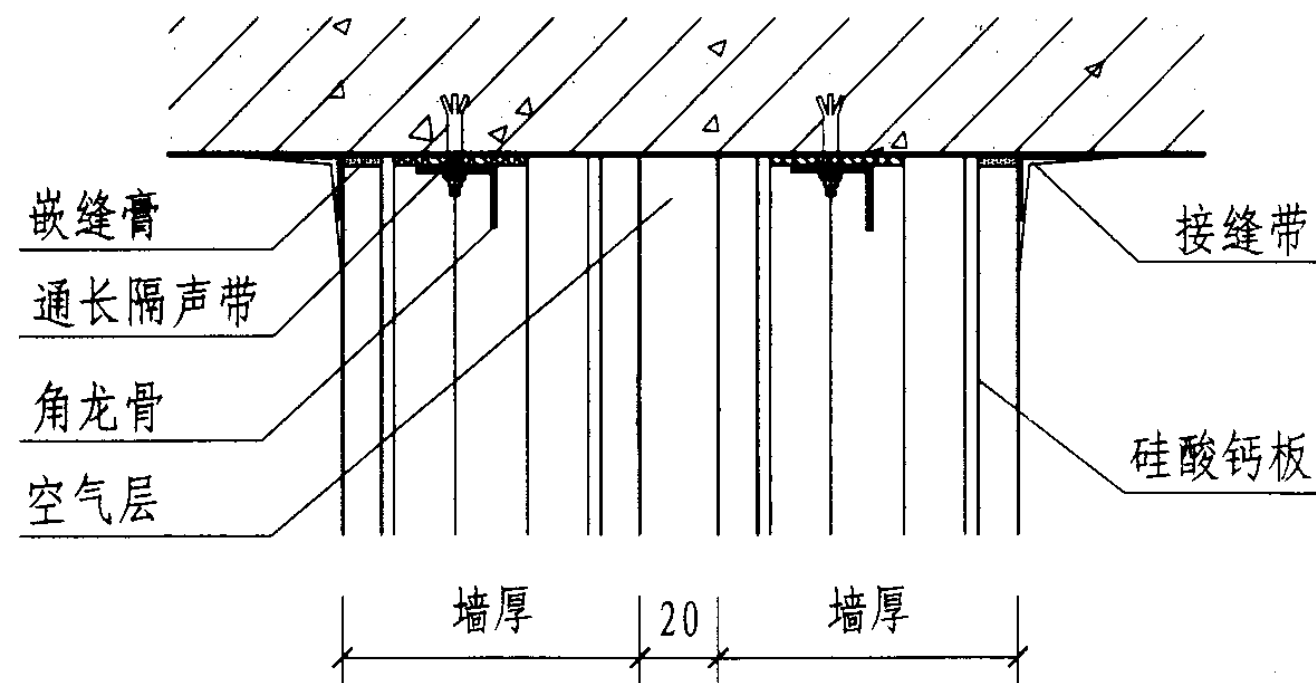


23 双层墙板与楼板顶面连接

墙板与结构梁、板连接节点 (一)								图集号	03J111-2
审核	李长发	徐畅	徐畅	设计	熊火生	页	22		

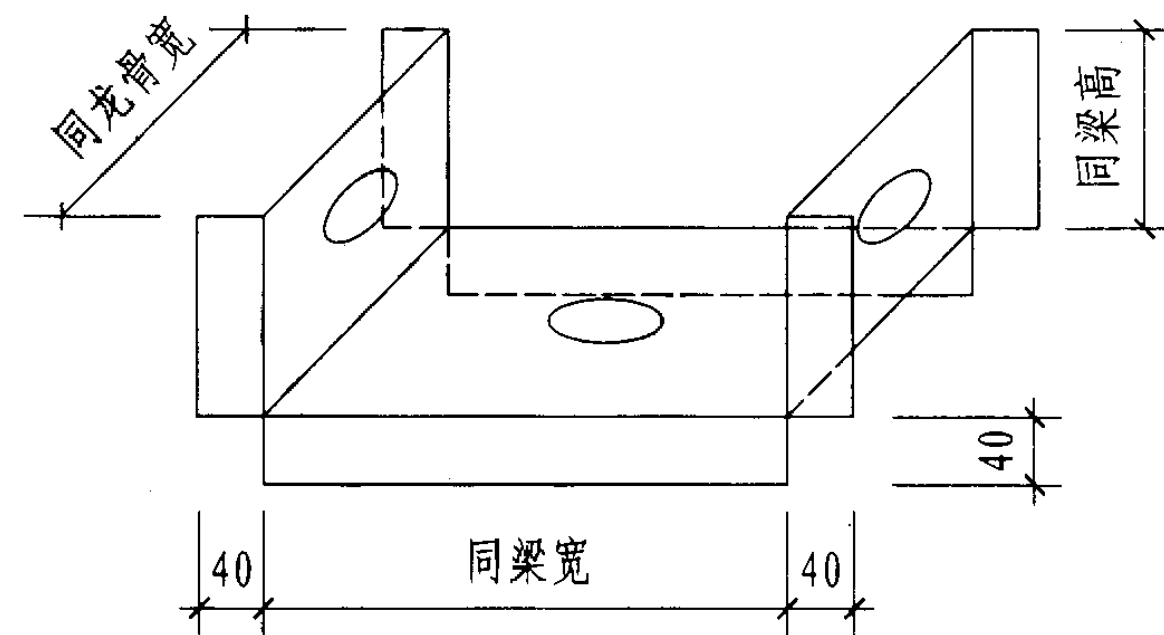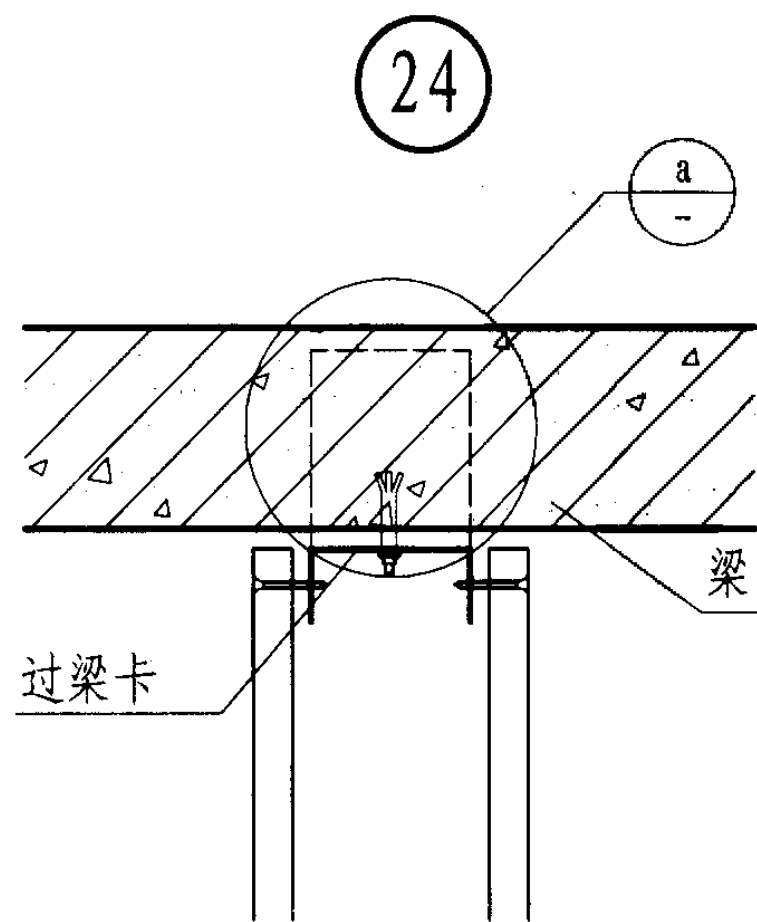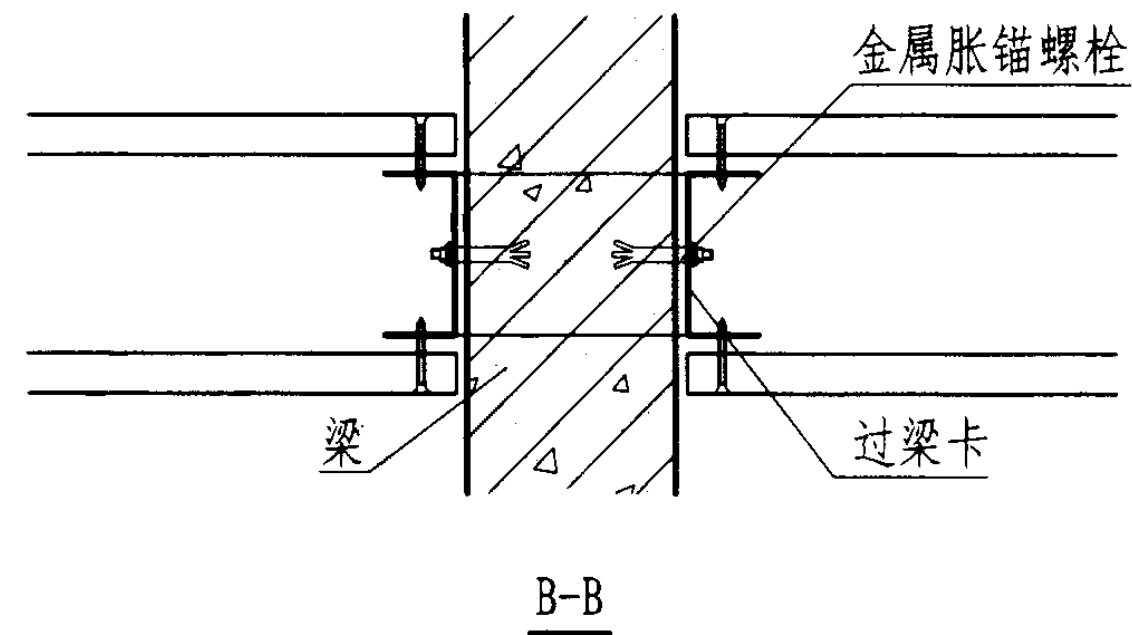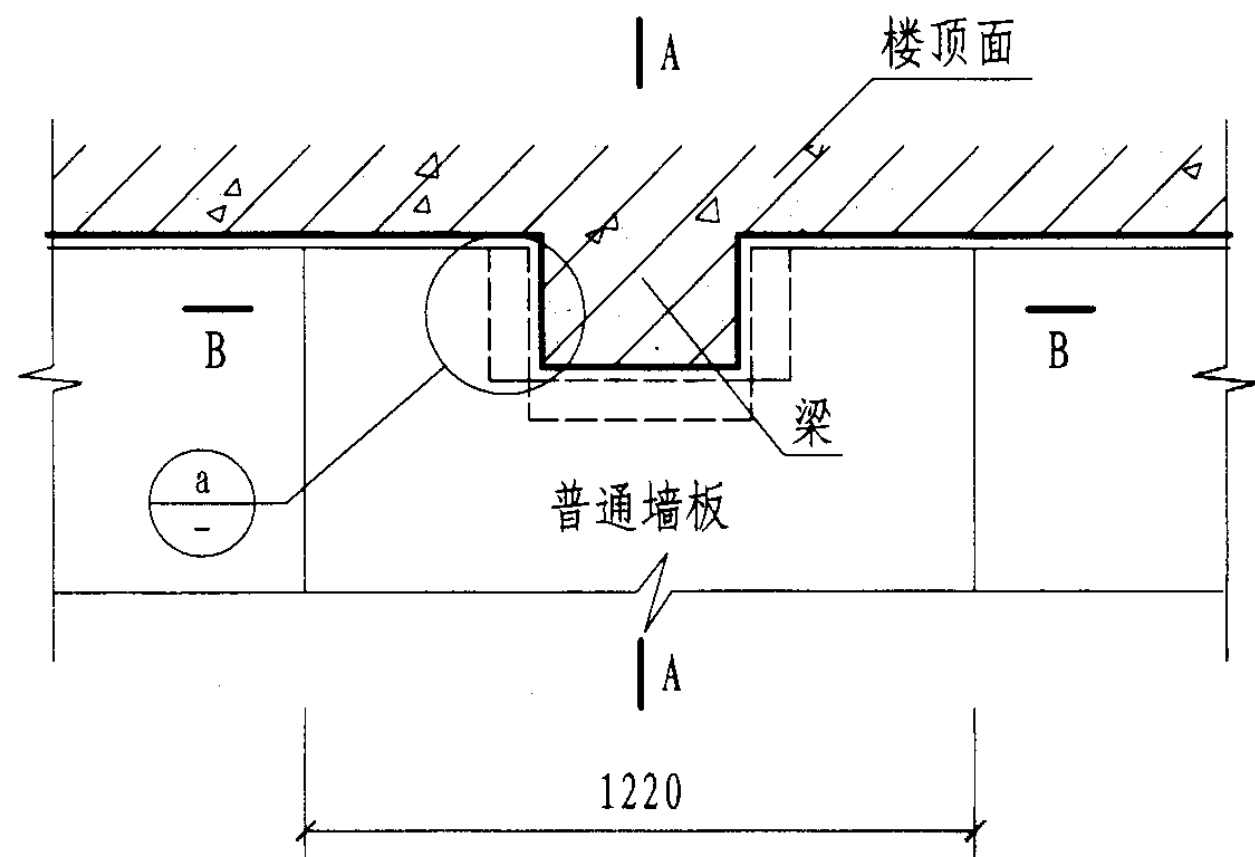


a 过梁卡 (镀锌钢板0.8厚)

墙板与结构梁、板连接节点 (二)								图集号	03J111-2
审核	李长发	校对	徐畅	徐畅	设计	熊火生	页	23	





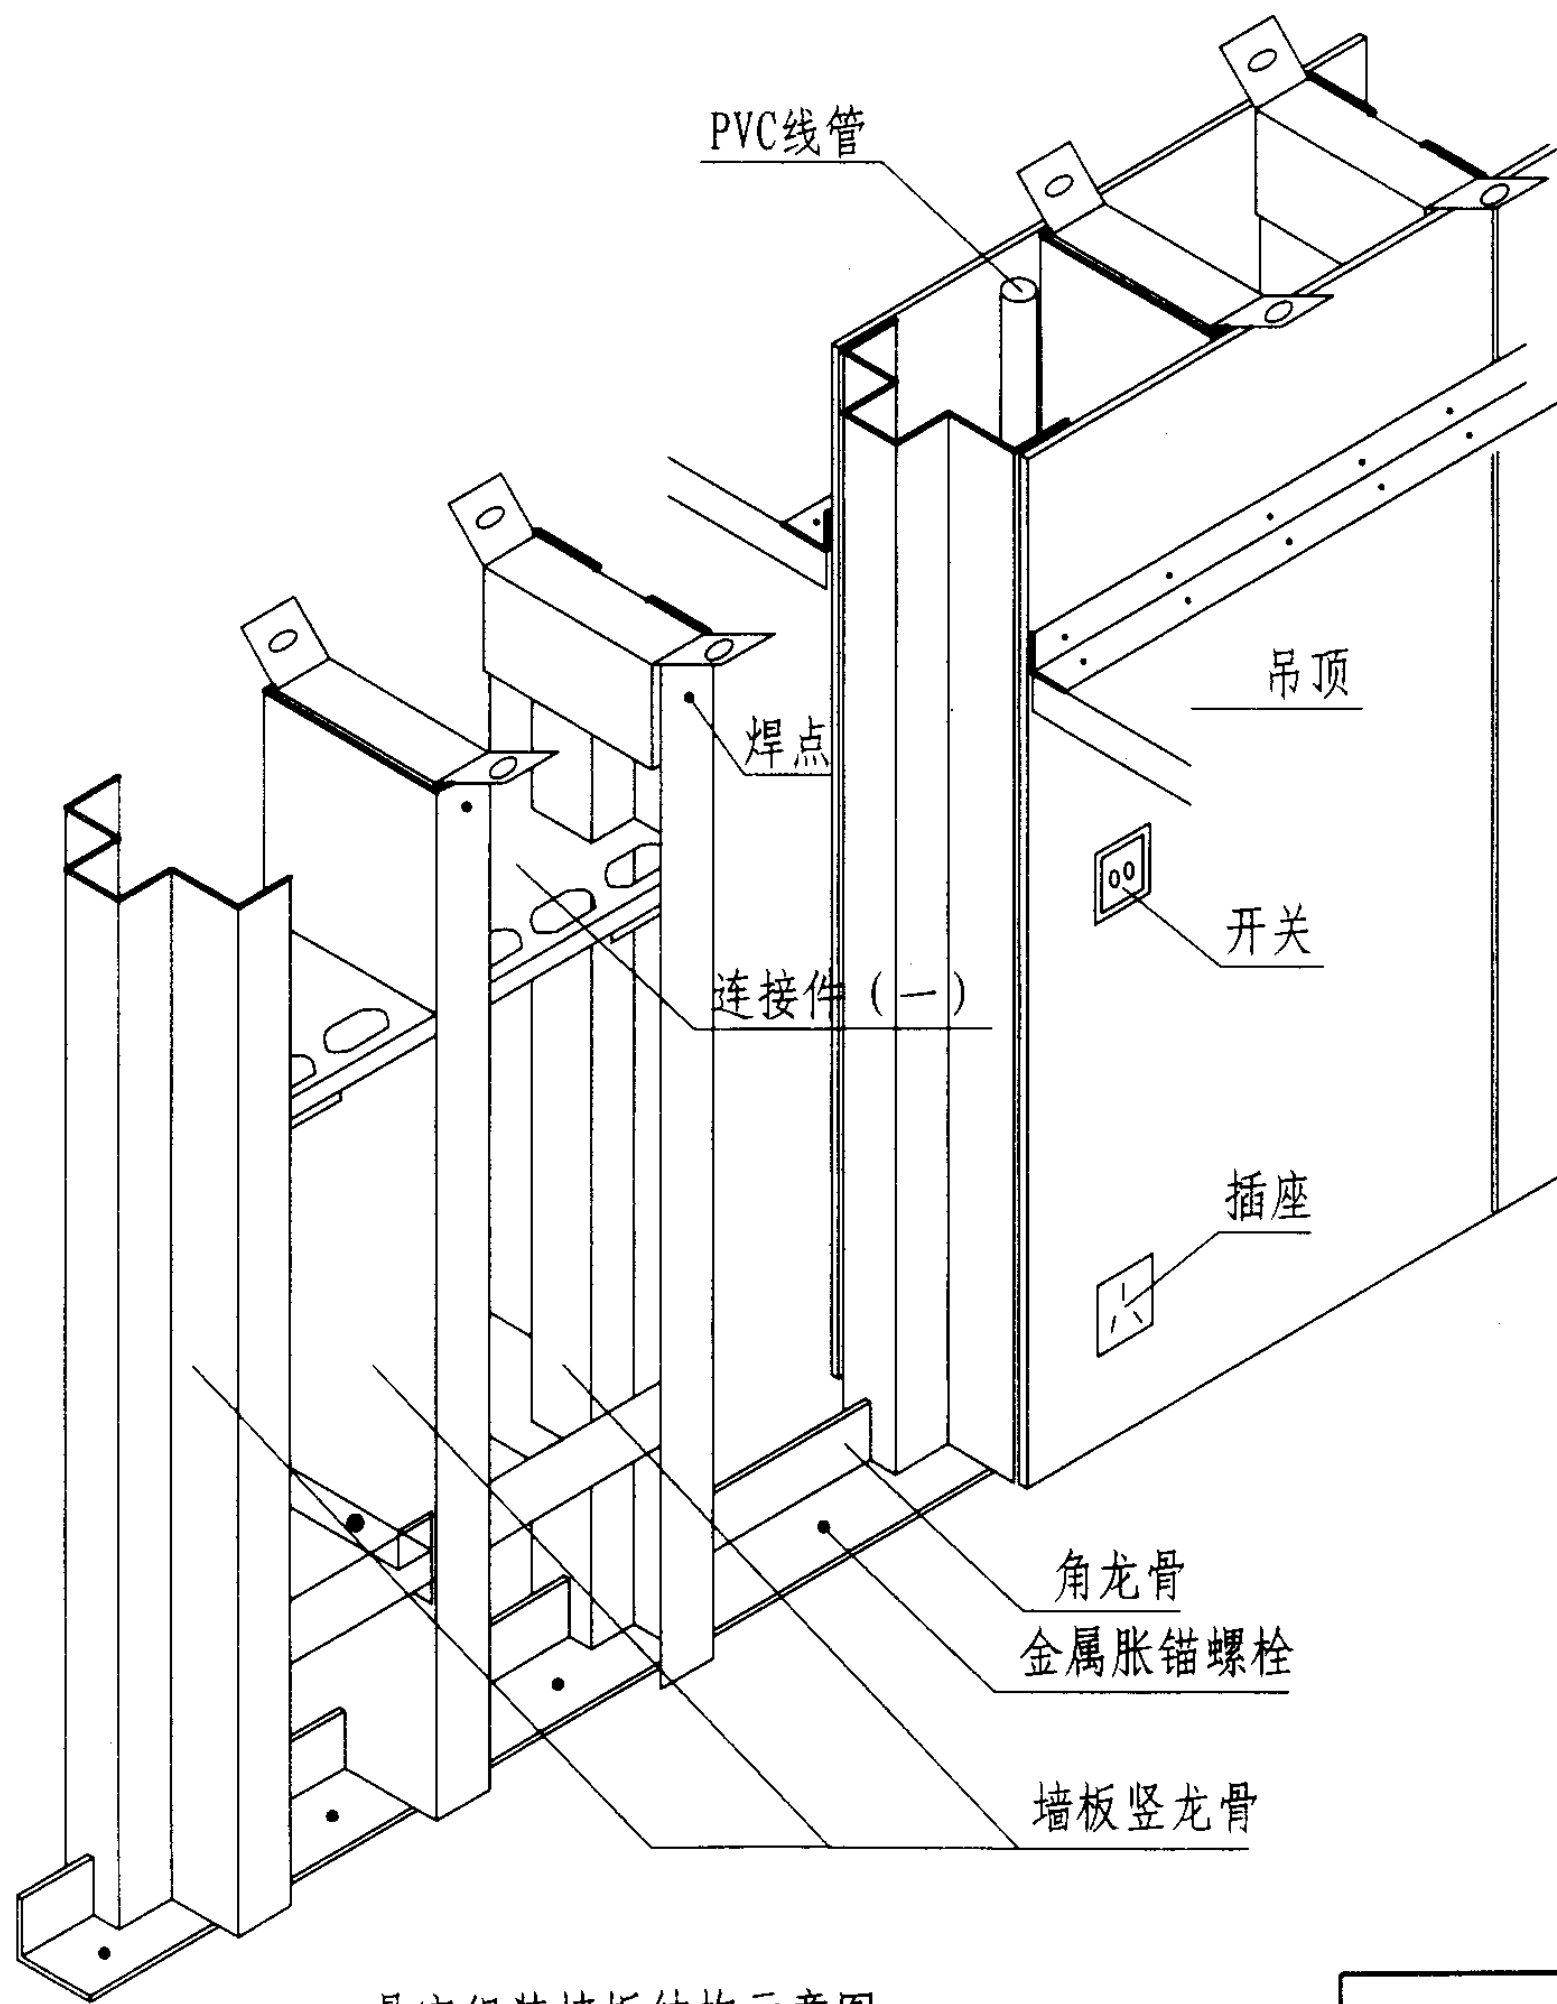


悬空组装墙板结构示意图

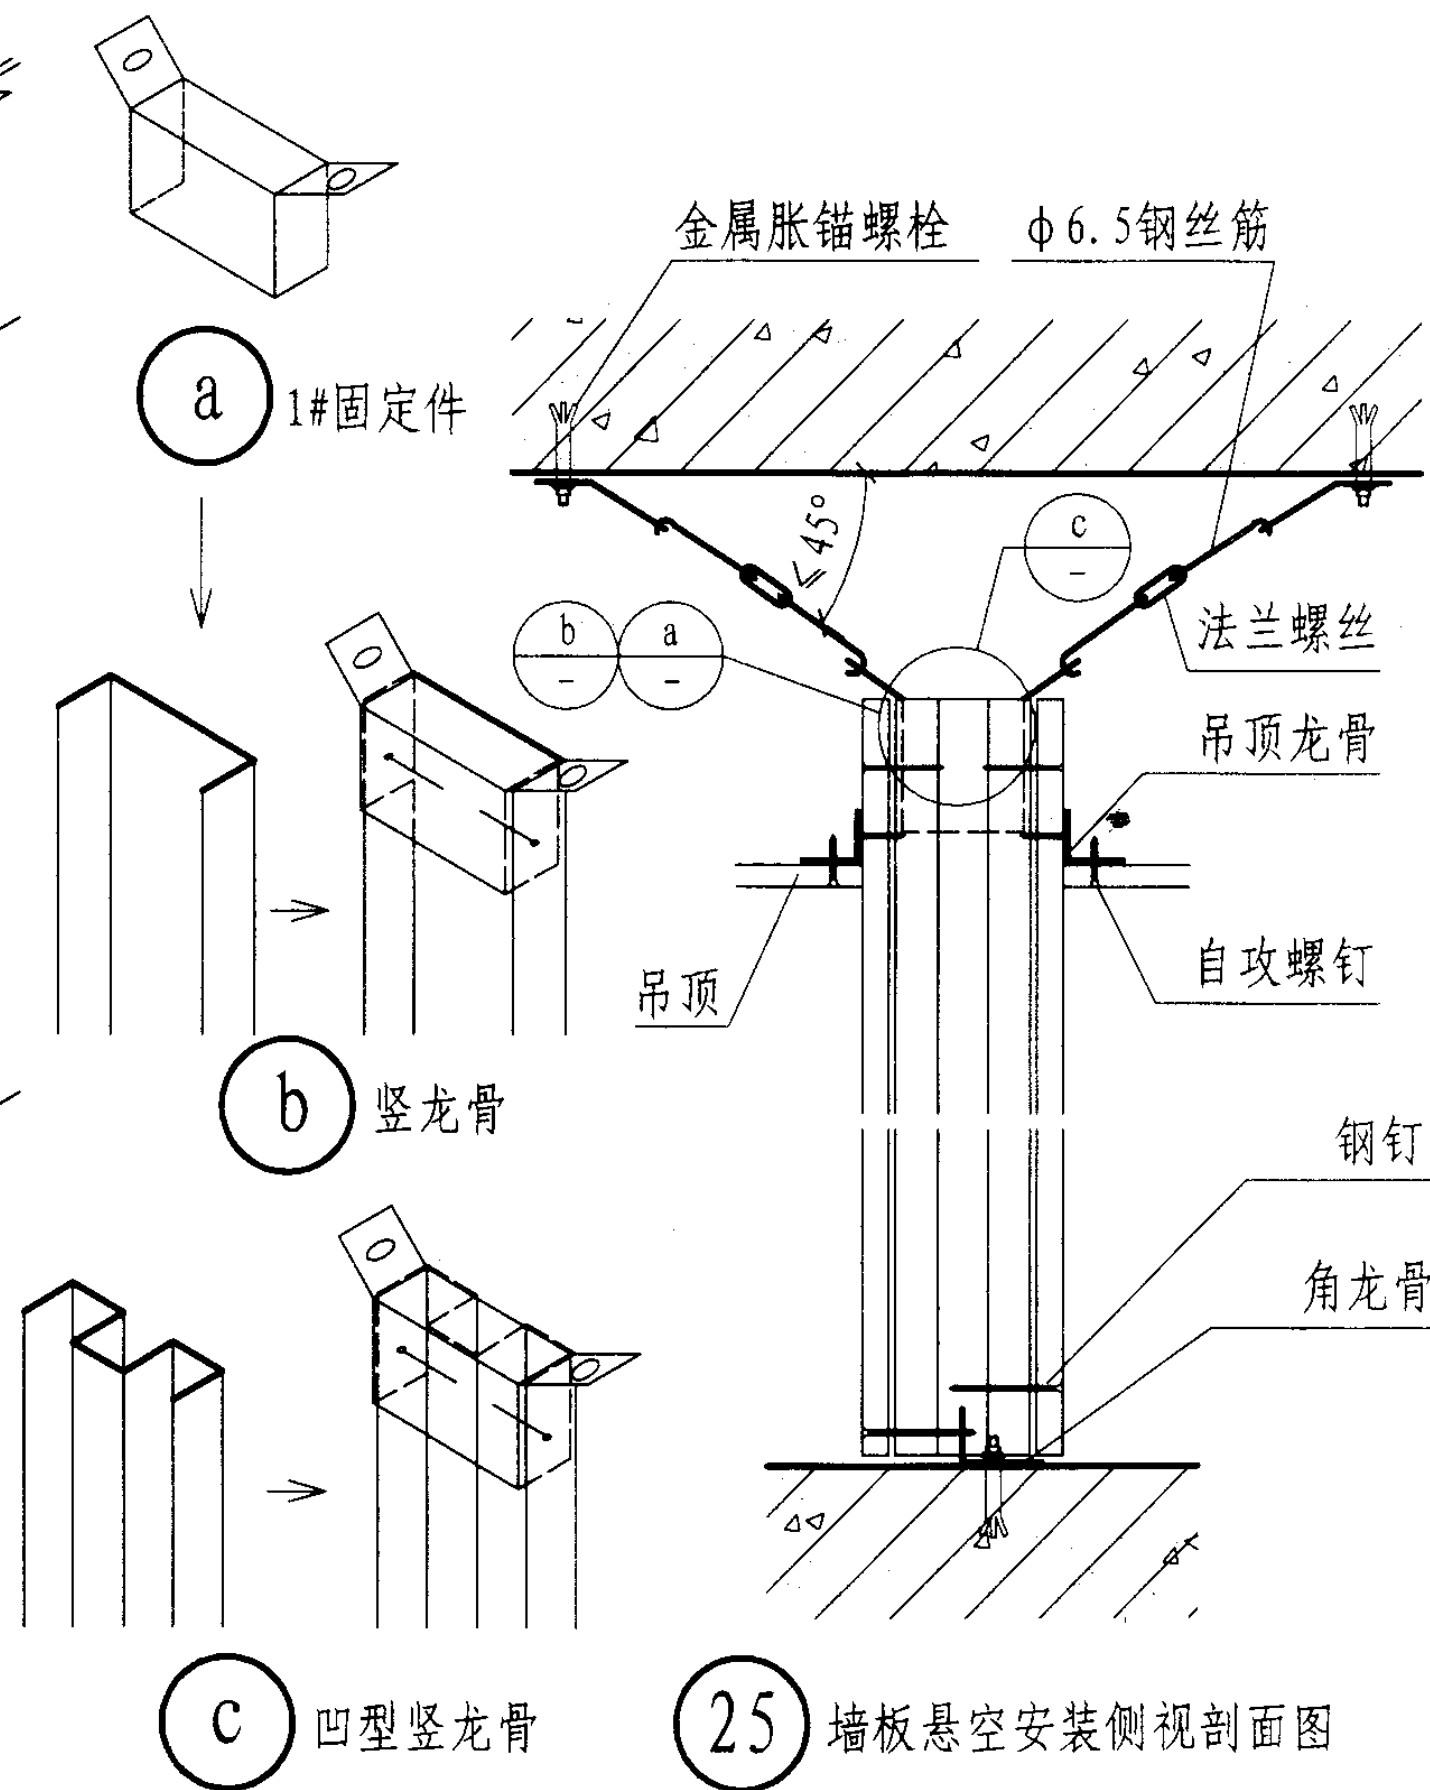

25 墙板悬空安装侧视剖面图

墙板悬空与结构梁板连接节点								图集号	03J111-2
审核	李长发	徐畅	徐畅	设计	熊火生	徐畅	徐畅	页	24

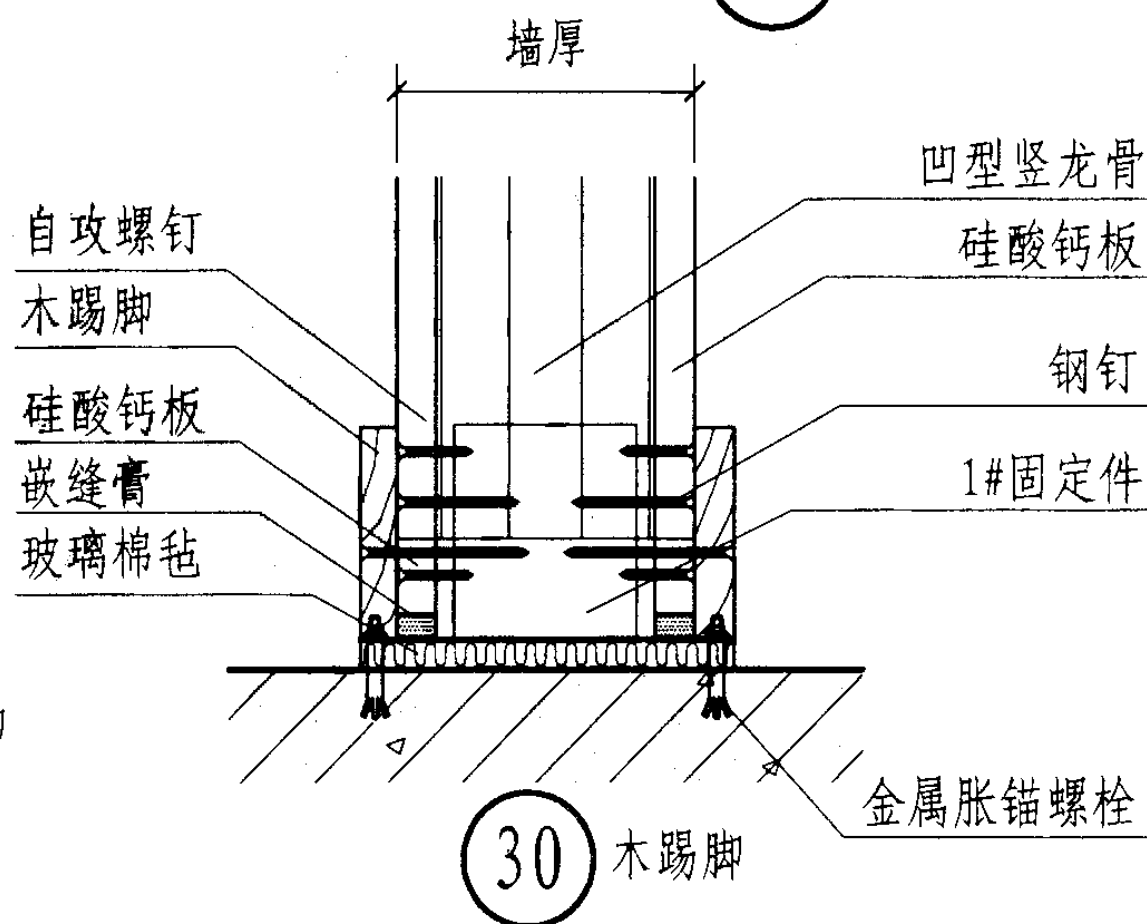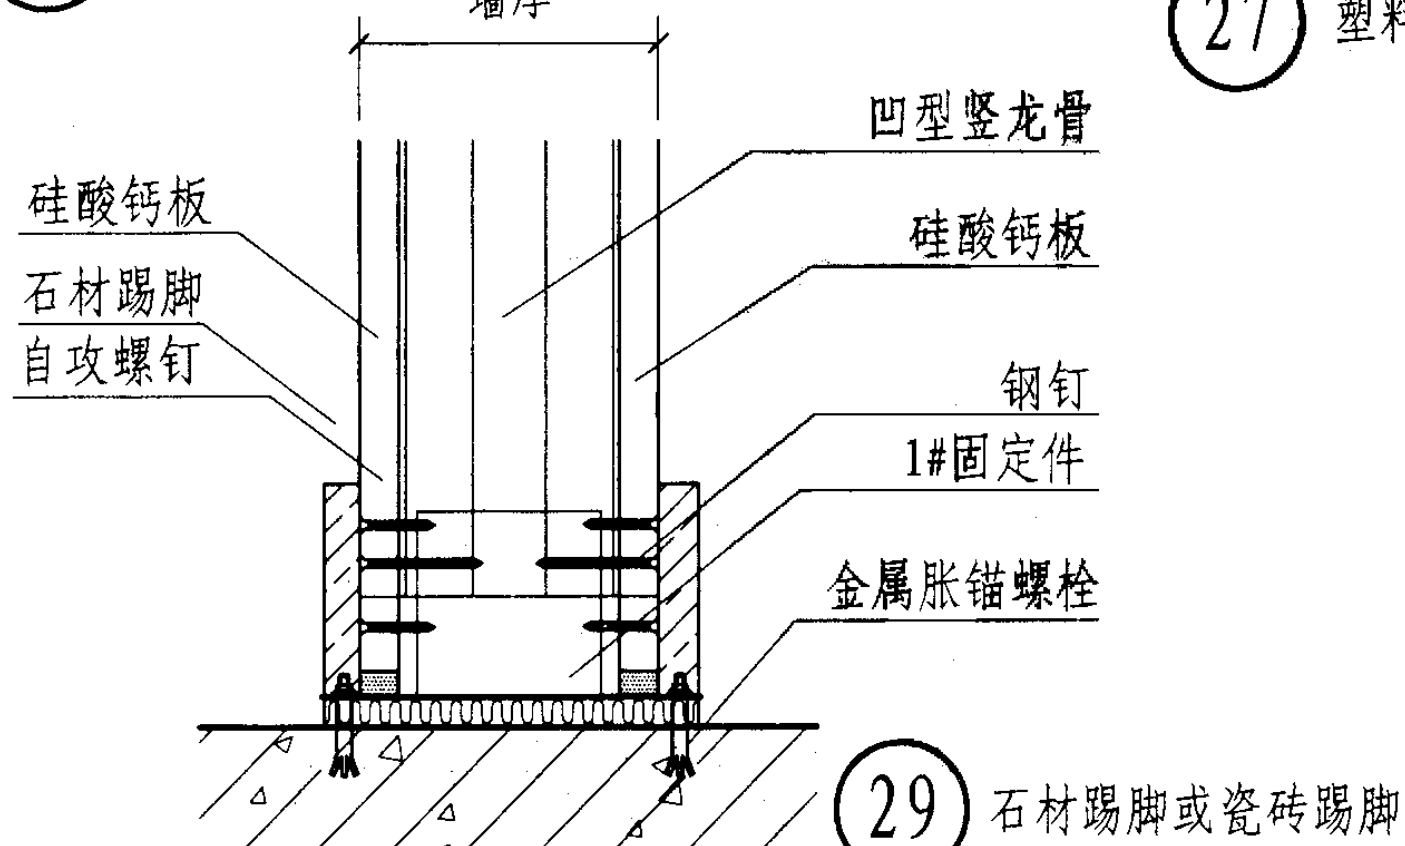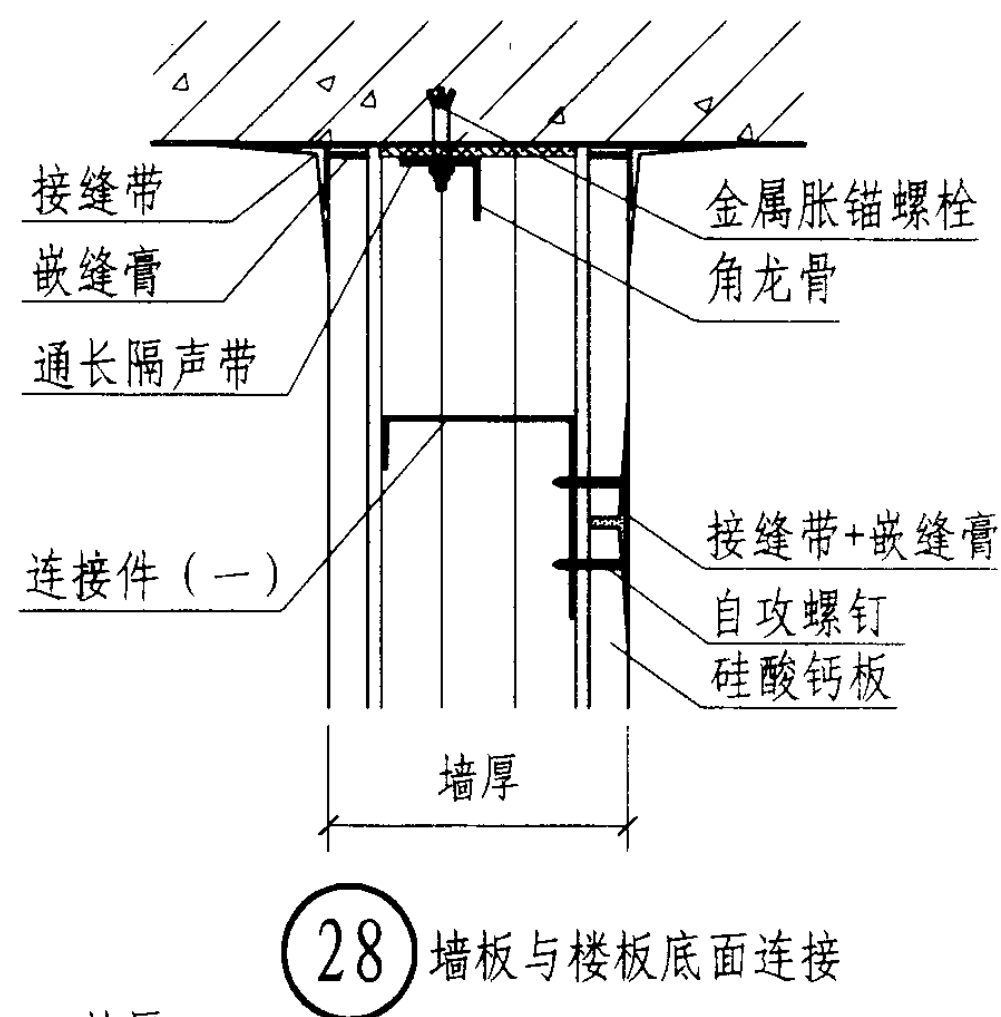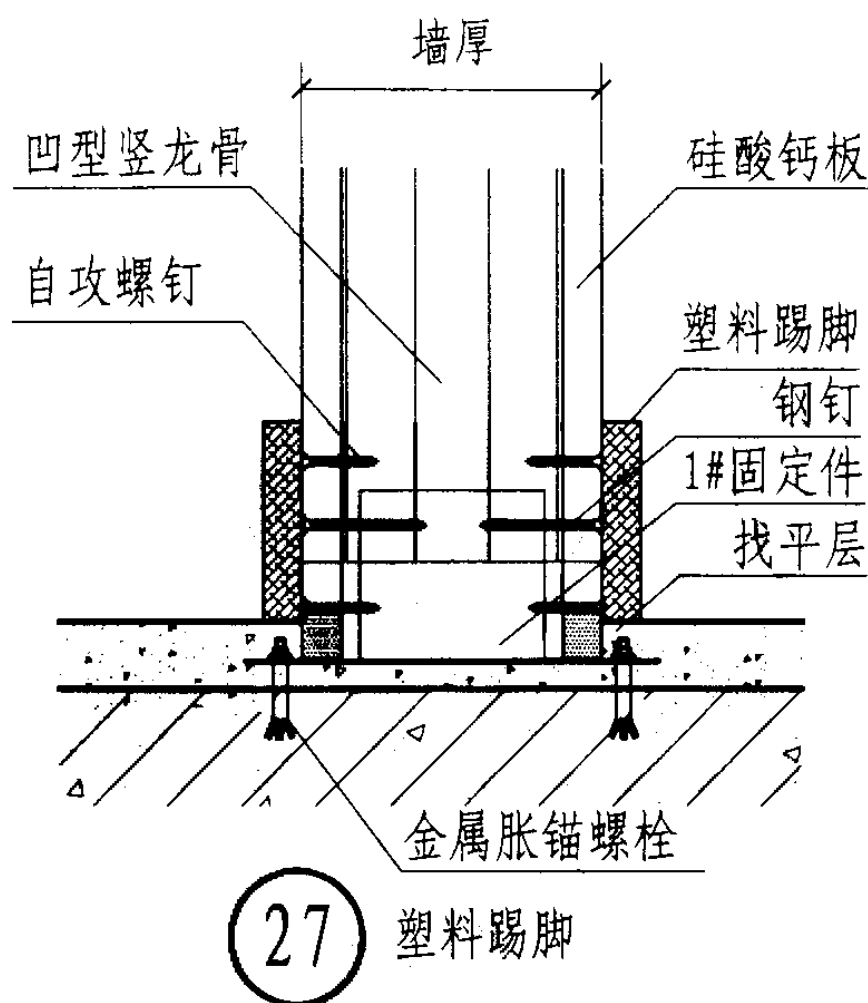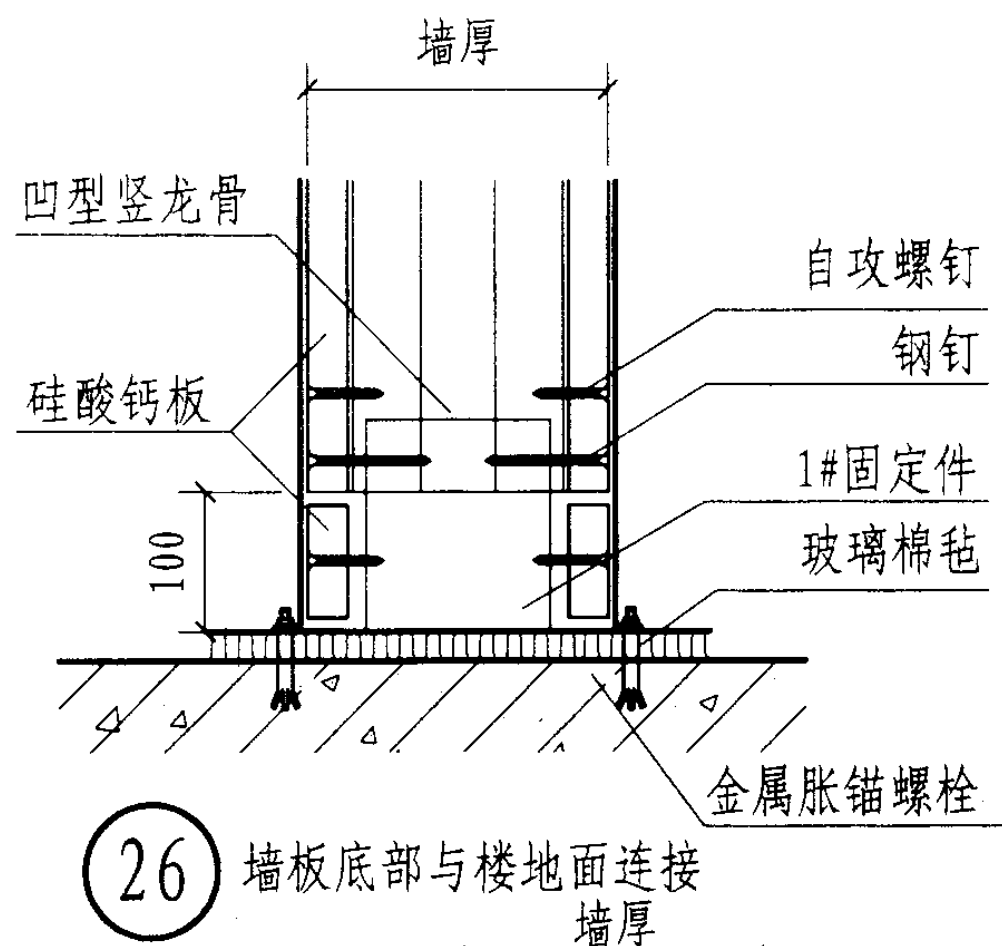

- 注:
1. 水泥、瓷砖踢脚建议在硅酸钙板上每200mm钻一孔, 然后用水泥浆粘贴。
 2. 木踢脚可用胶粘剂或装饰用射钉固定。
 3. 有隔声要求时, 固定件与地面加设玻璃棉毡。
 4. 墙内埋设管线时, 使用2#固定件替代1#固定件。

墙板与楼地面连接、踢脚做法节点 (一)

审核 李长发

校对 徐畅


设计 熊火生

图集号


03J111-2

页


25

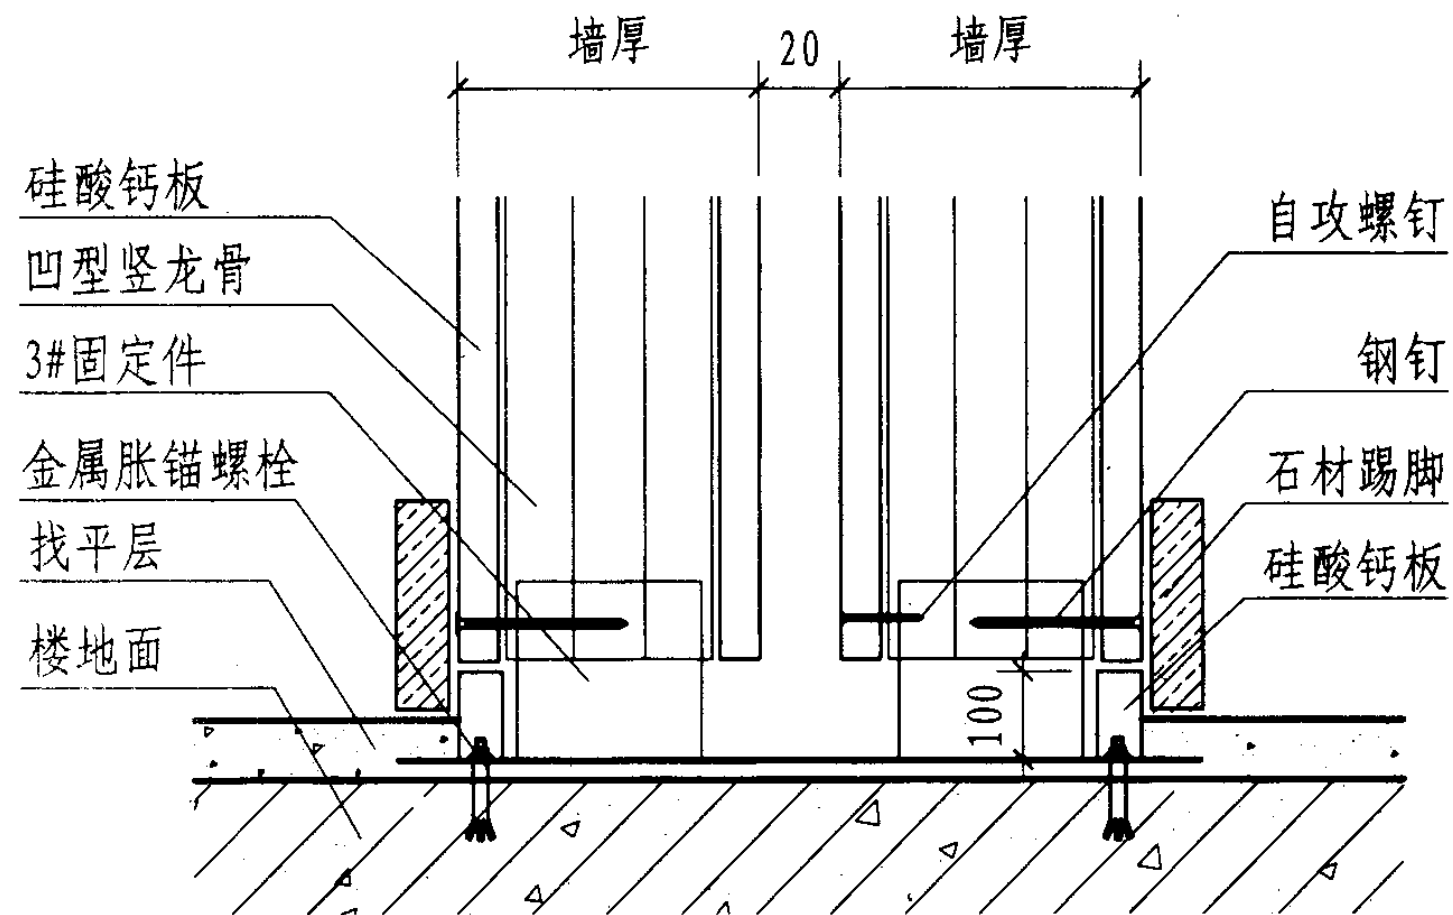

31 石材踢脚

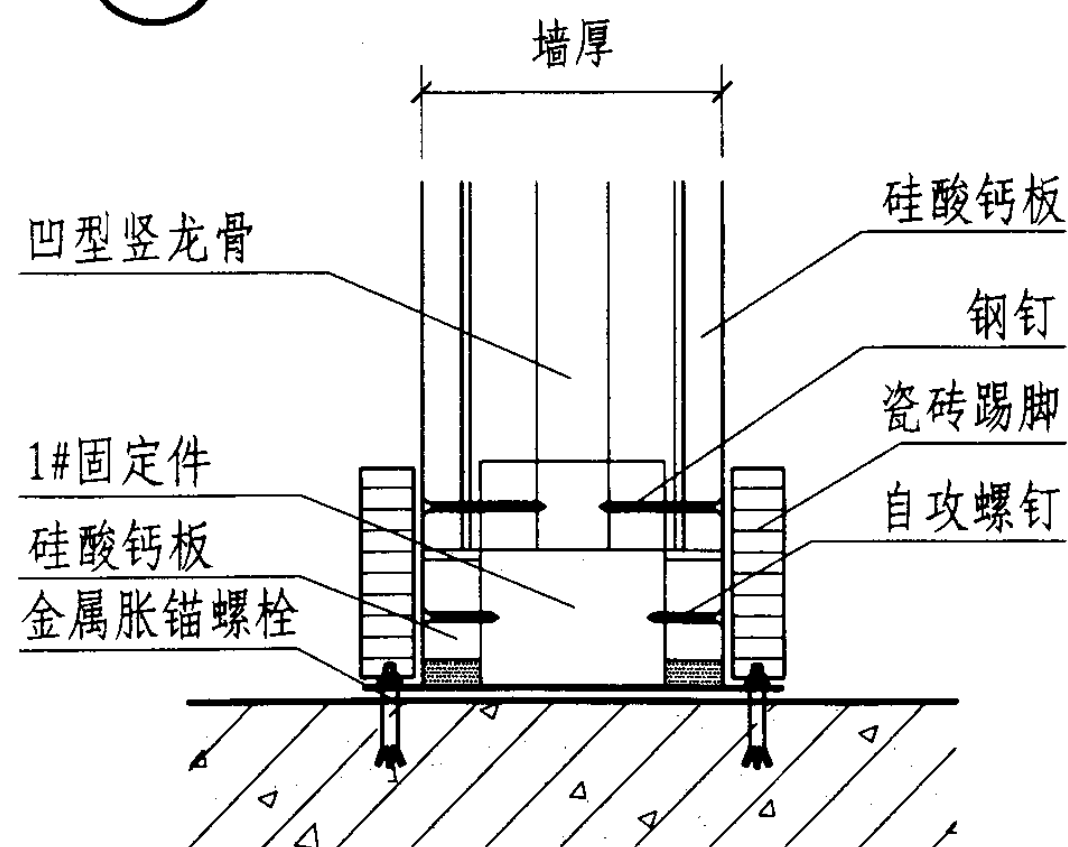

32 水泥踢脚或瓷砖踢脚

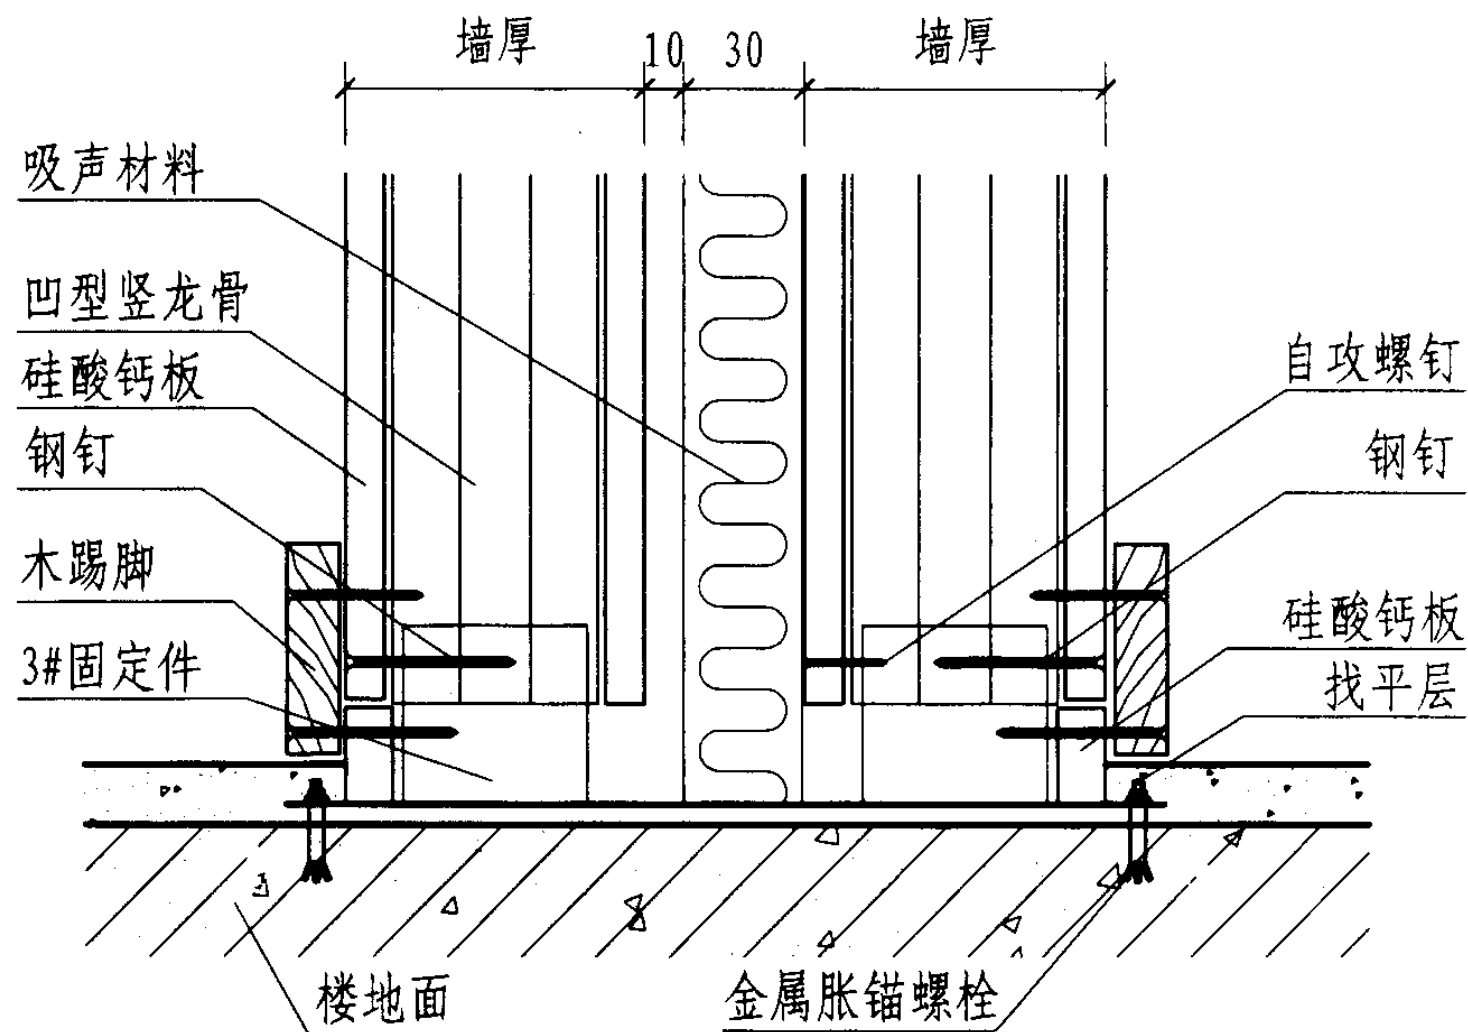


33 木踢脚

墙板与楼地面连接、踢脚做法节点 (二)


图集号 03J111-2

审核 李长发 徐畅 设计 熊火生


页 26

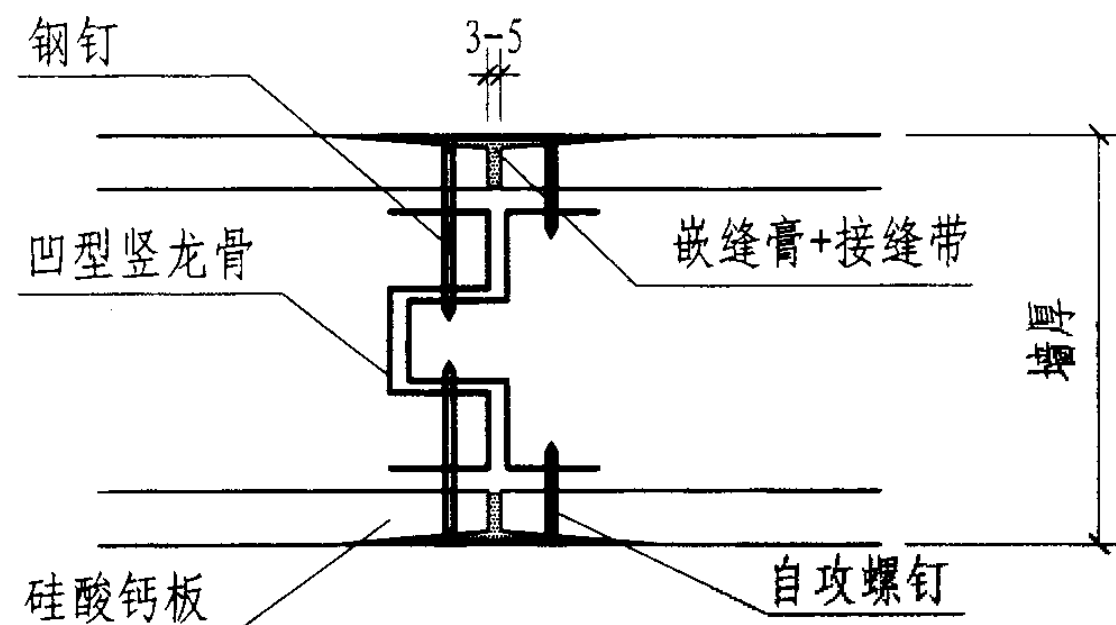


34 一字形墙板连接

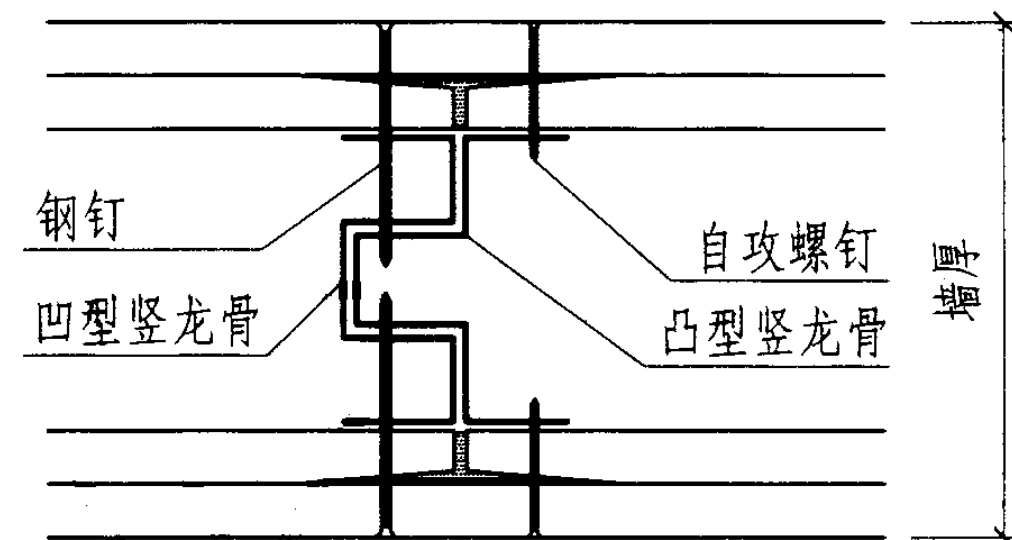

35 双层硅酸钙板接缝

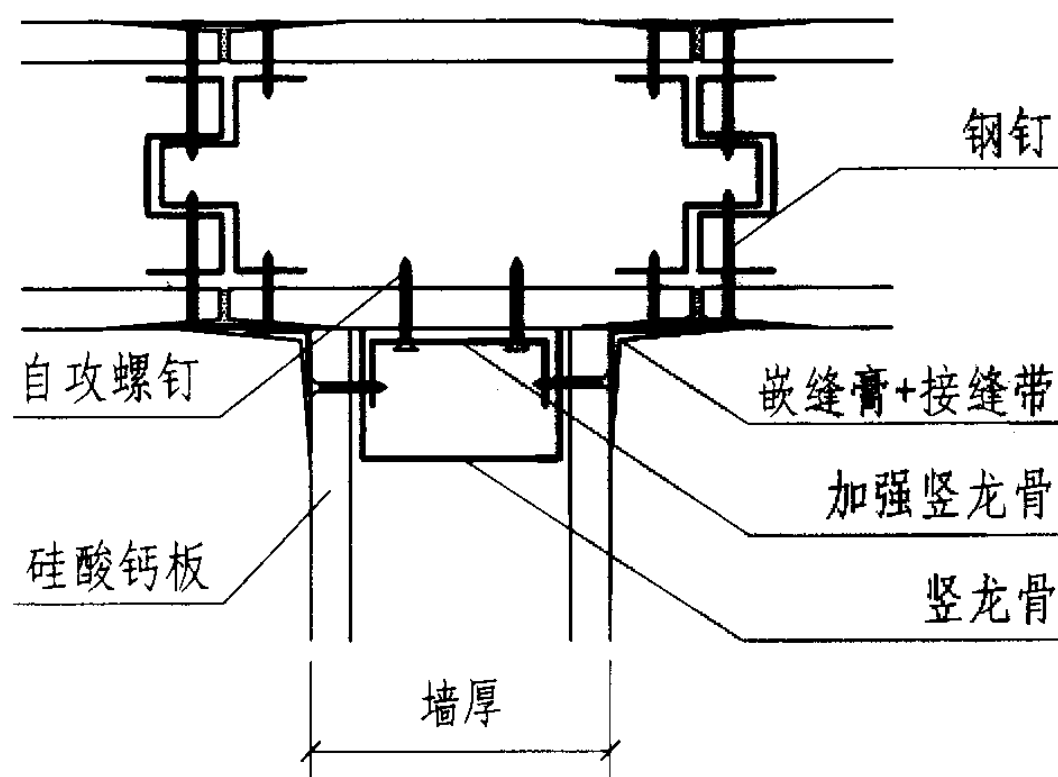

36 T形墙板连接

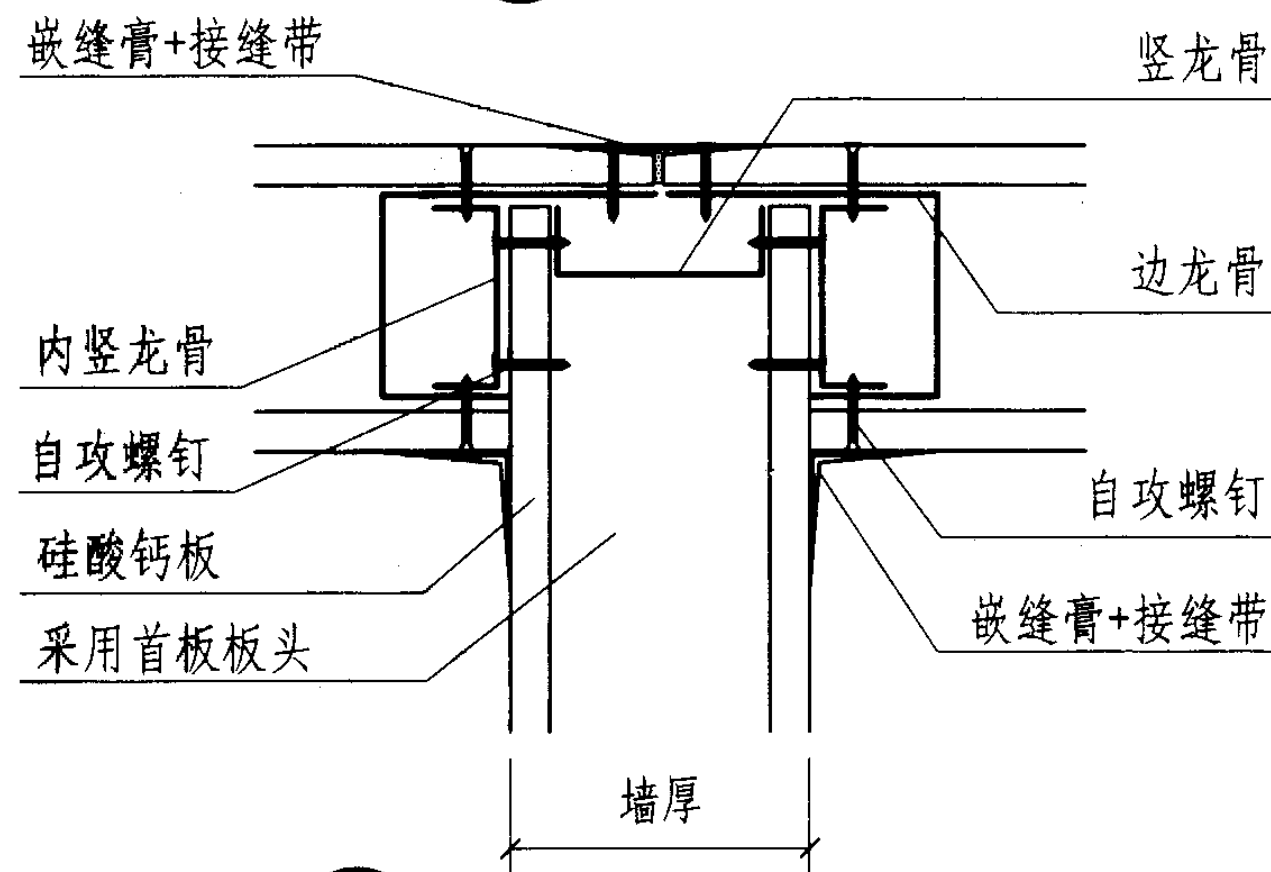


37 T形墙板连接

墙板连接节点 (一)


图集号 03J111-2

审核 李长发 校对 徐畅 设计 熊火生


页 27

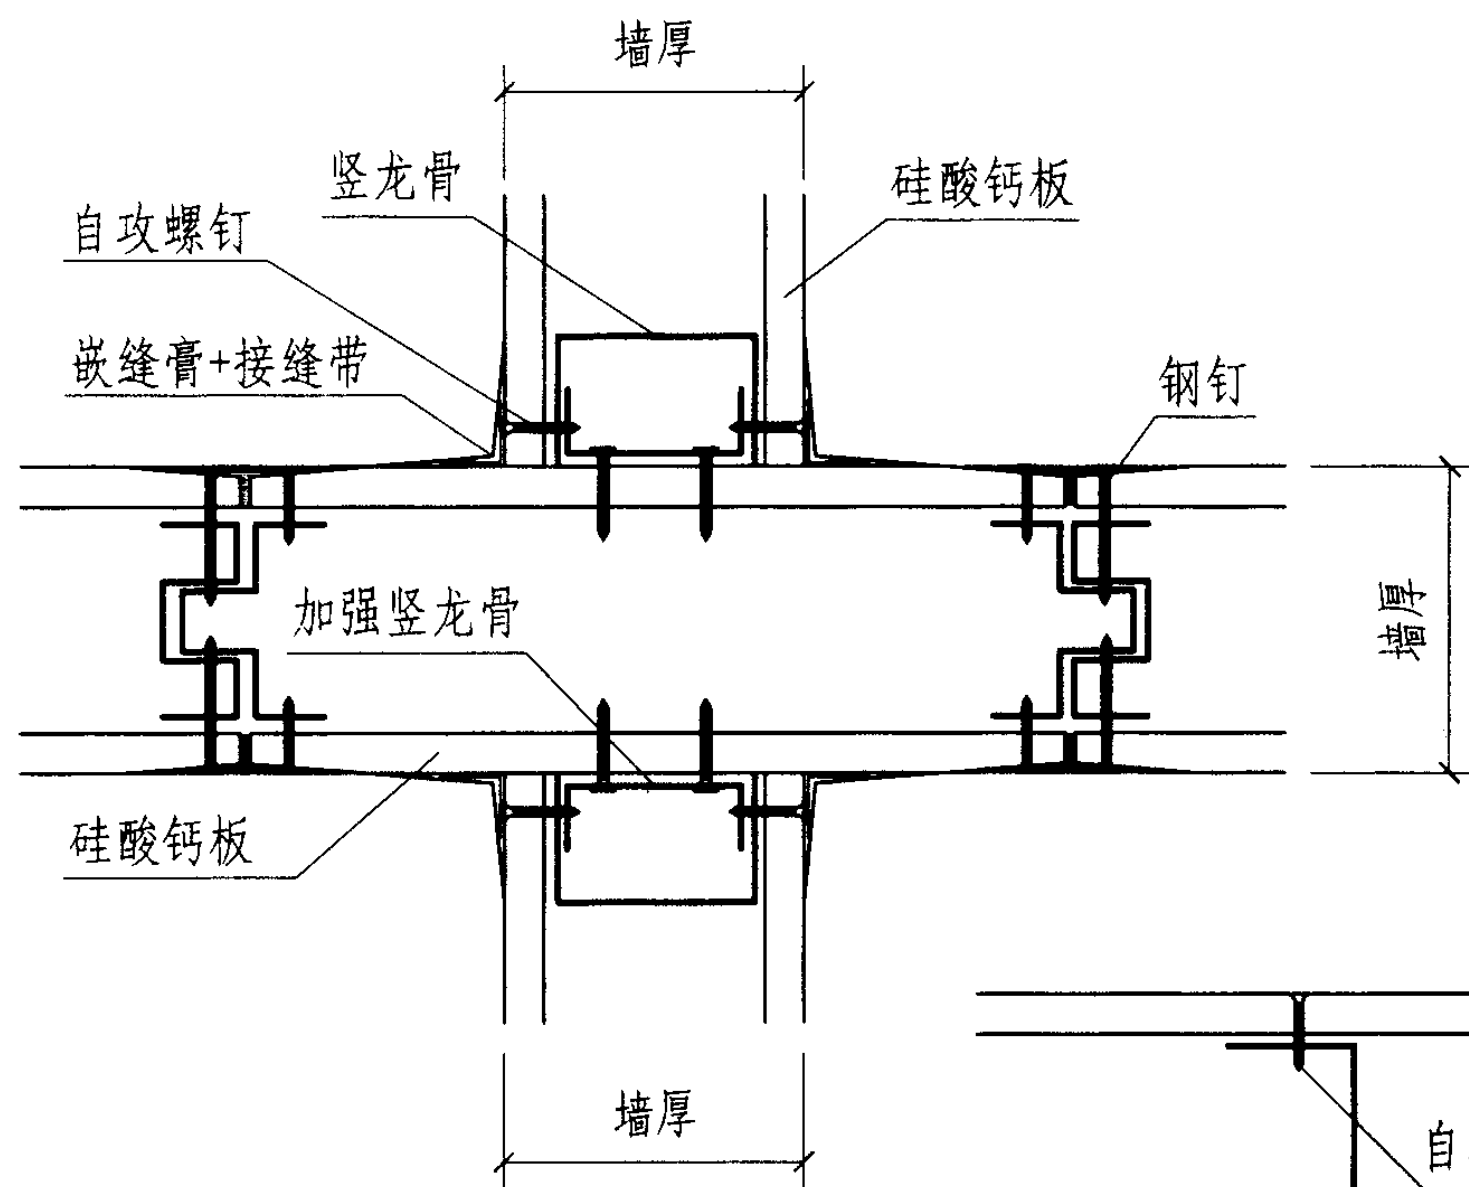

38 十字墙板连接

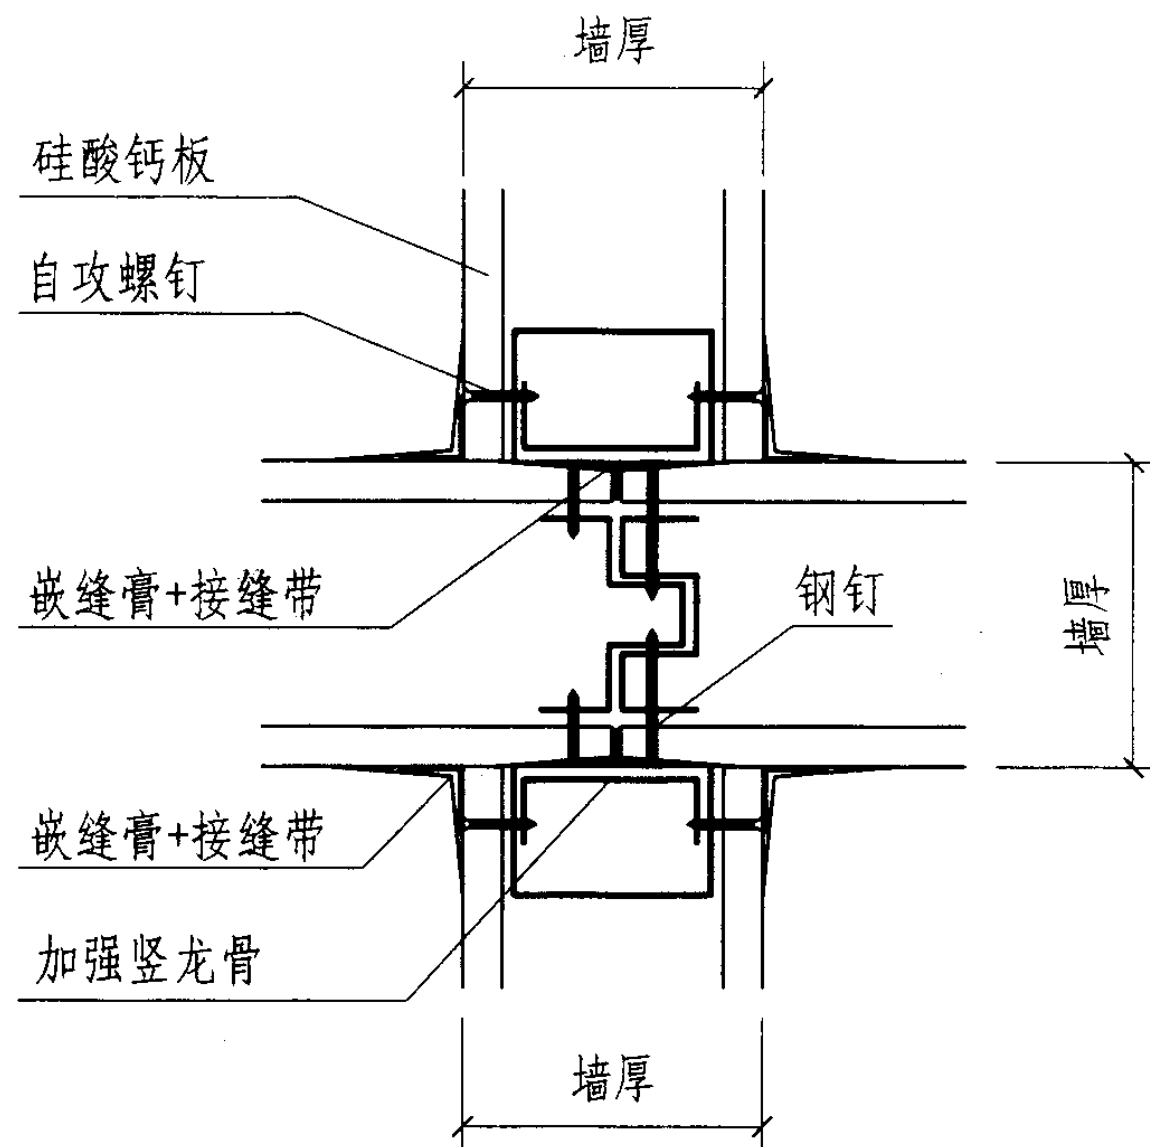

39 十字墙板连接

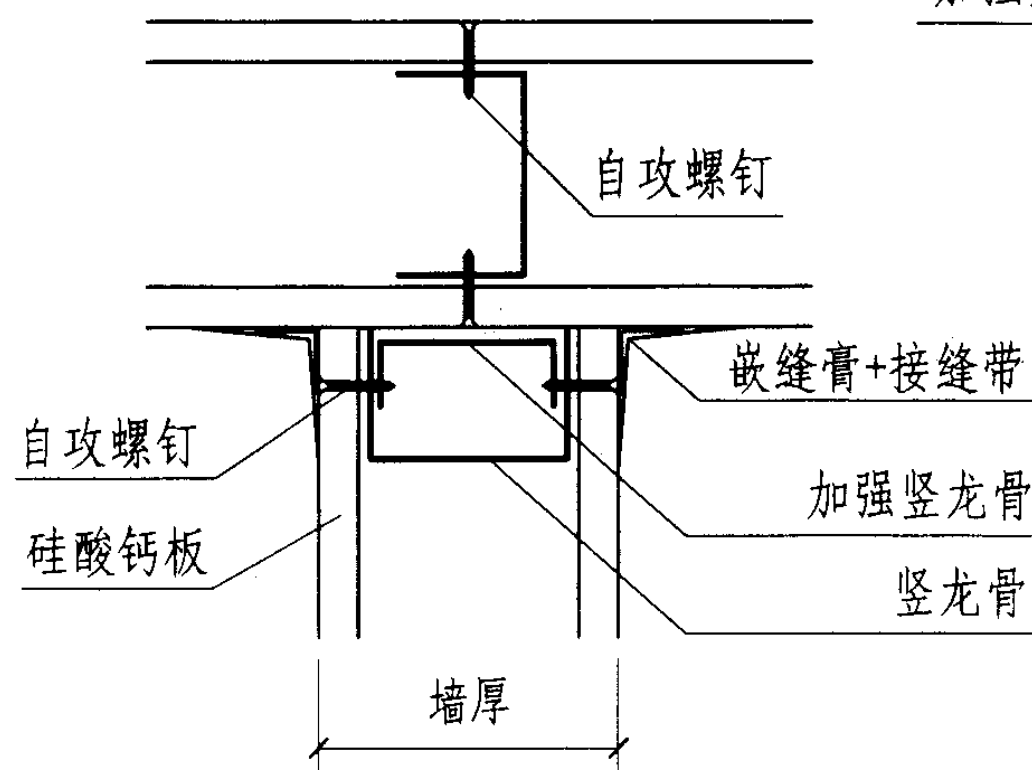


40 T形墙板连接

墙板连接节点 (二)


审核 李长发 校对 徐畅 设计 熊火生

图集号 03J111-2


页 28

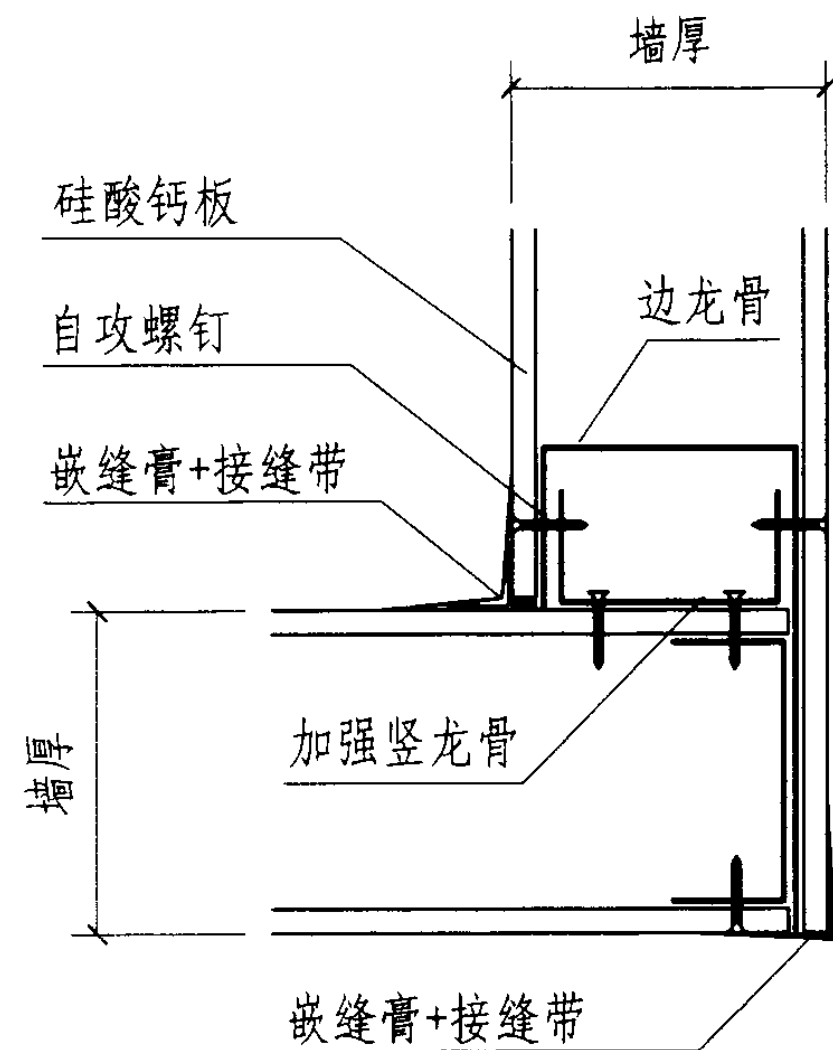

41

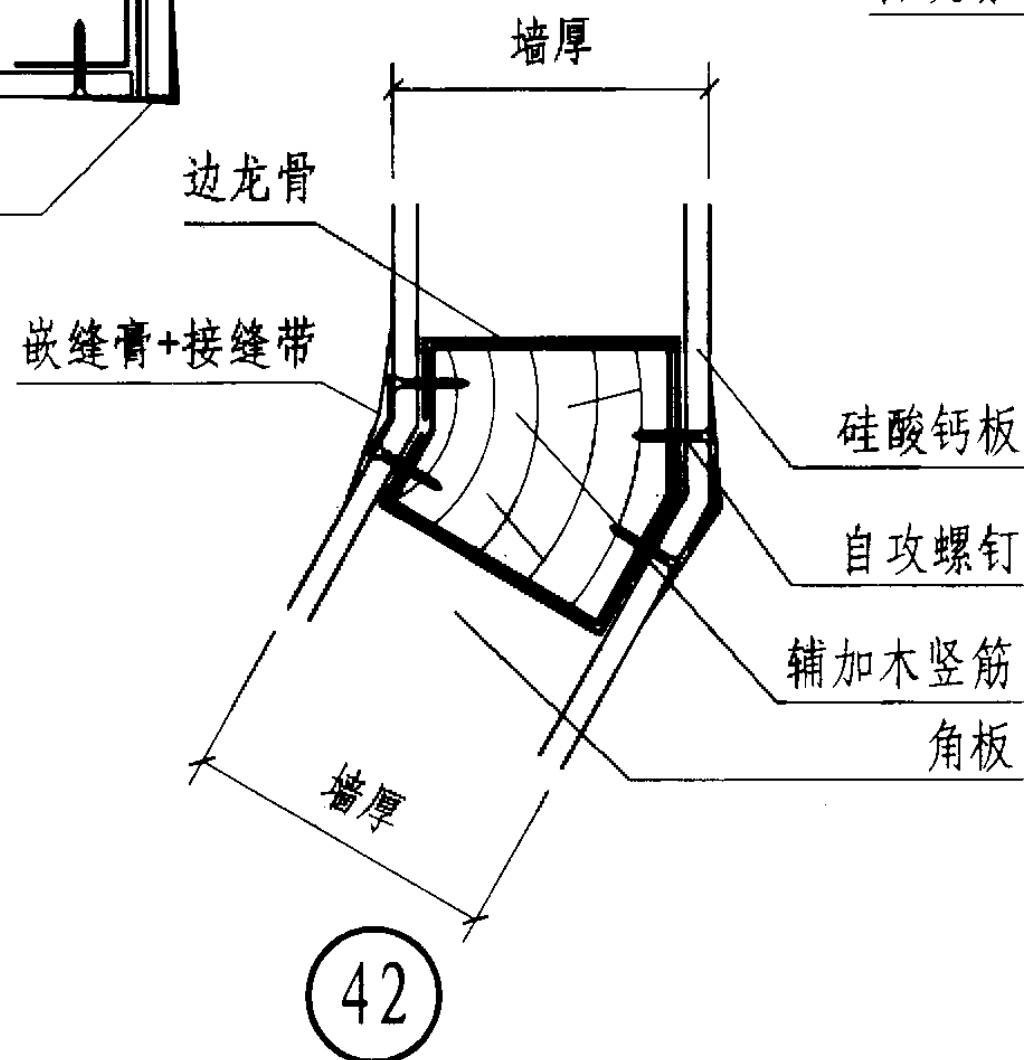

42

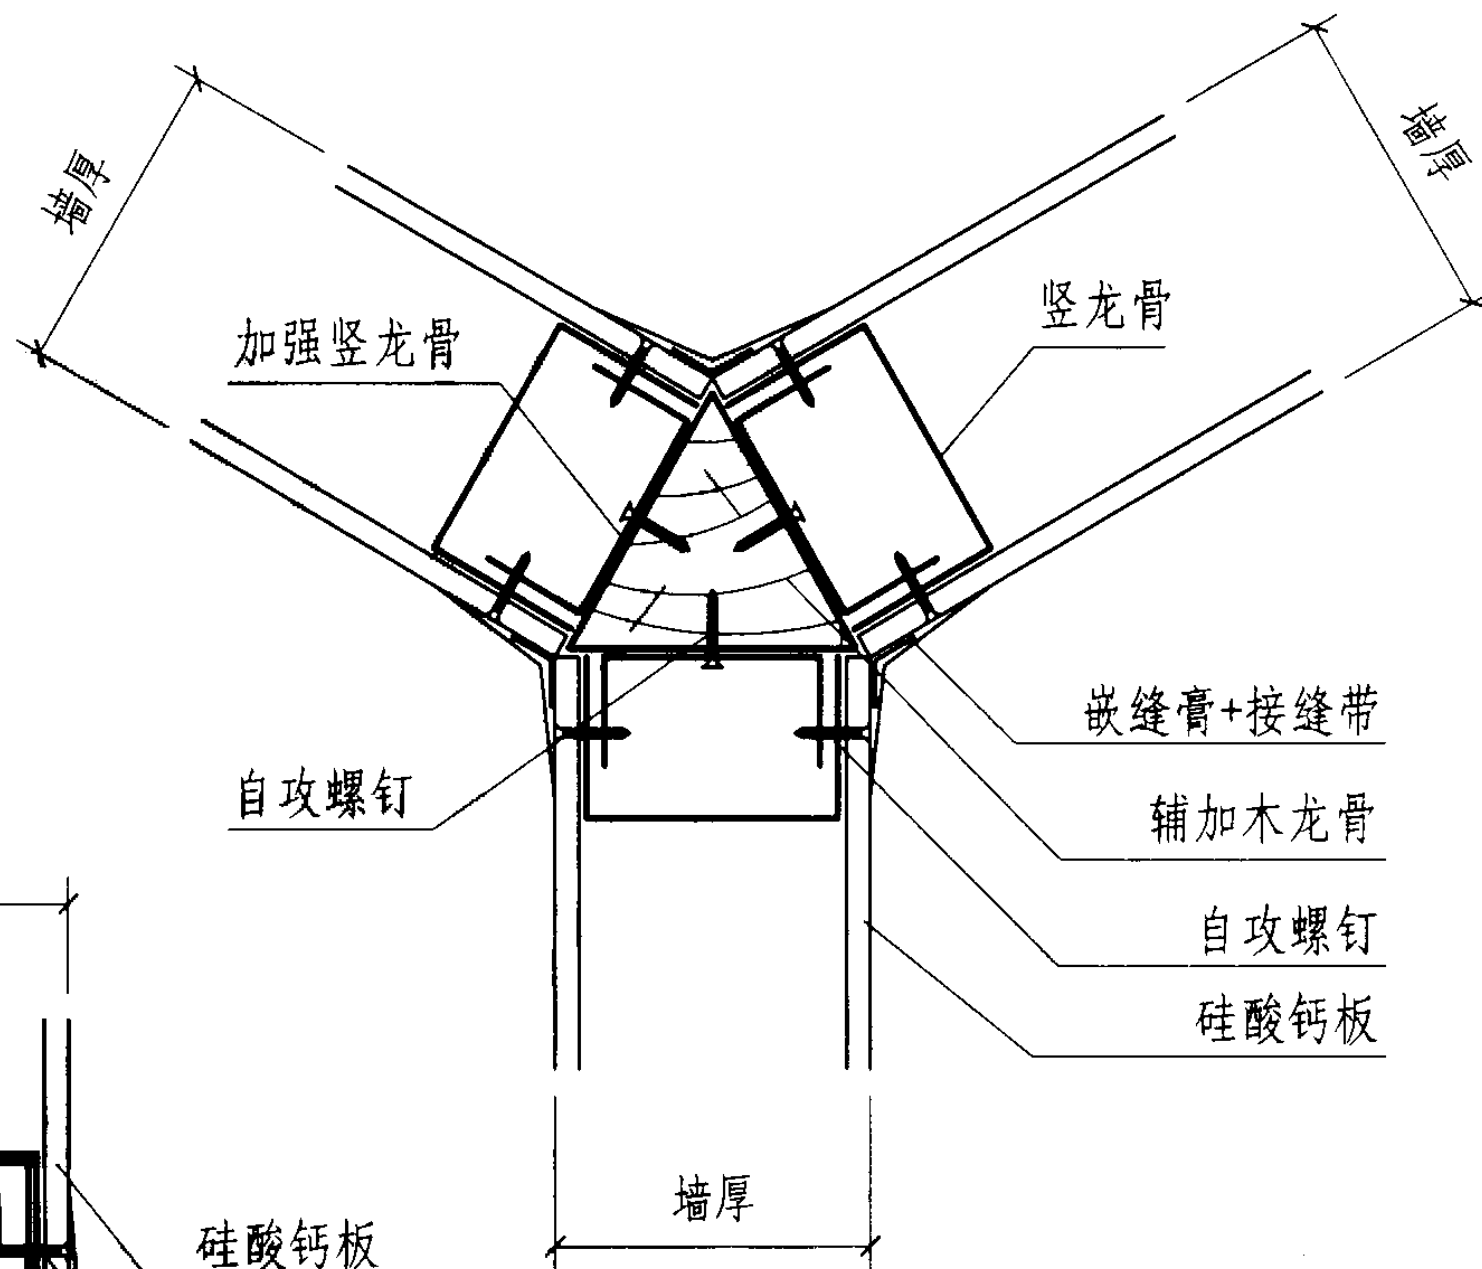

43

墙板连接节点 (三)

图集号

03J111-2

审核 李长发

校对

徐畅


徐畅

设计


熊火生

页


29

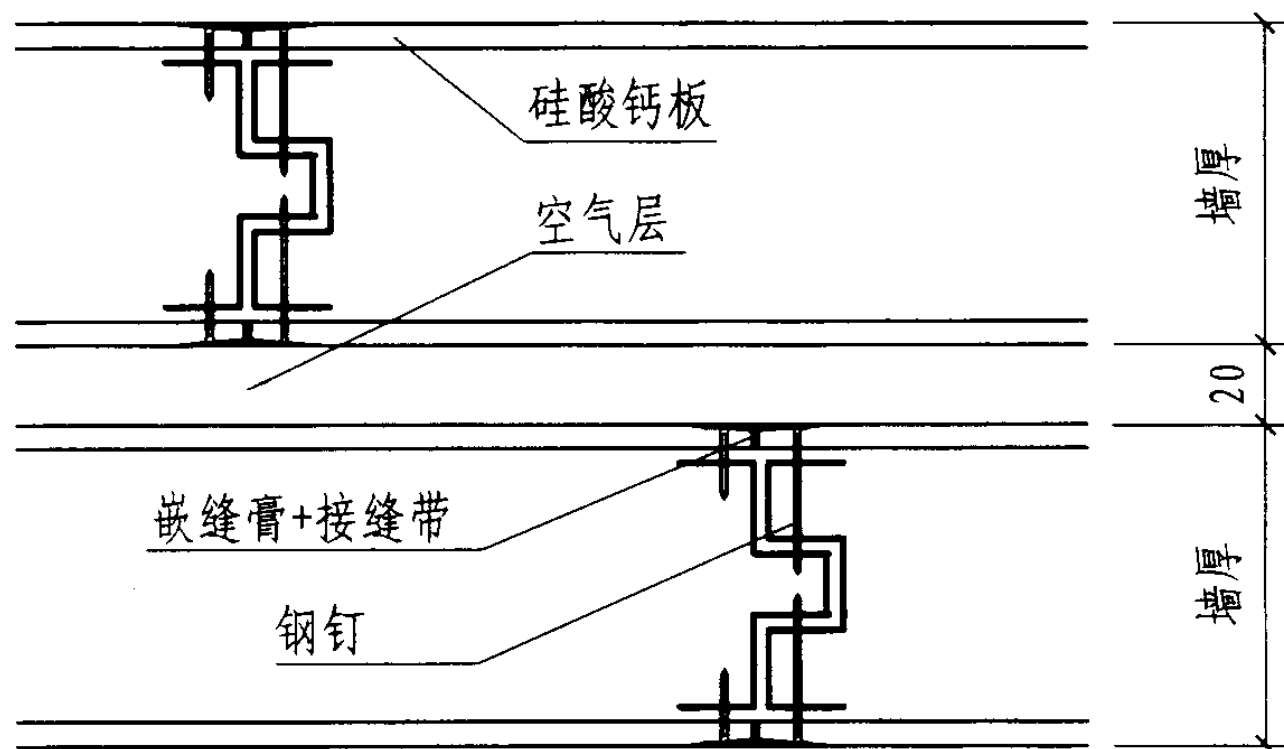

44 双层墙一字连接

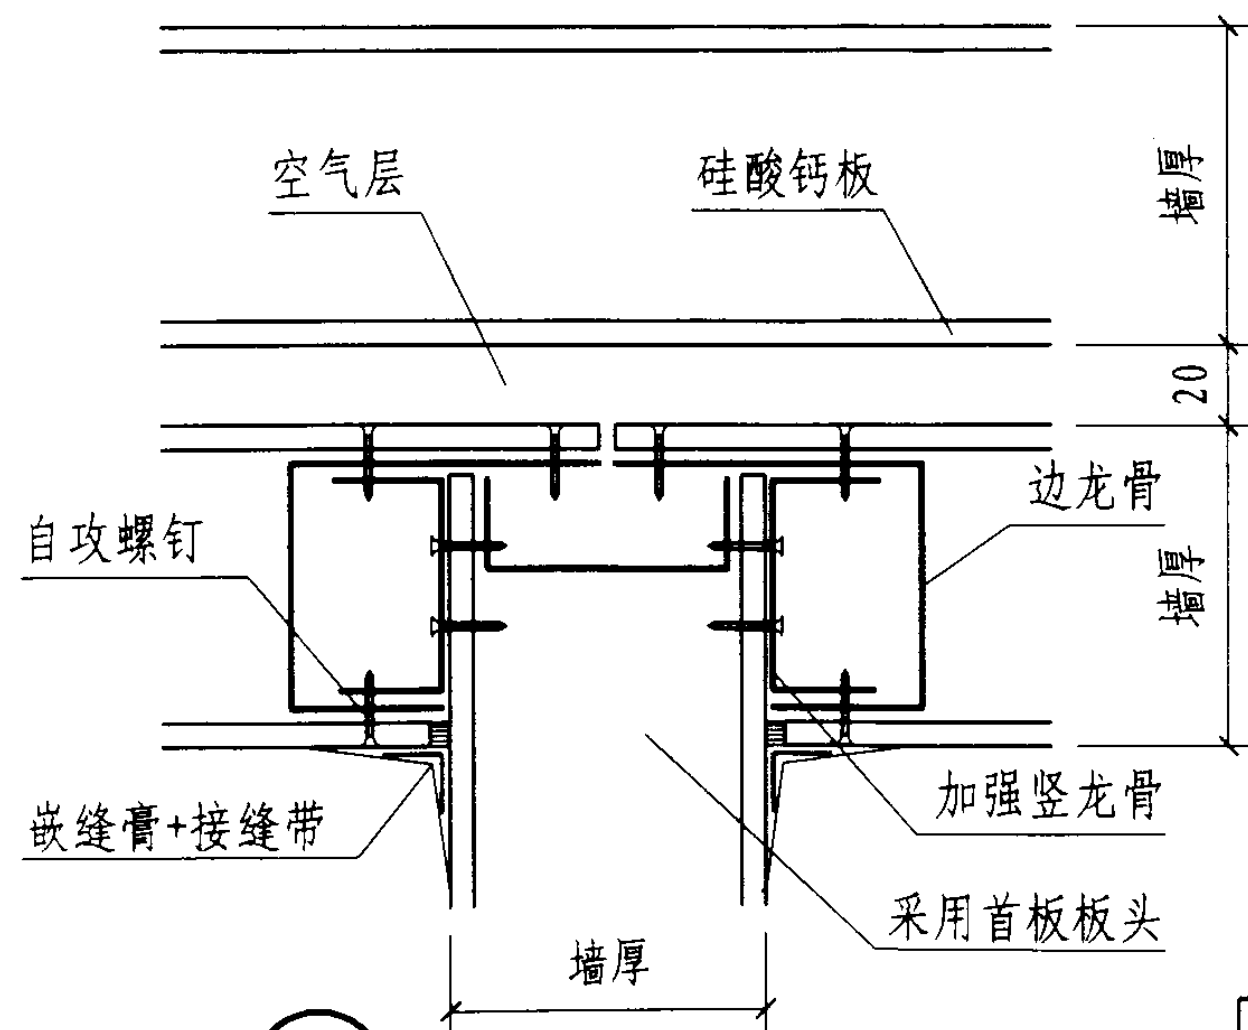

45 双层墙与单层墙连接

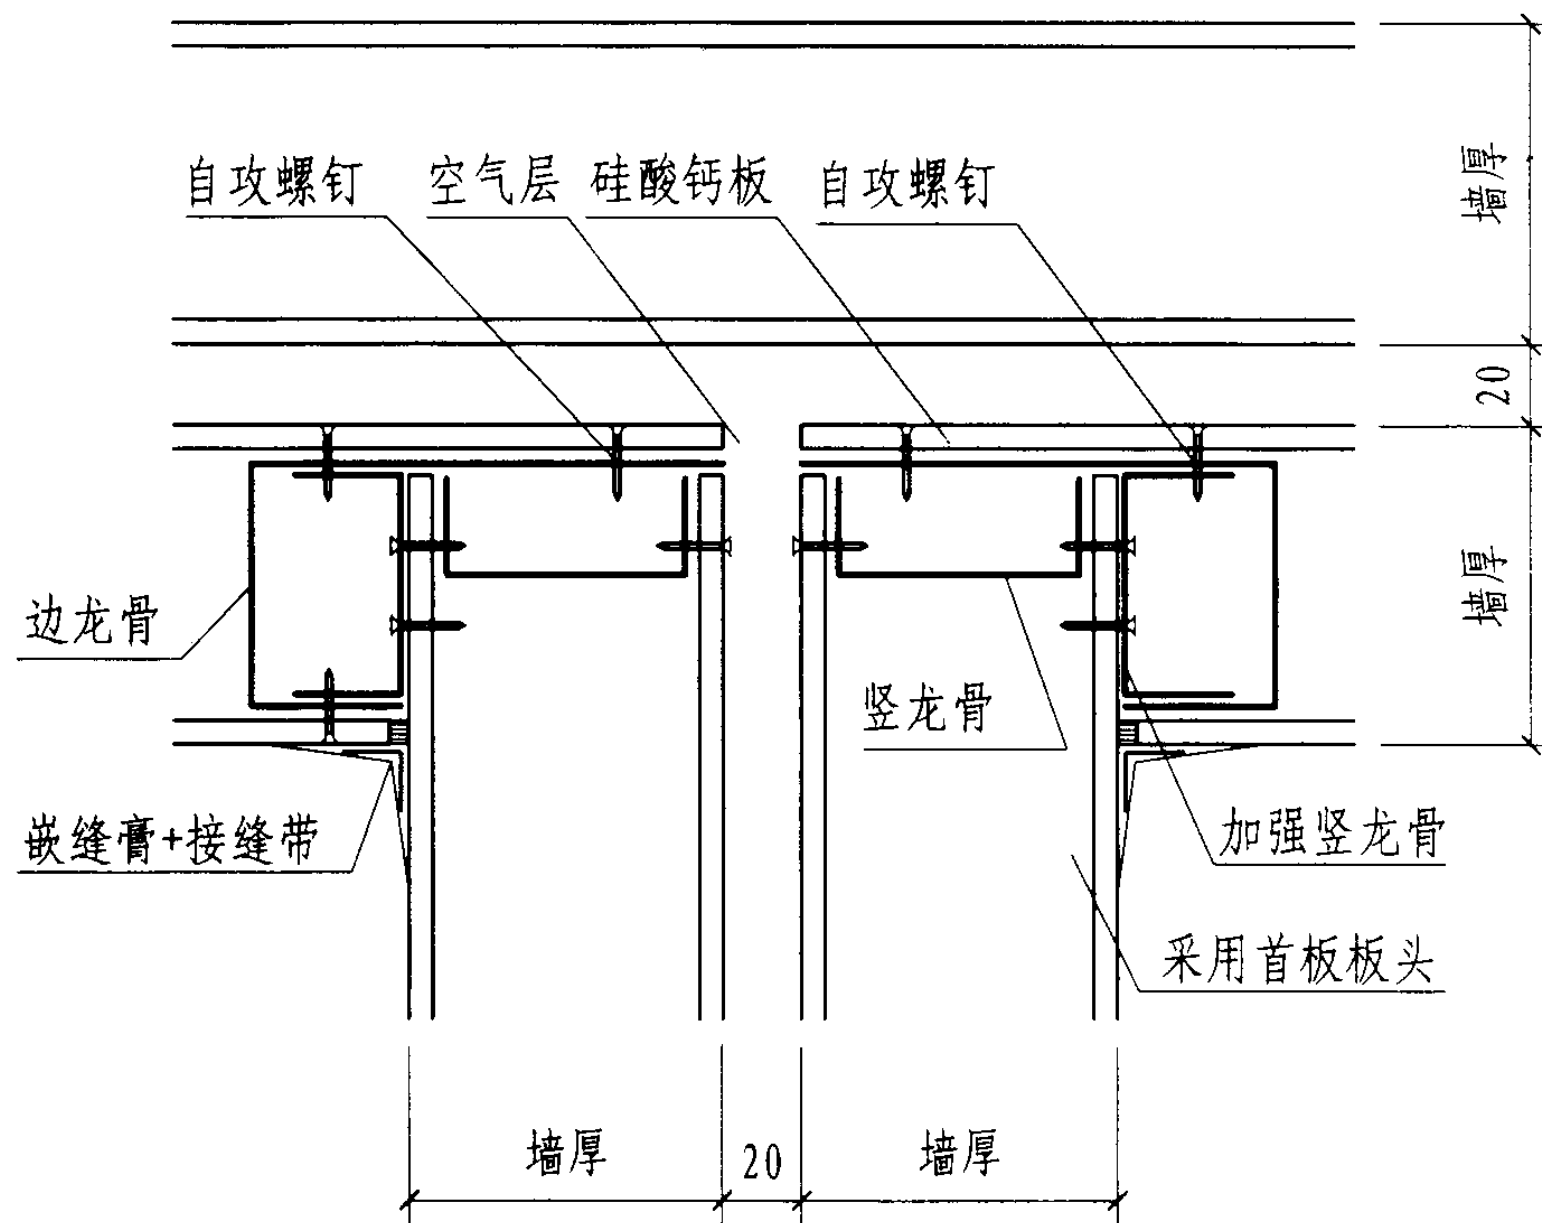

46 双层墙连接

双层墙板连接节点 (一)

图集号

03J111-2

审核

李长发

校对





徐畅

设计

熊火生

页

30

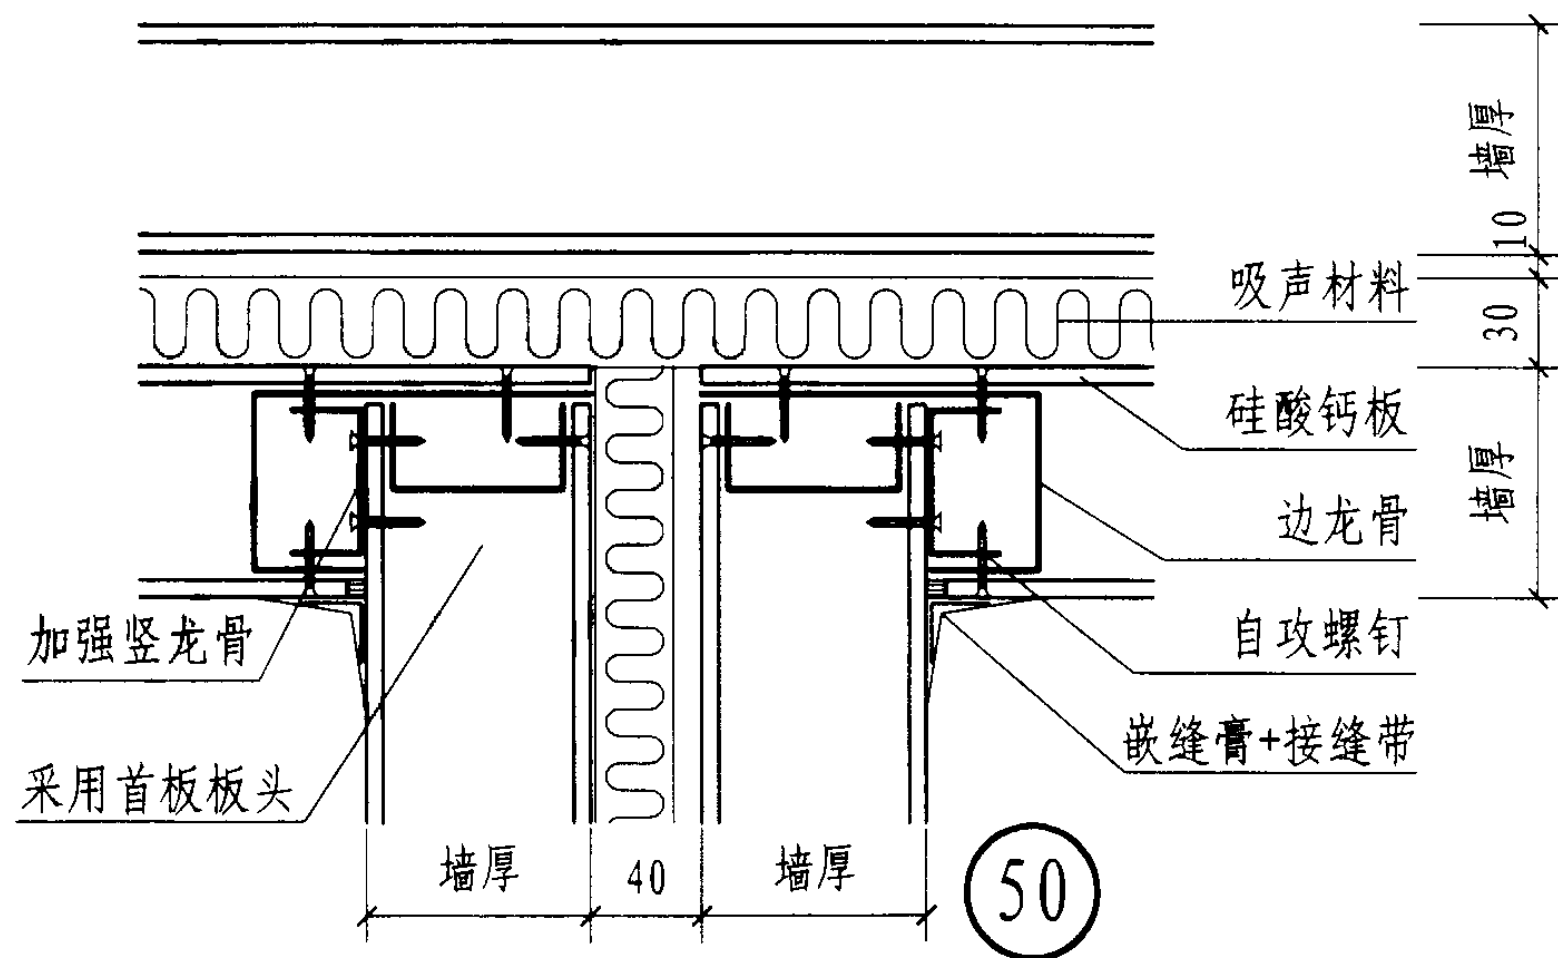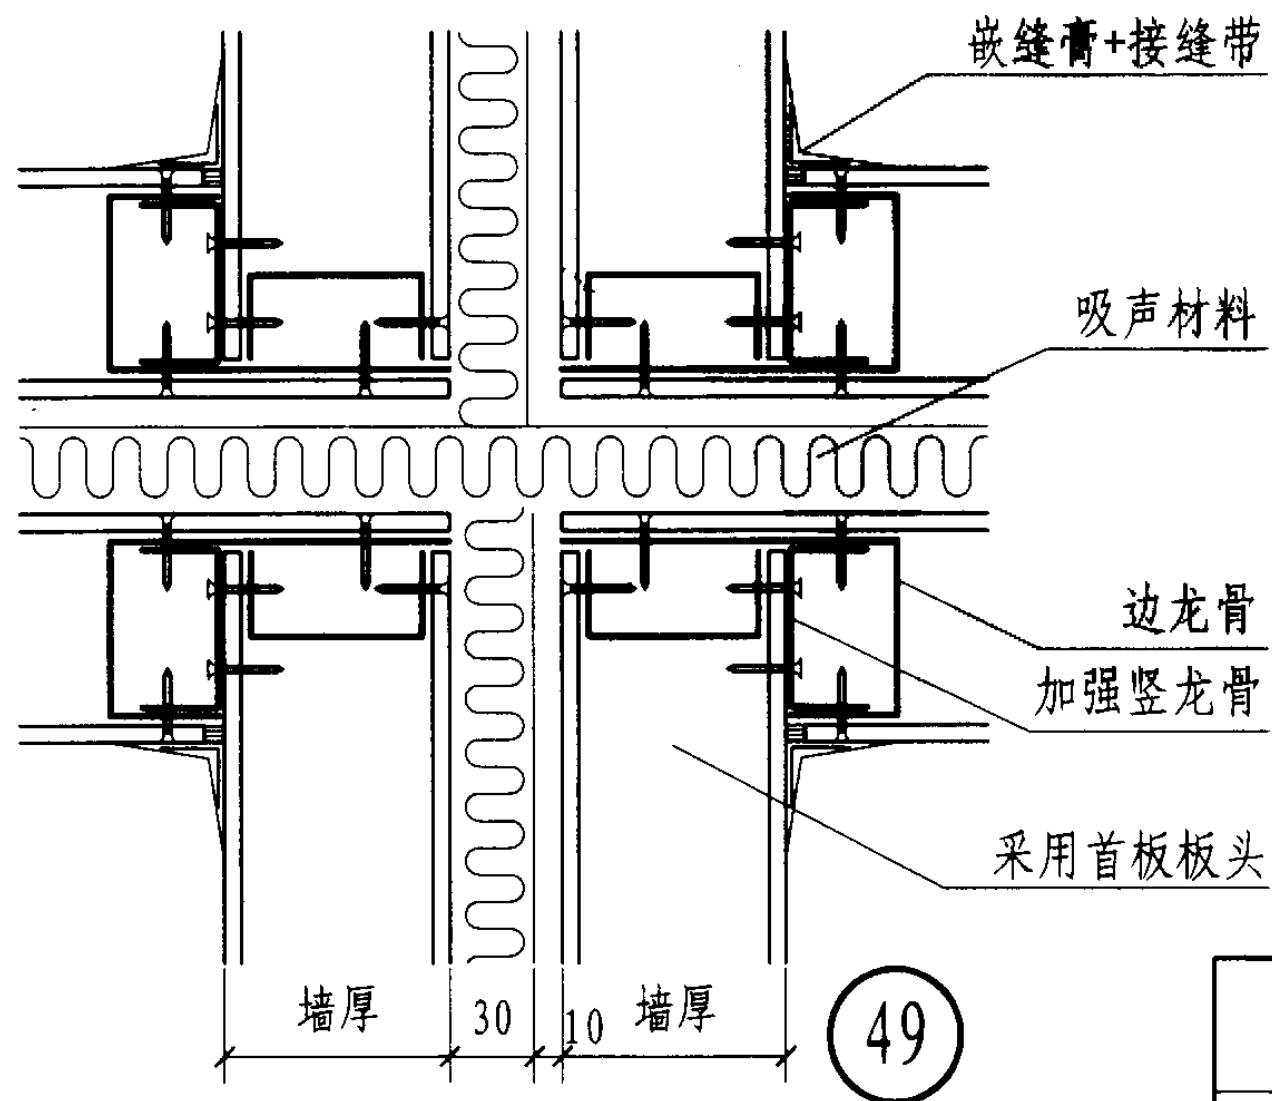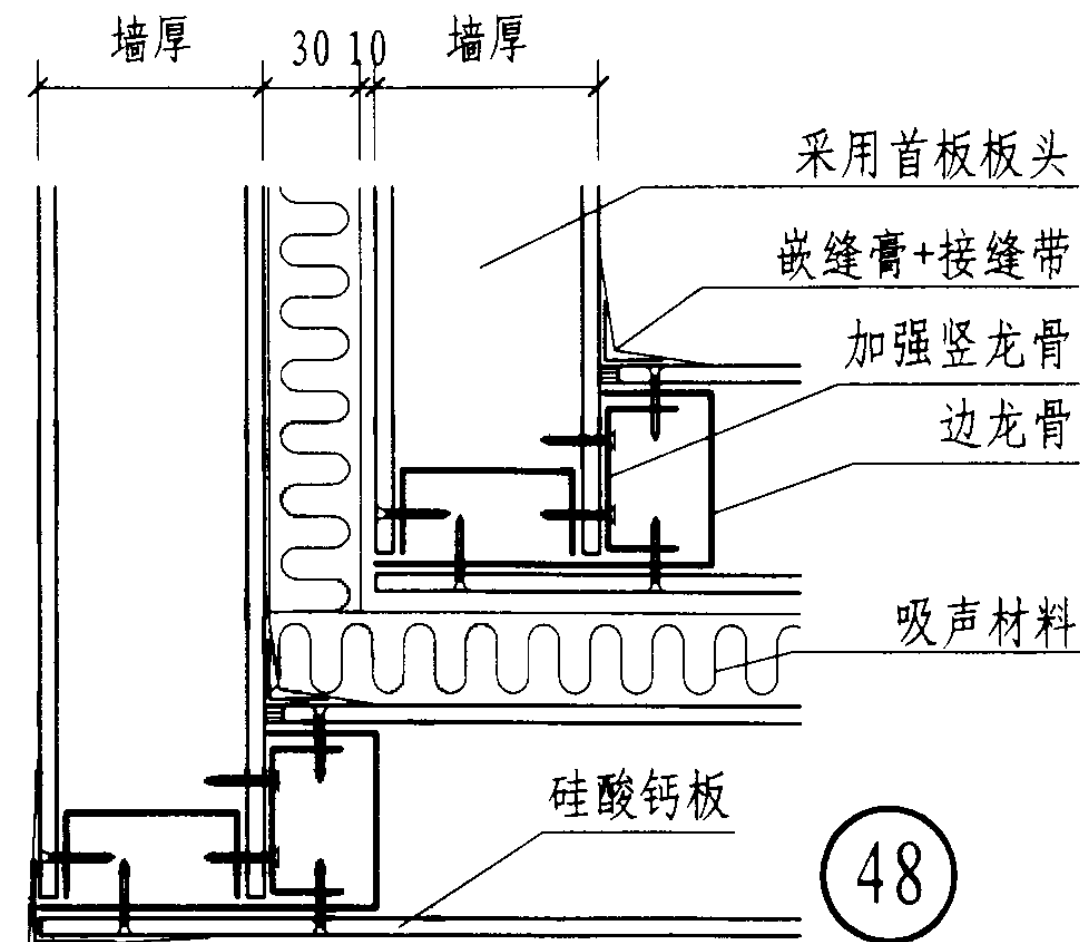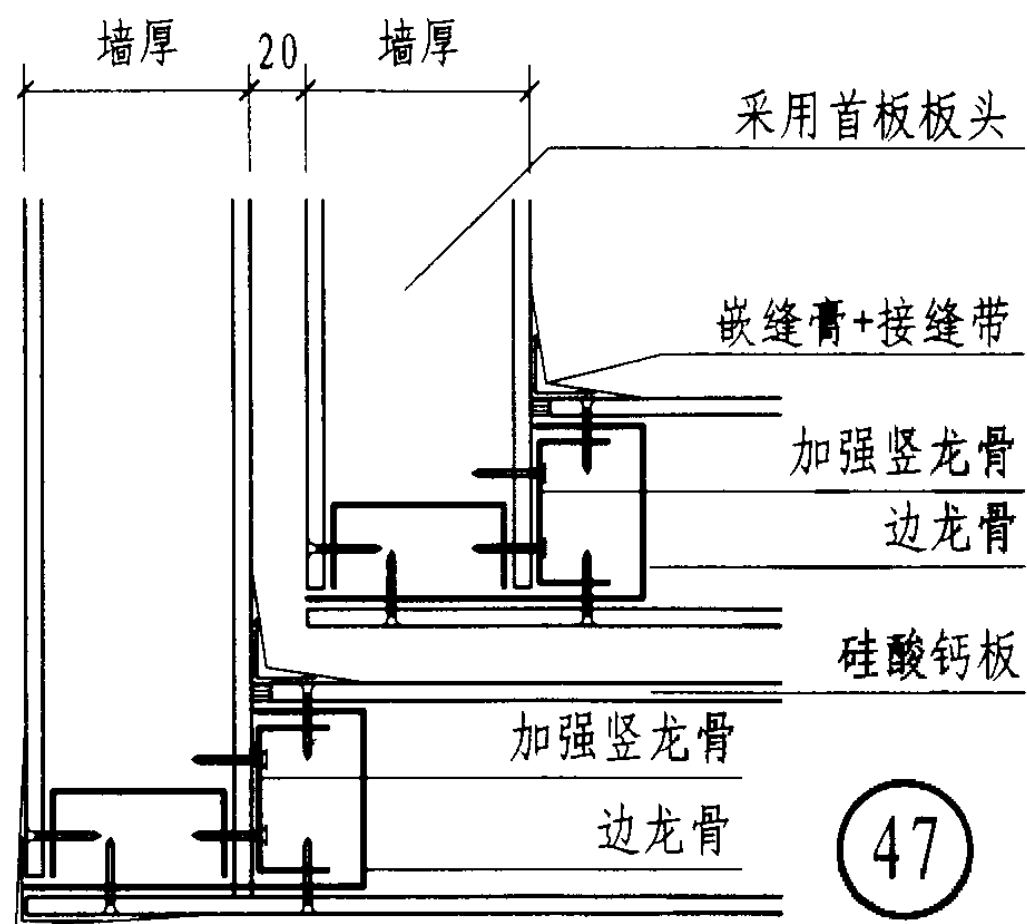


双层墙板连接节点 (二)


图集号 03J111-2

审核 李长发 校对 徐畅 设计 熊火生

页 31

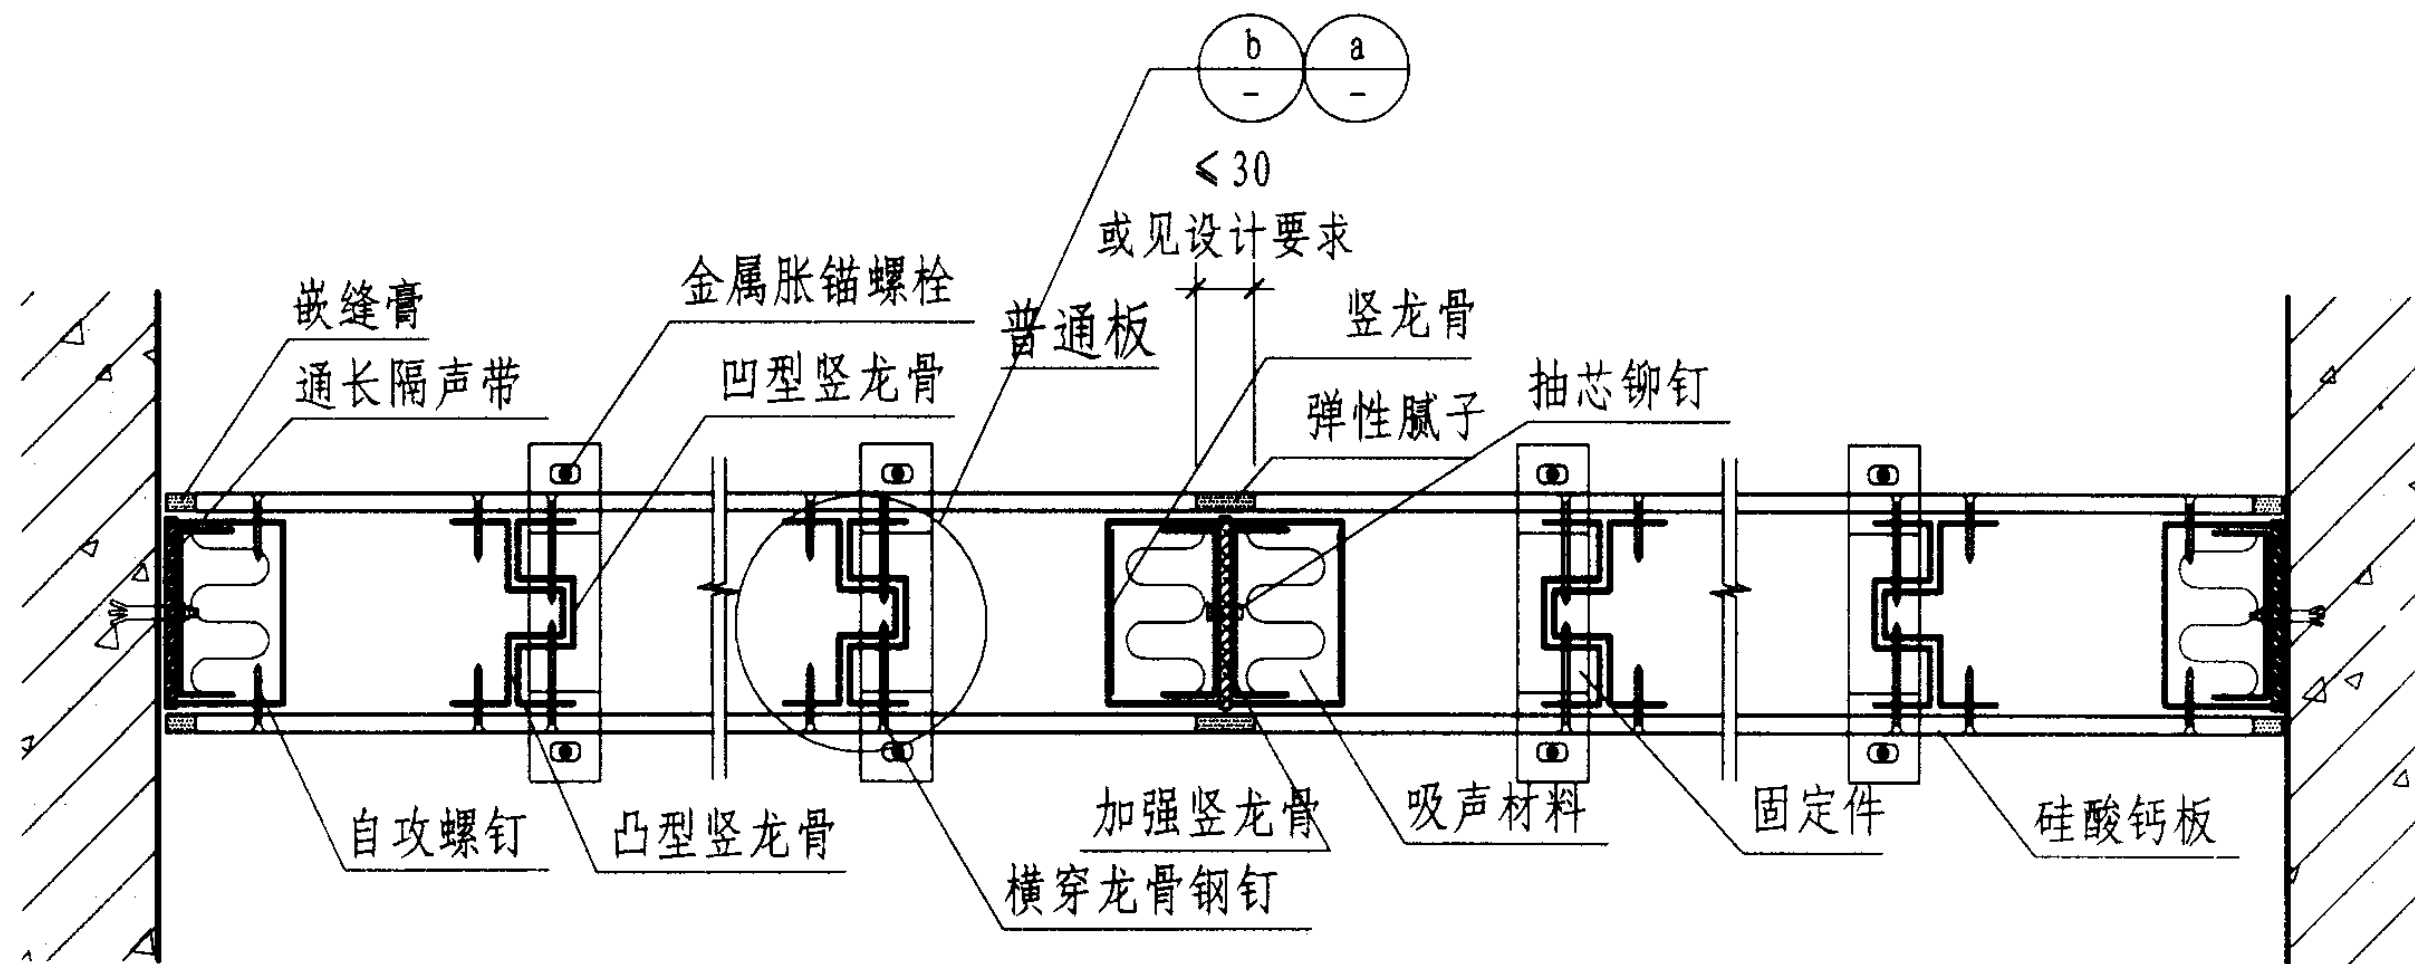


51

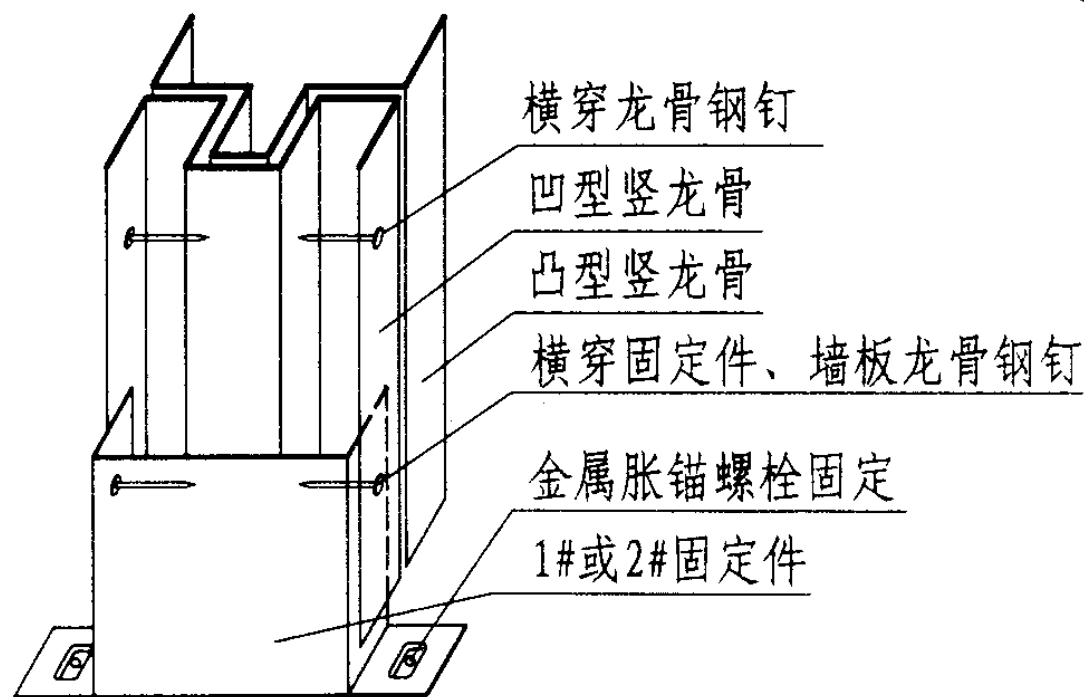

a

与楼地面固定

注：弹性腻子的宽度为墙板伸缩缝尺寸

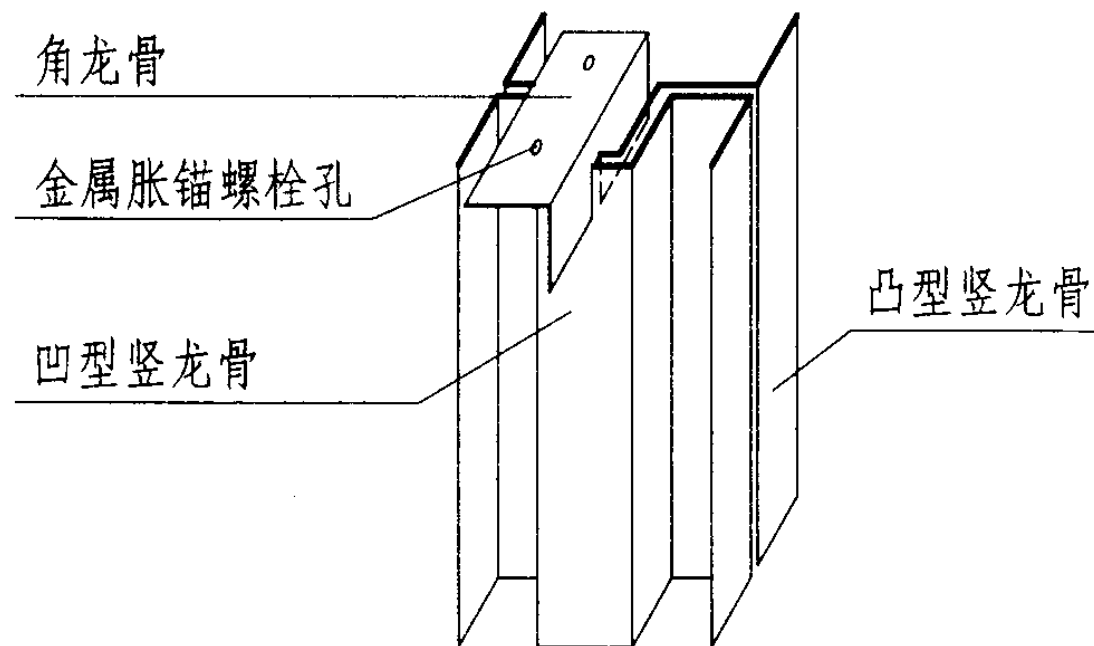

b

与楼板顶固定

墙体伸缩缝节点

图集号

03J111-2

审核

李长发

校对

徐畅


徐畅

设计


熊火生

页


32

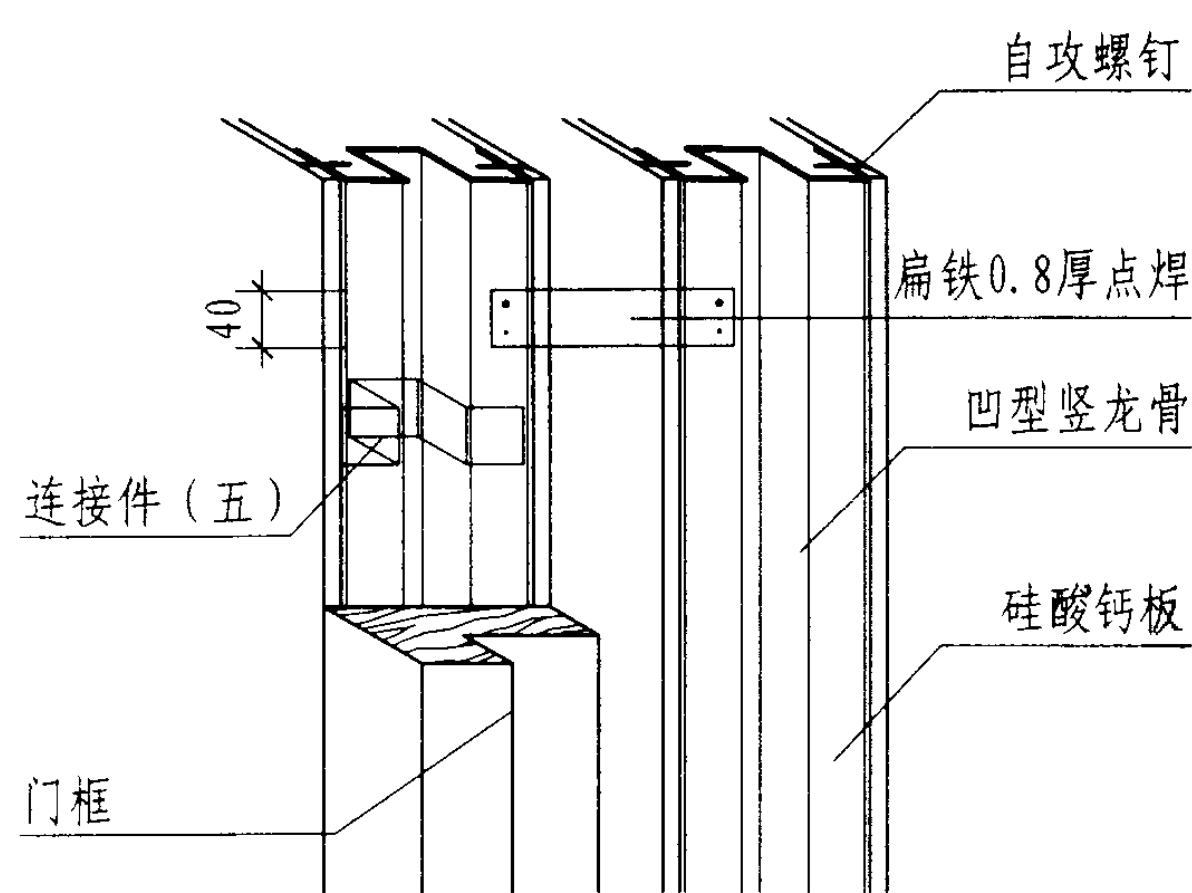


墙板与门框连接示意图

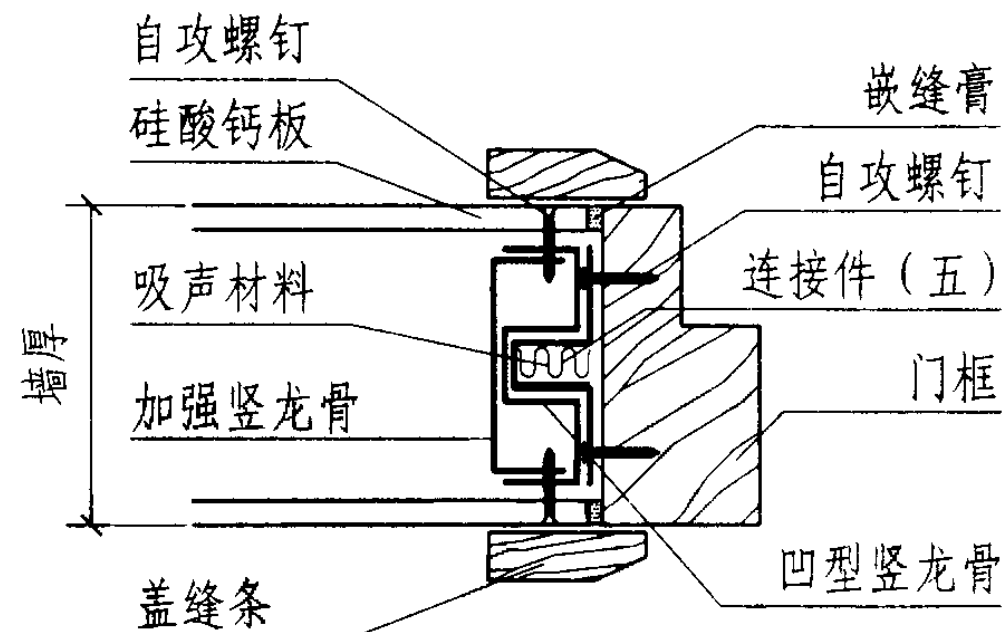


52 门框宽度 > 1000做法

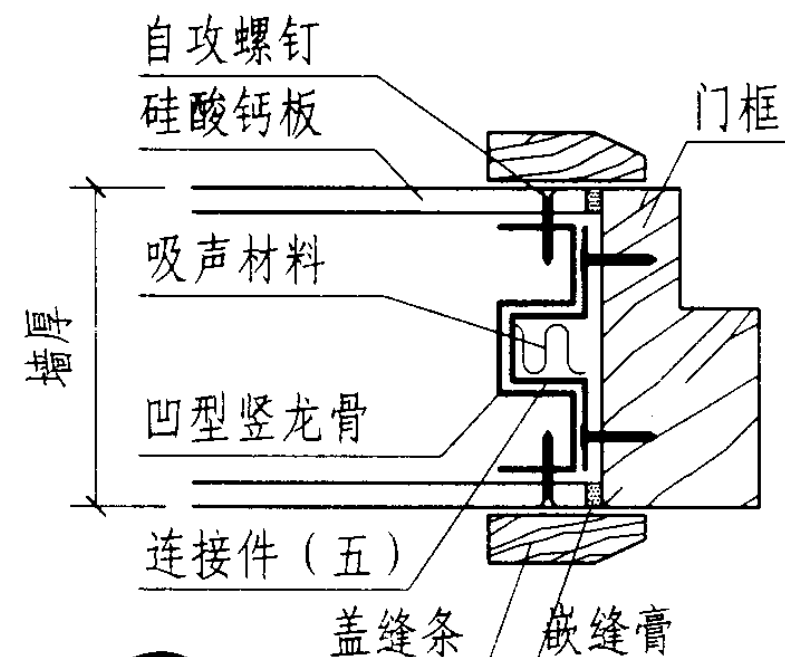

53 门框宽度 < 1000做法

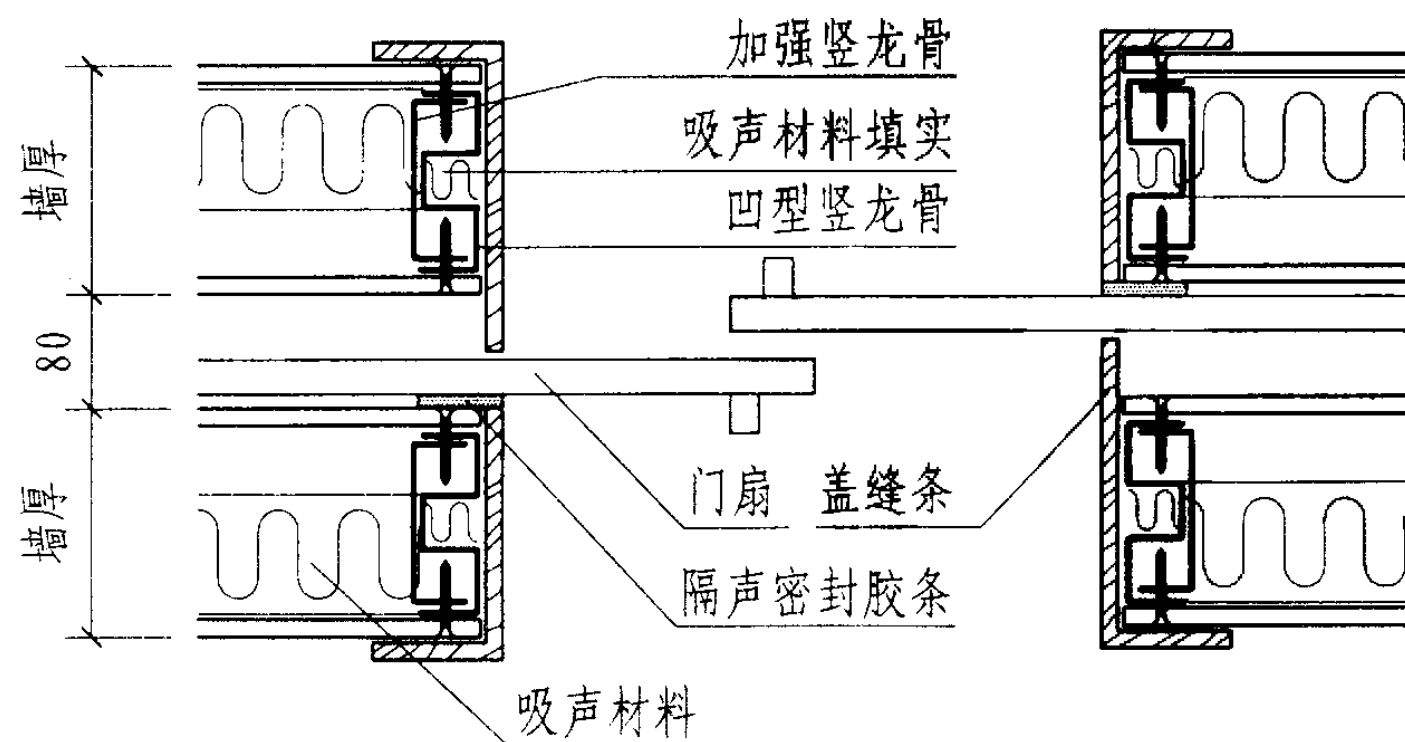


54 墙板与推拉门做法

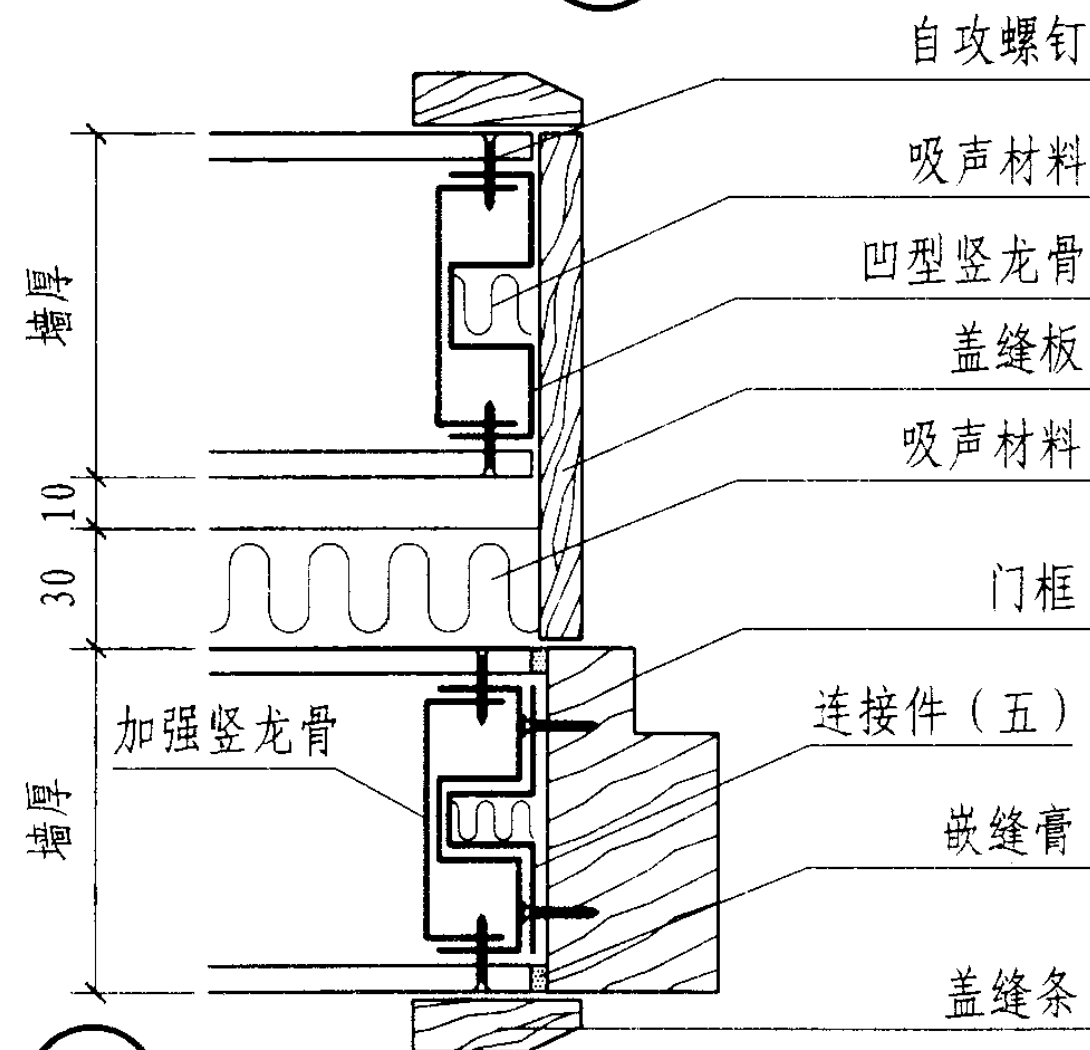

55 双层墙板与门框连接做法


注: 1. 当门洞宽度大于1000采用做法 52。
2. 窗洞做法同门洞。

墙板与门窗框连接节点								图集号	03J111-2
审核	李长发	校对	徐畅	徐畅	设计	熊火生	页	33	

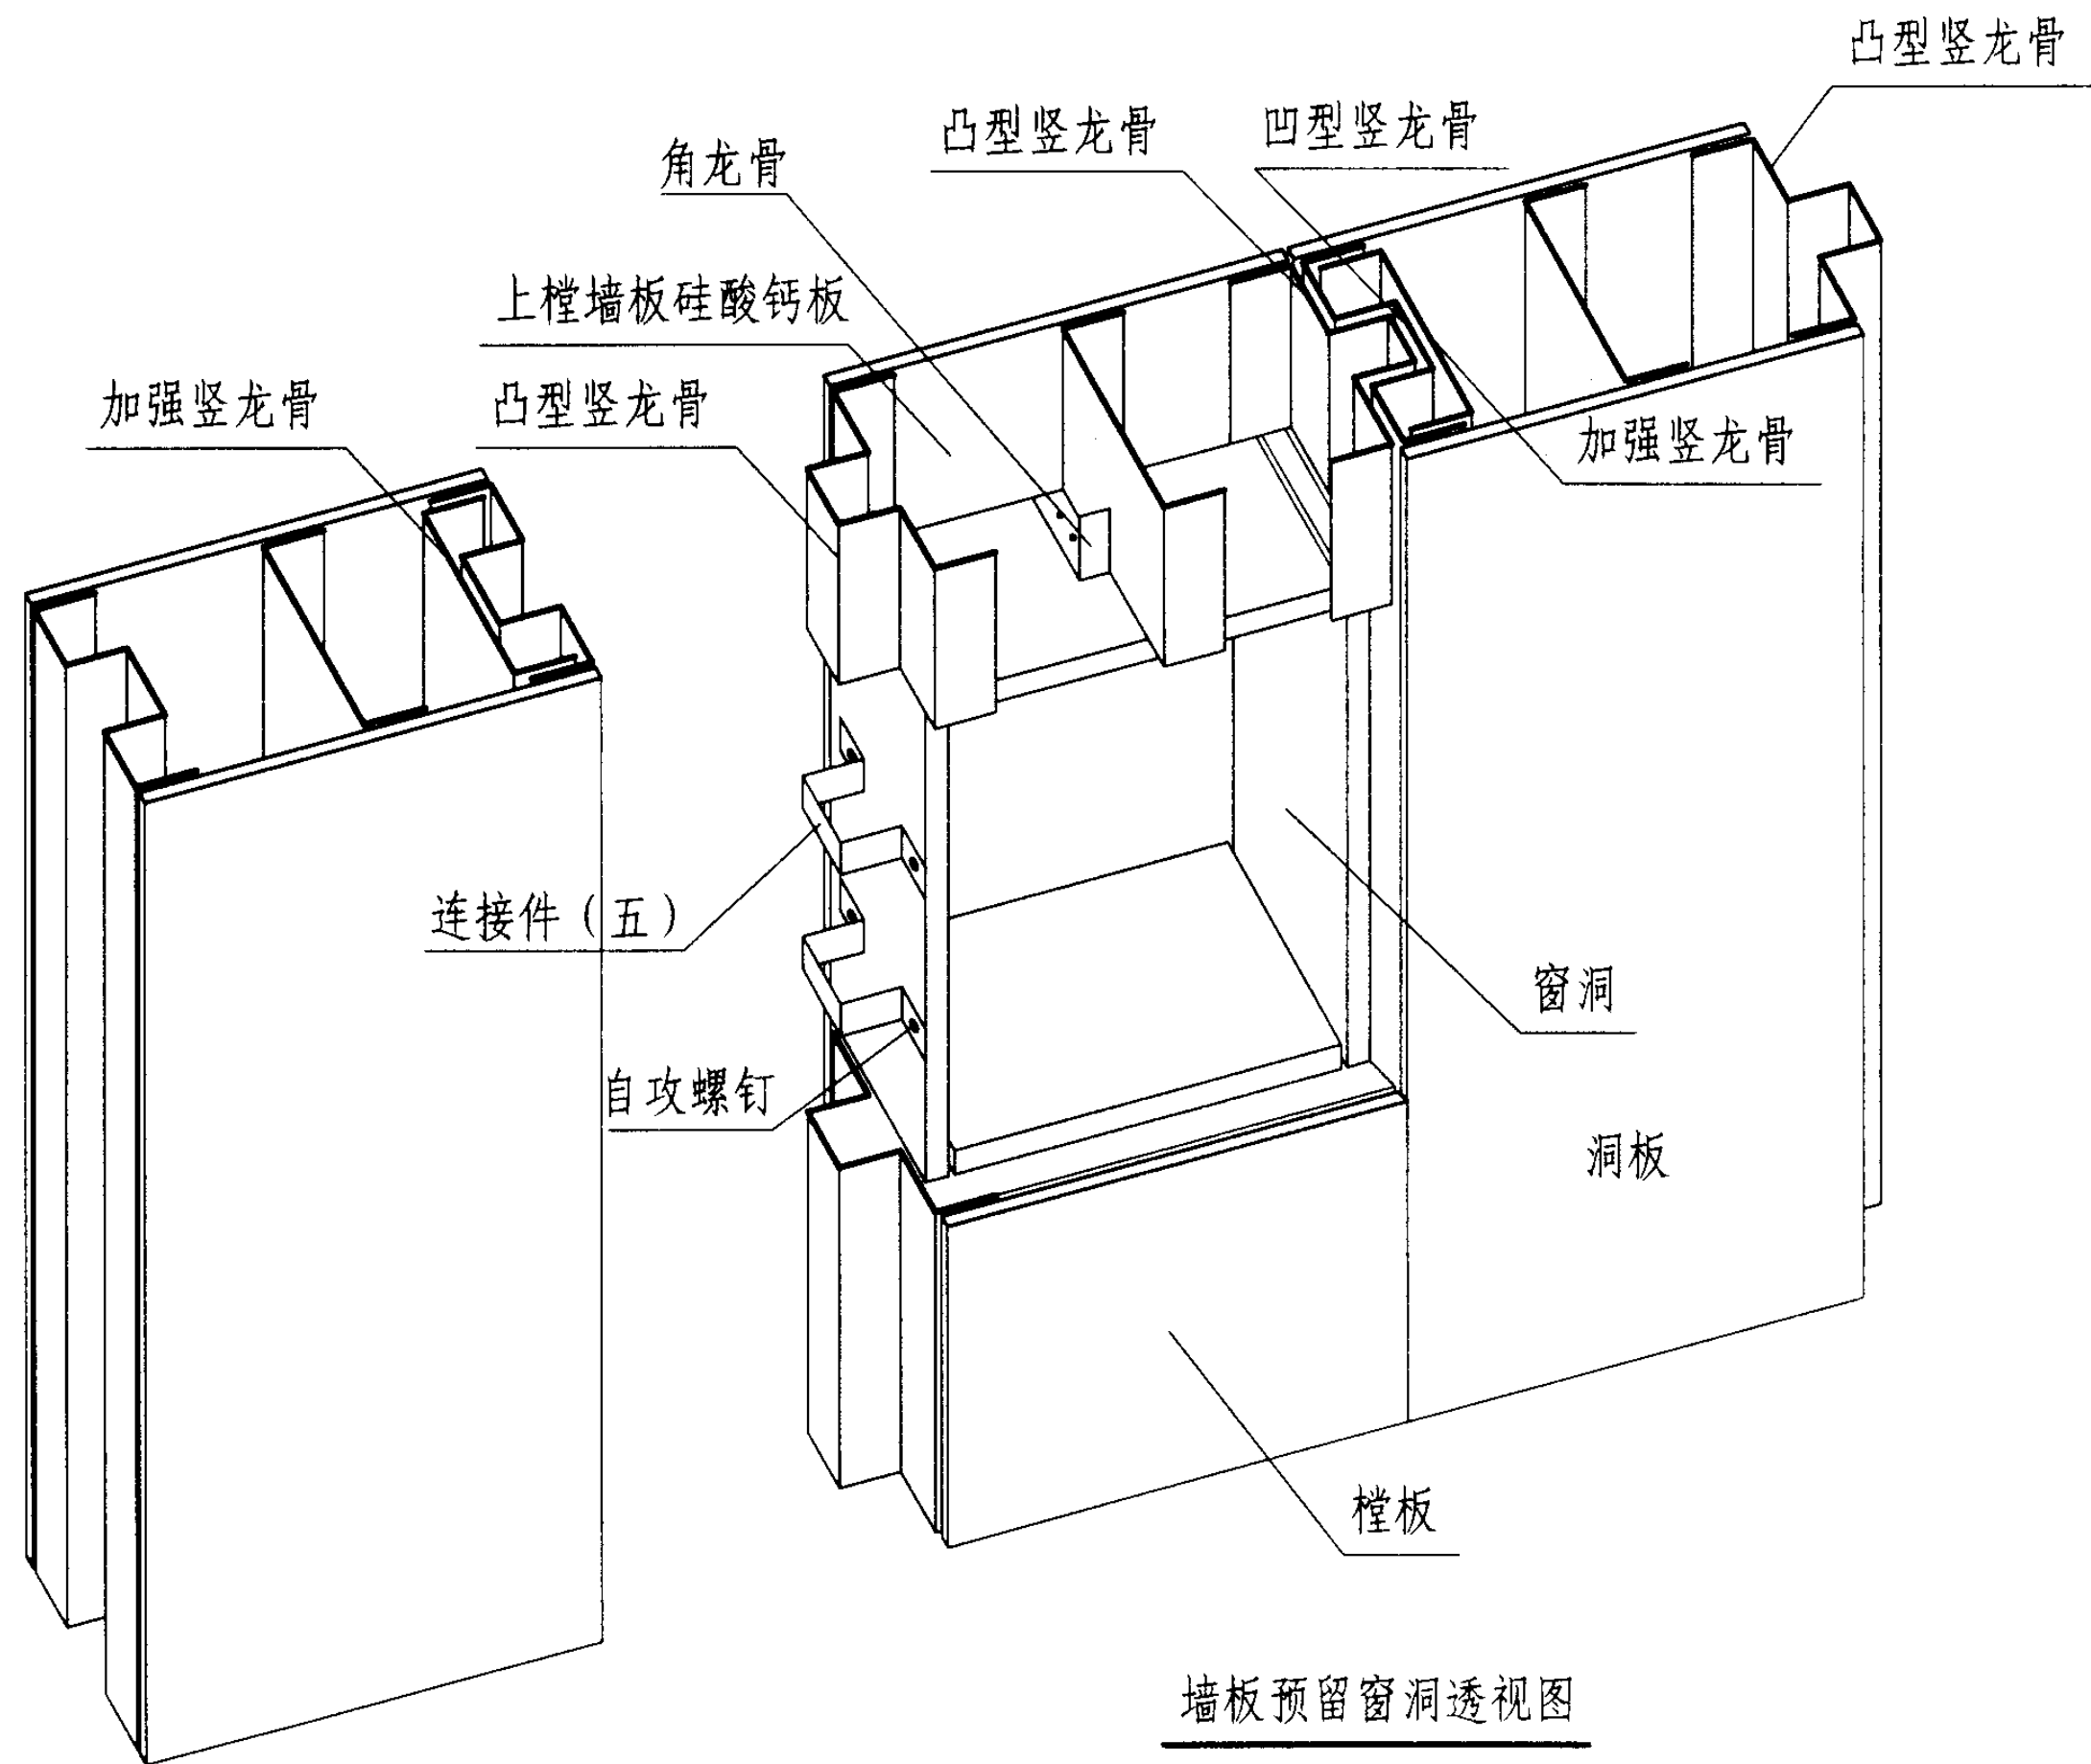


墙板预留窗洞透视图

墙板预留窗洞透视图								图集号	03J111-2
审核	李长发	徐畅	校对	徐畅	设计	熊火生	熊火生	页	34

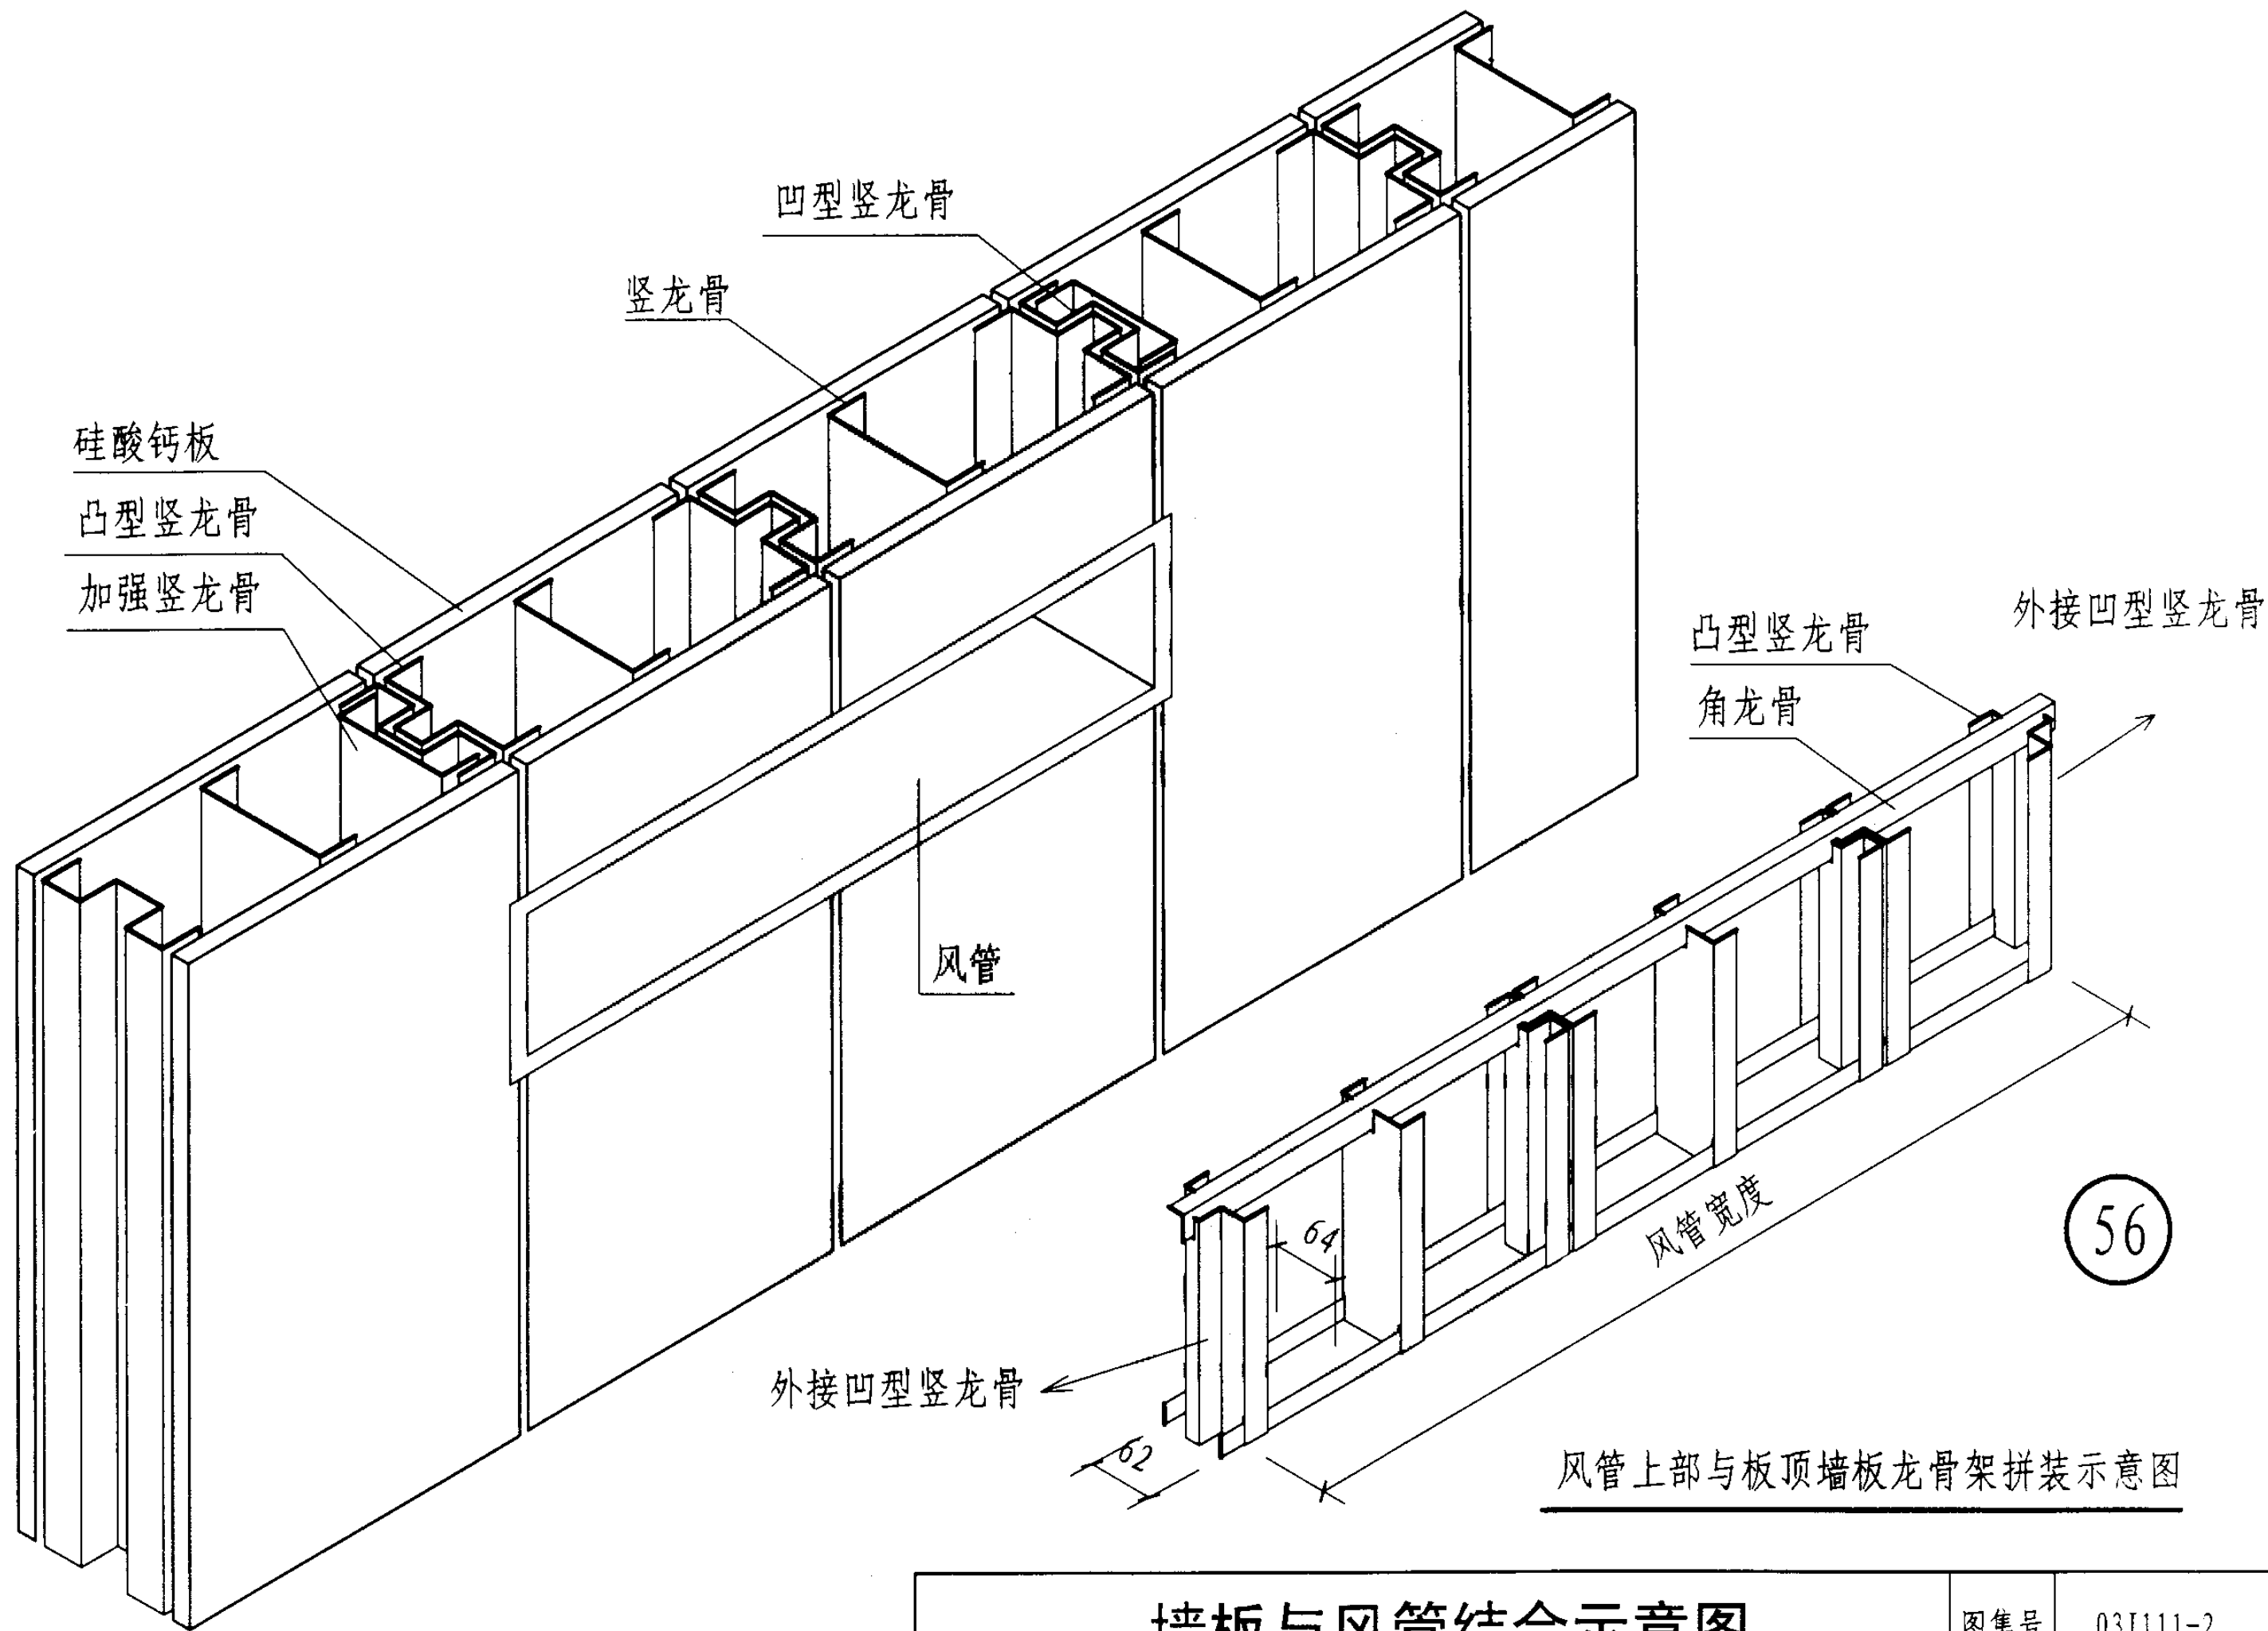

风管上部与板顶墙板龙骨架拼装示意图

墙板与风管结合示意图								图集号	03J111-2
审核	李长发	徐畅	徐畅	设计	熊火生	页	35		

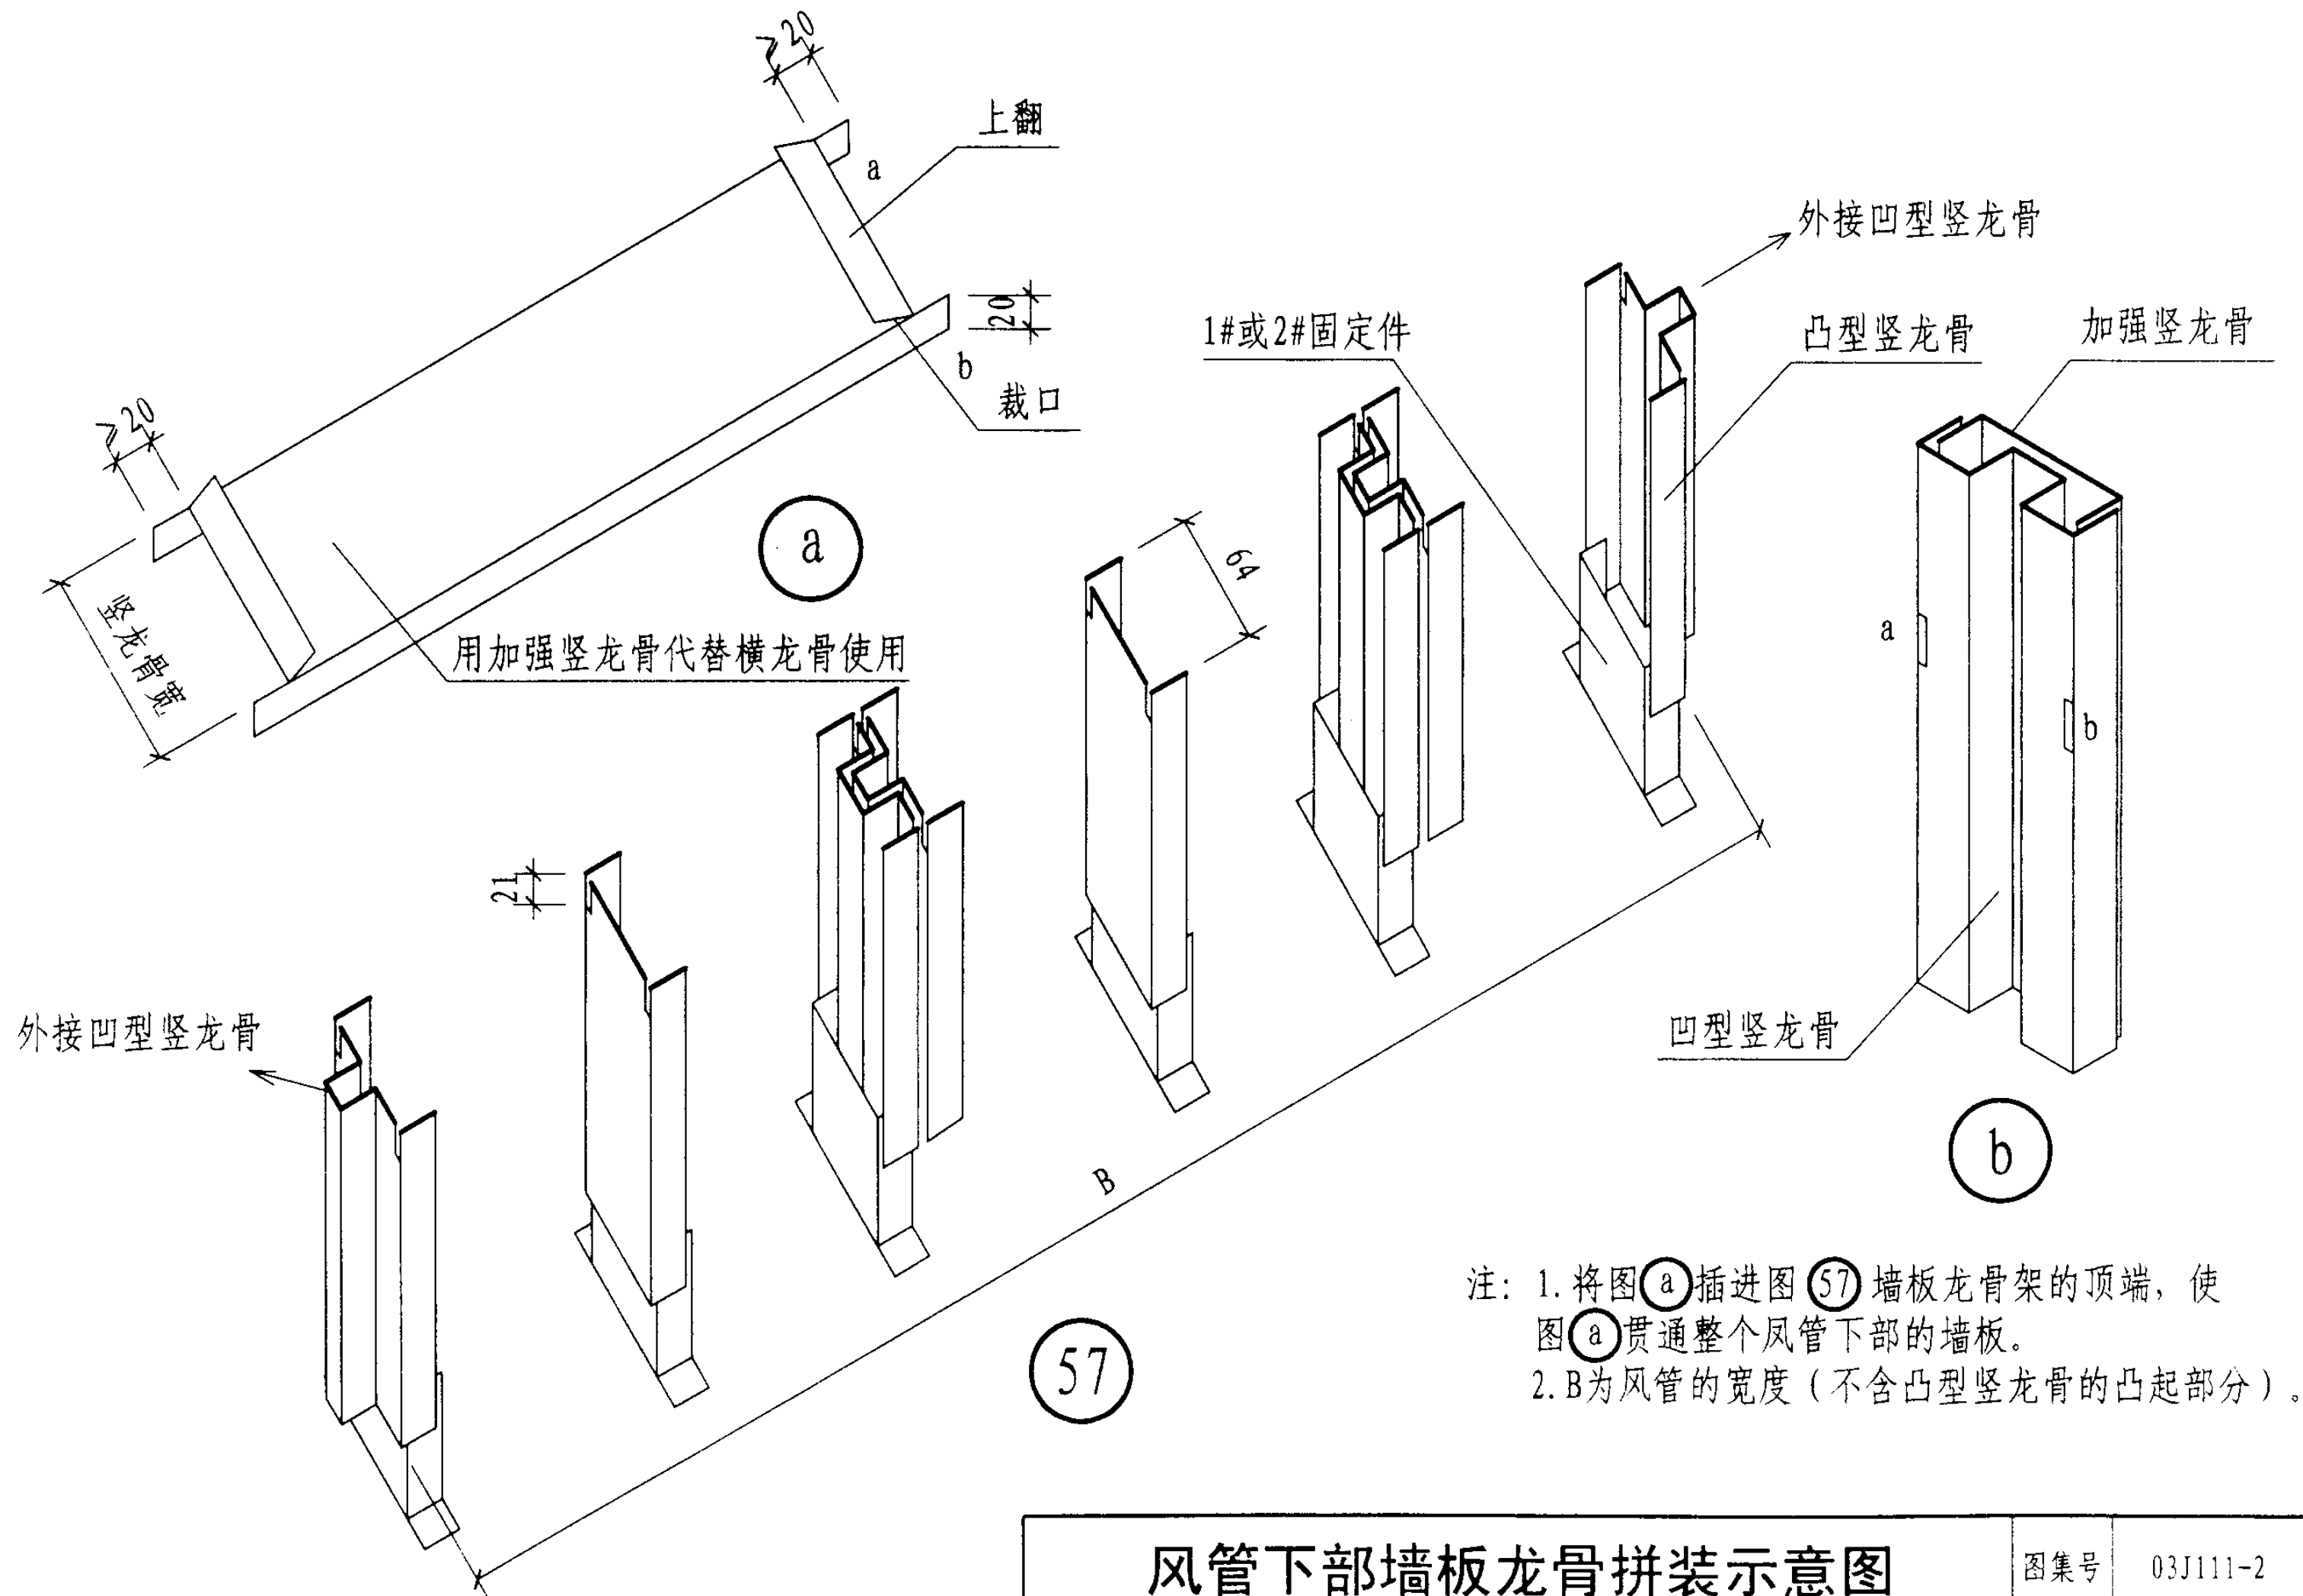


风管下部墙板龙骨拼装示意图


图集号 03J111-2

审核 李长发 徐畅 设计 熊火生


页 36

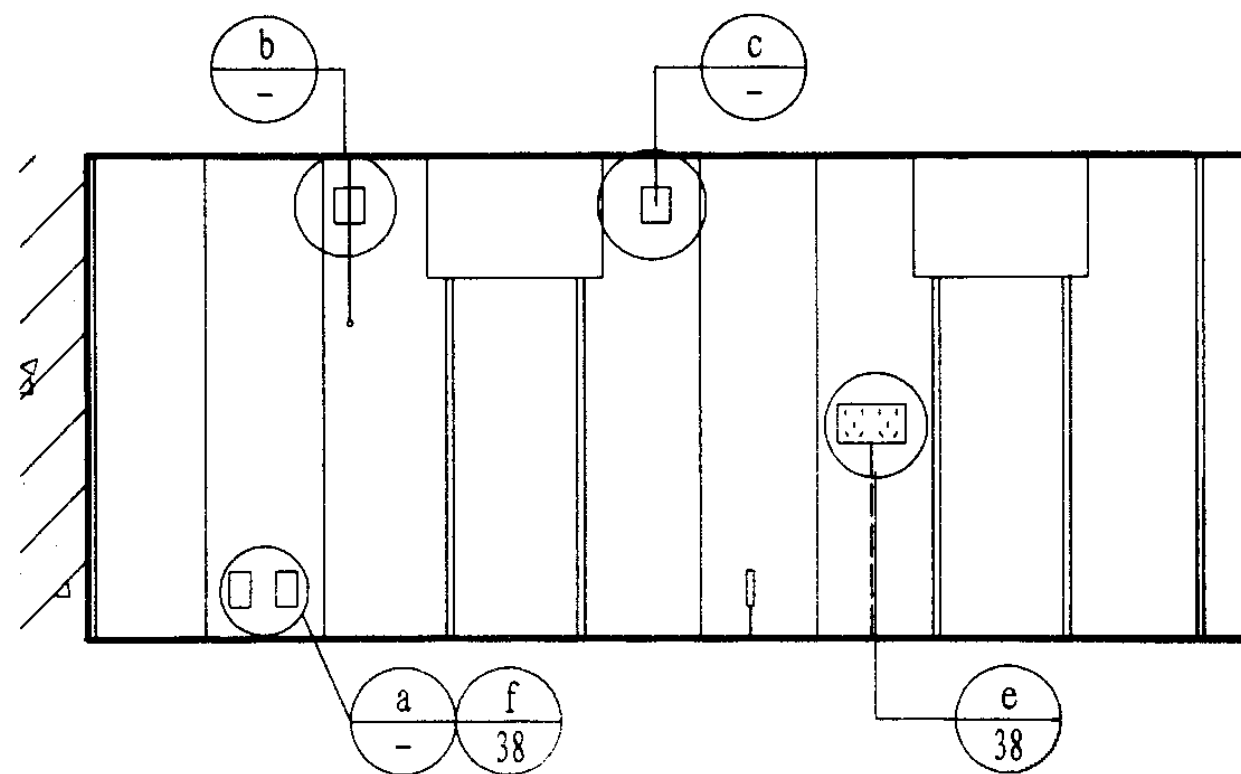


电气开关插座立面

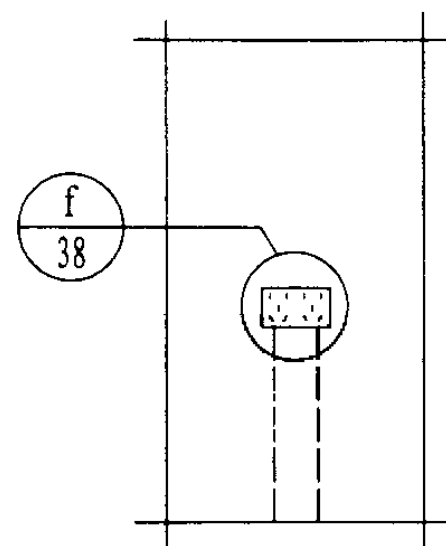


暗线插座立面

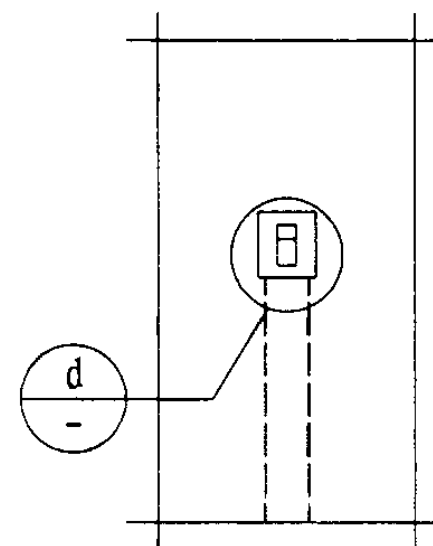


暗线开关立面

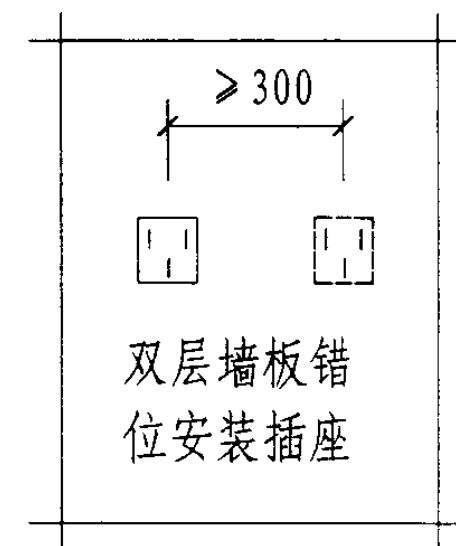


双层墙板插座立面

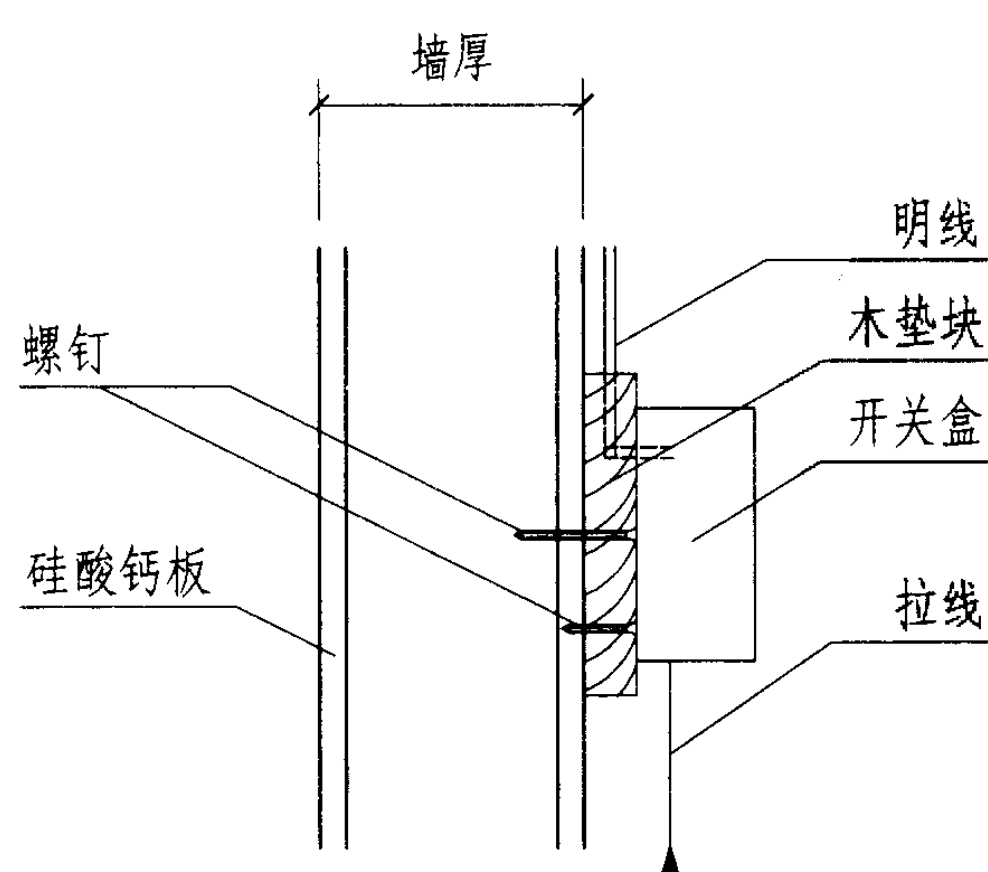

明线拉线开关剖面

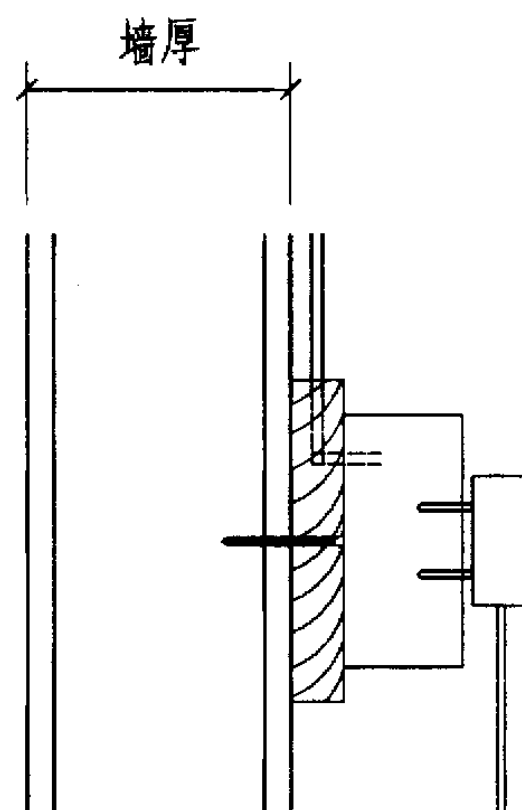

明线插座剖面

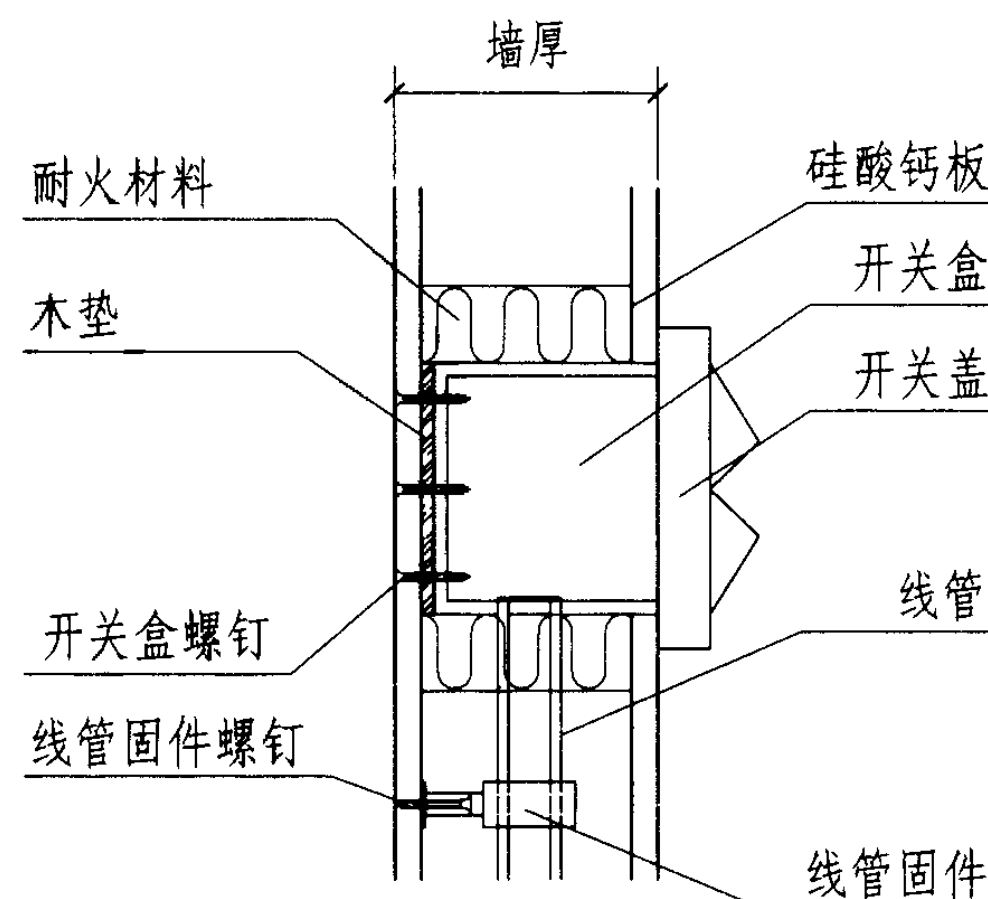

暗线开关剖面

电气开关插座安装节点

图集号 03J111-2


审核 李长发

校对 徐畅


设计 熊火生

页


37

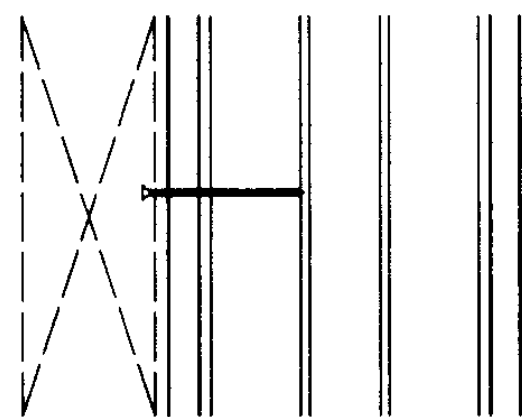


58 螺钉穿透四层吊挂物件示意

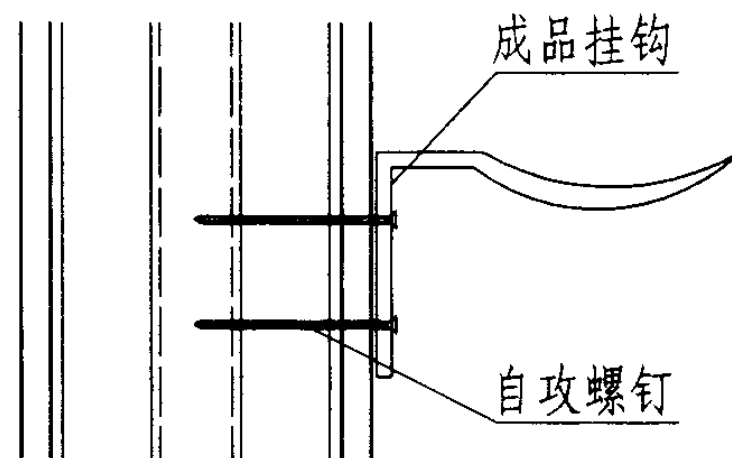

59 螺钉穿透管道托件示意

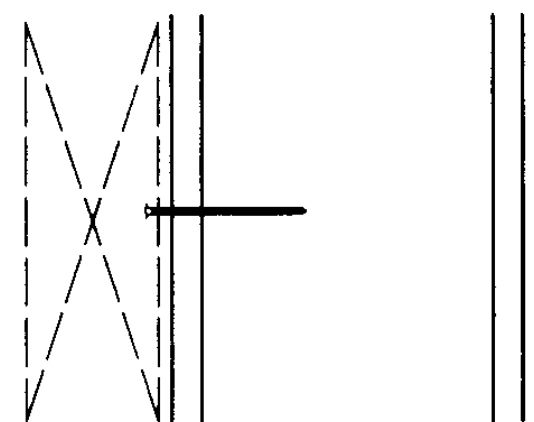


60 螺钉穿硅酸钙板吊挂物件示意

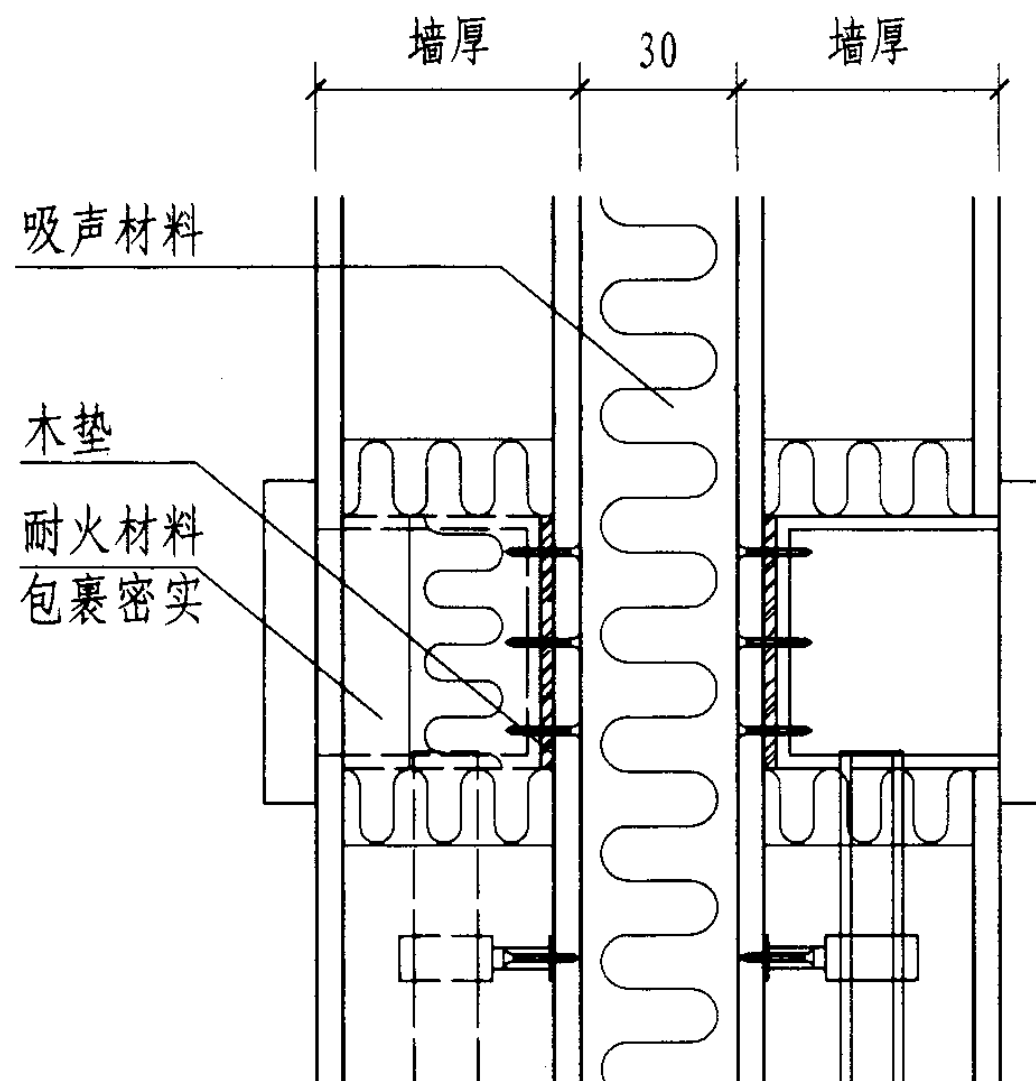


e 暗线插座

f 双层墙插座

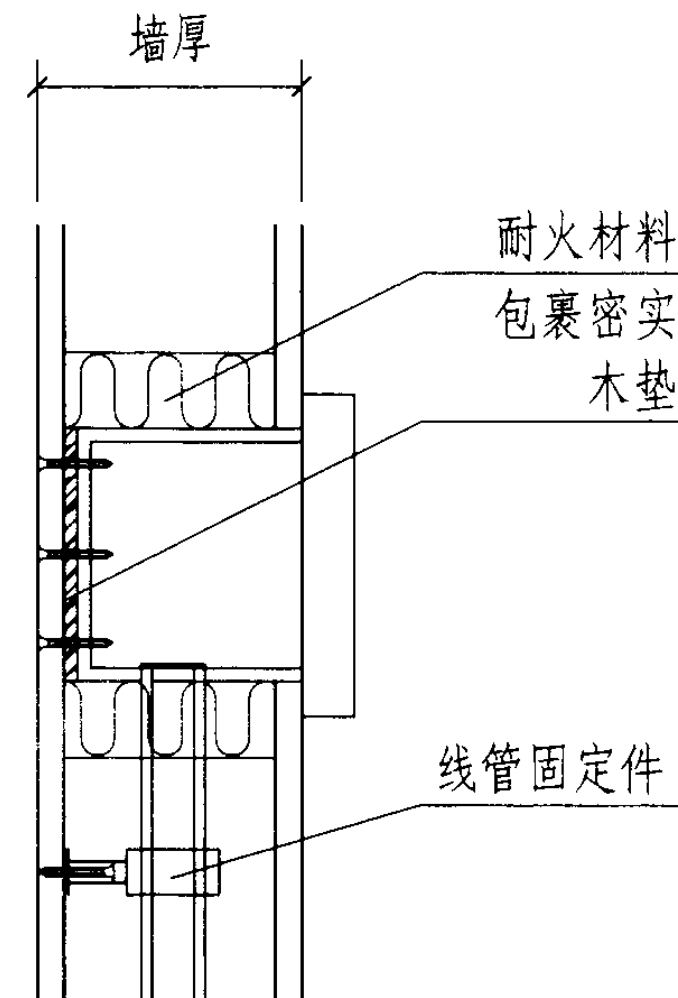







注：吊挂点根据设备轻重及吊挂位置，查阅
“预制轻钢龙骨内隔墙物理力学性能指标表”表1、表2。

设备吊挂件安装节点								图集号	03J111-2
审核	李长发	徐畅	徐畅	设计	熊火生	页	38		

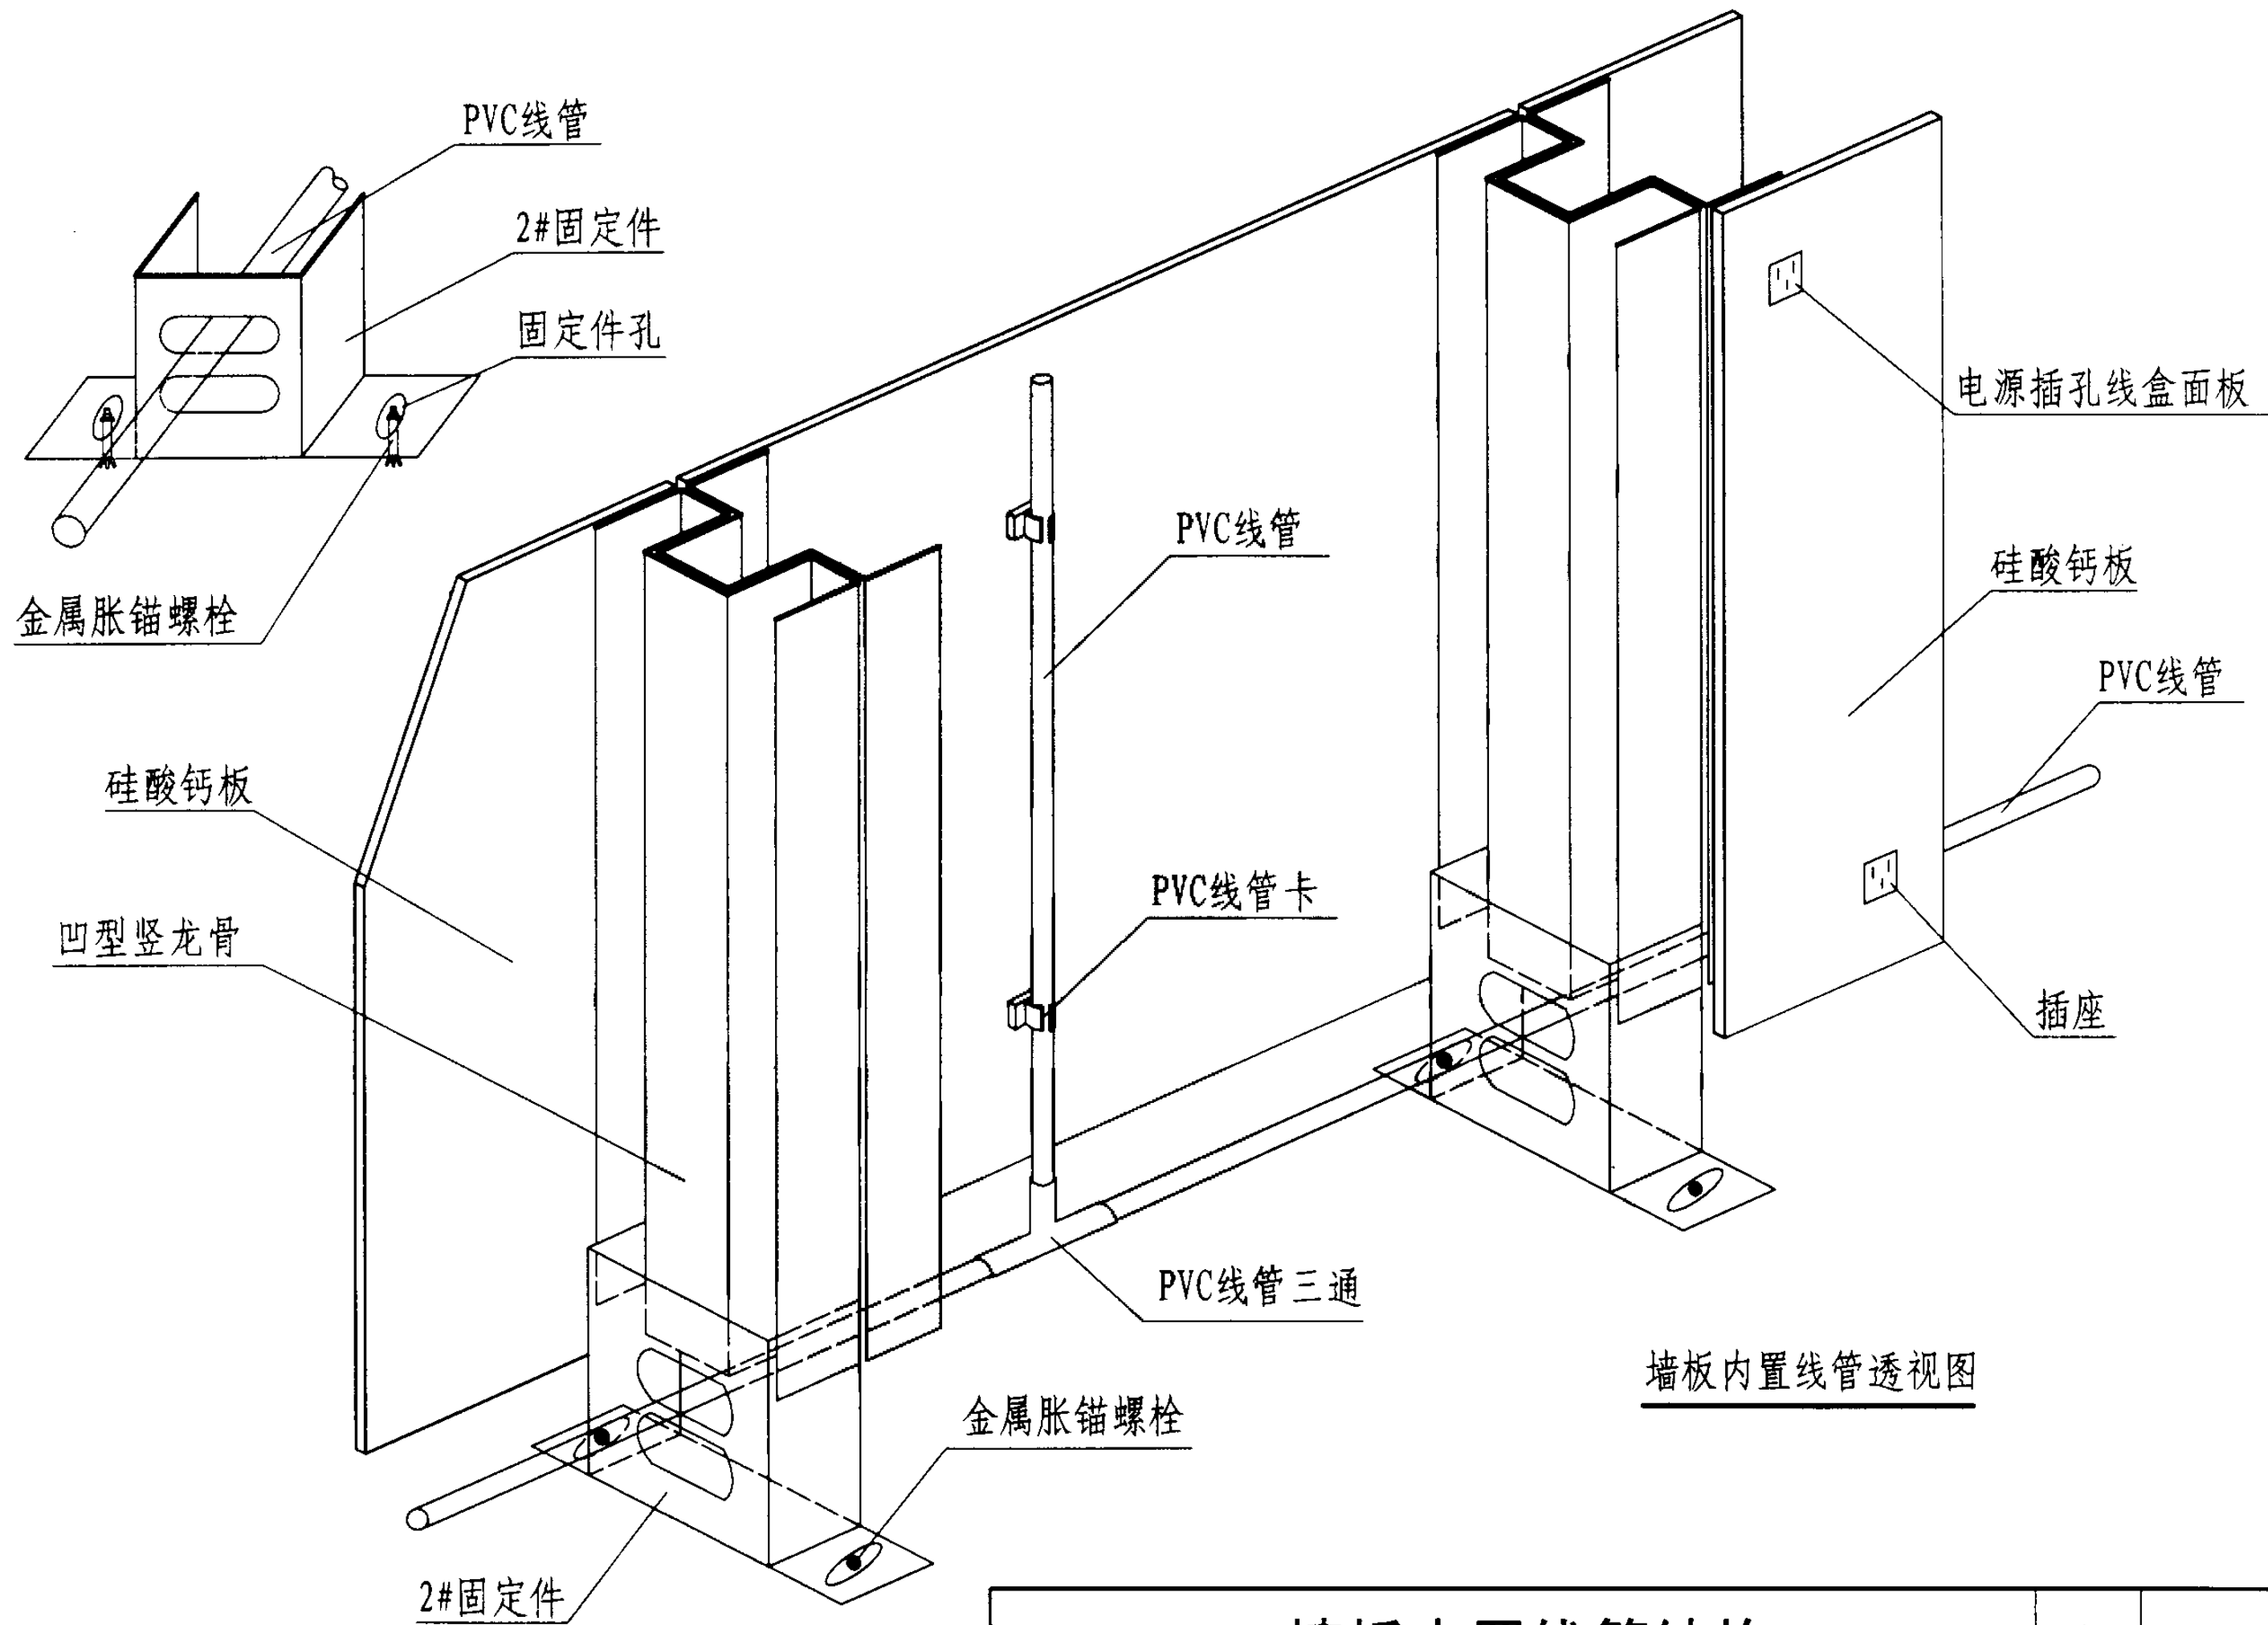


墙板内置线管透视图

墙板内置线管结构								图集号	03J111-2
审核	李长发	徐畅	校对	徐畅	设计	熊火生	页	39	

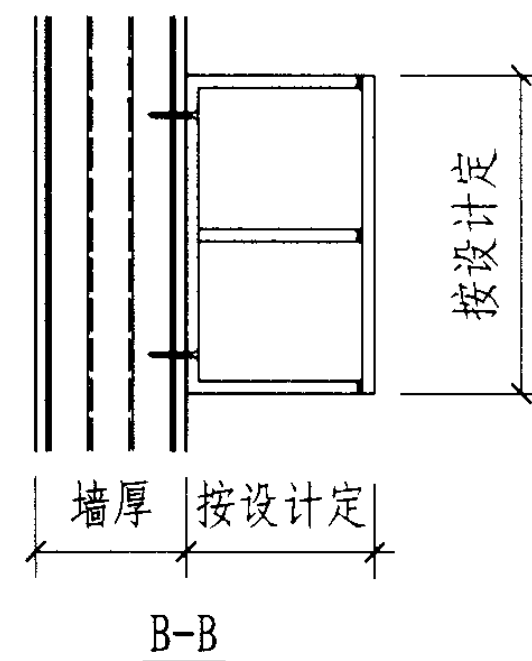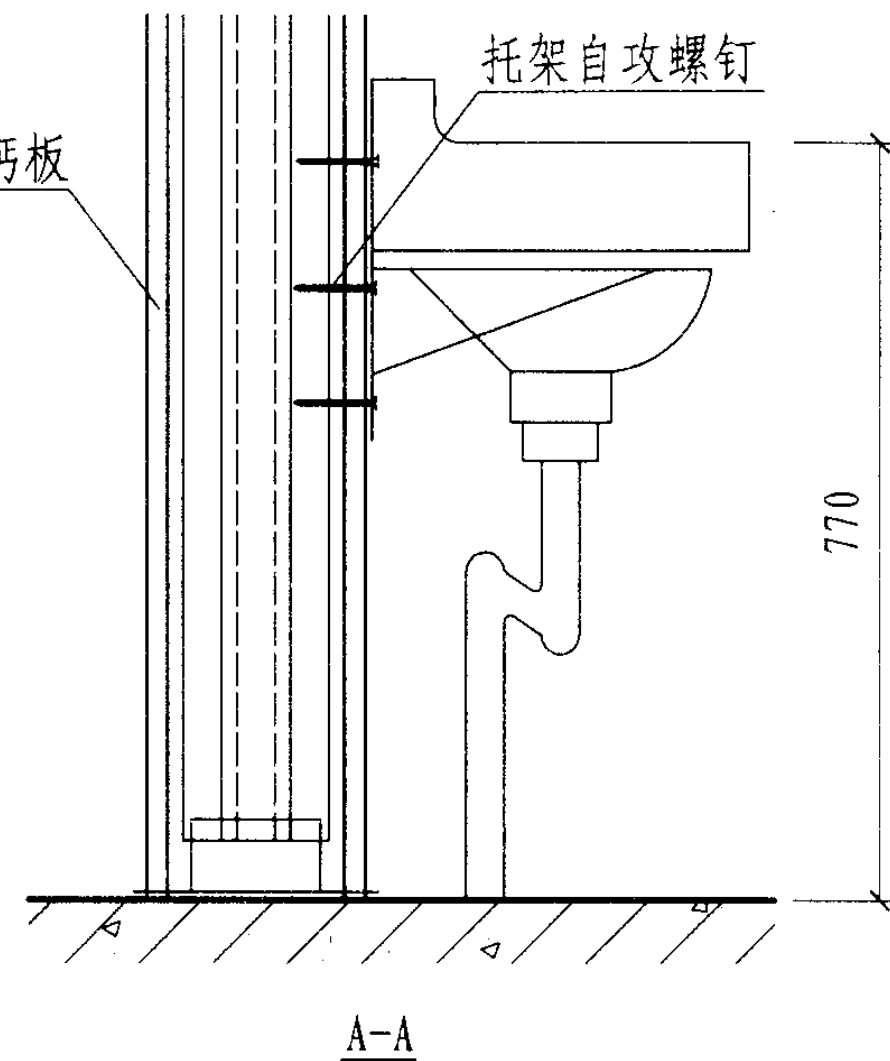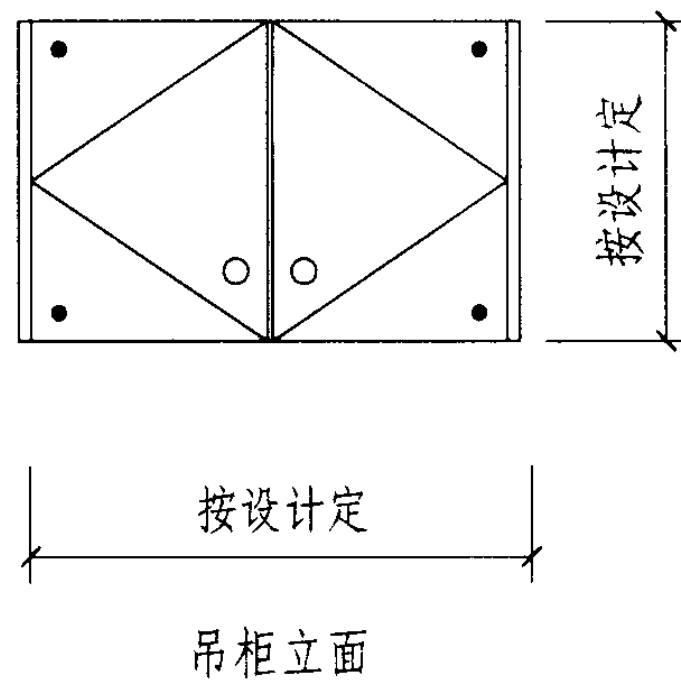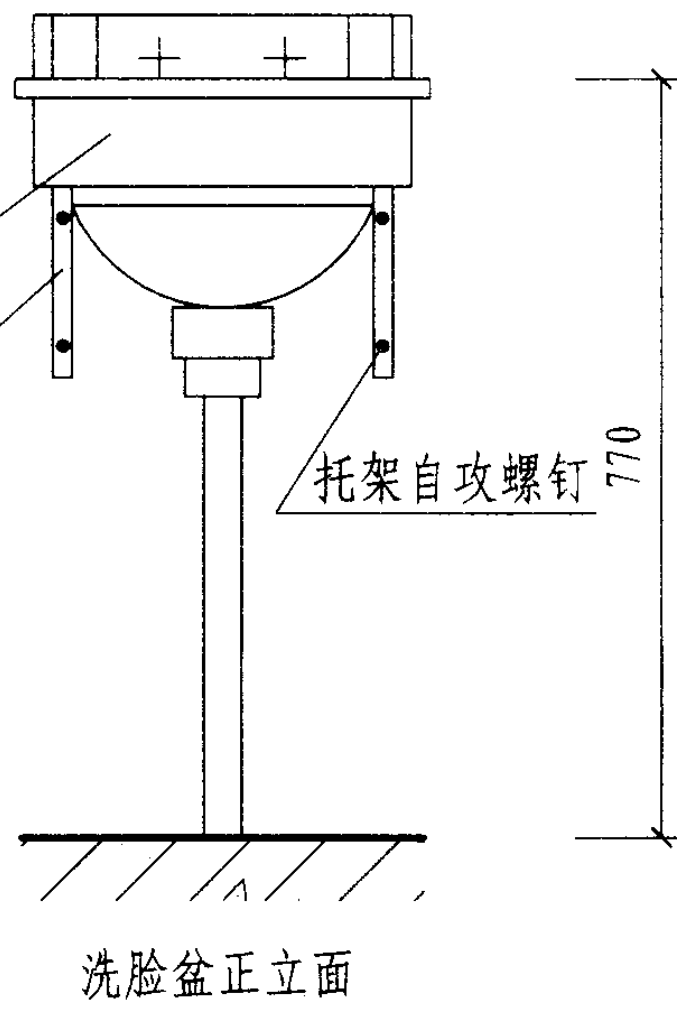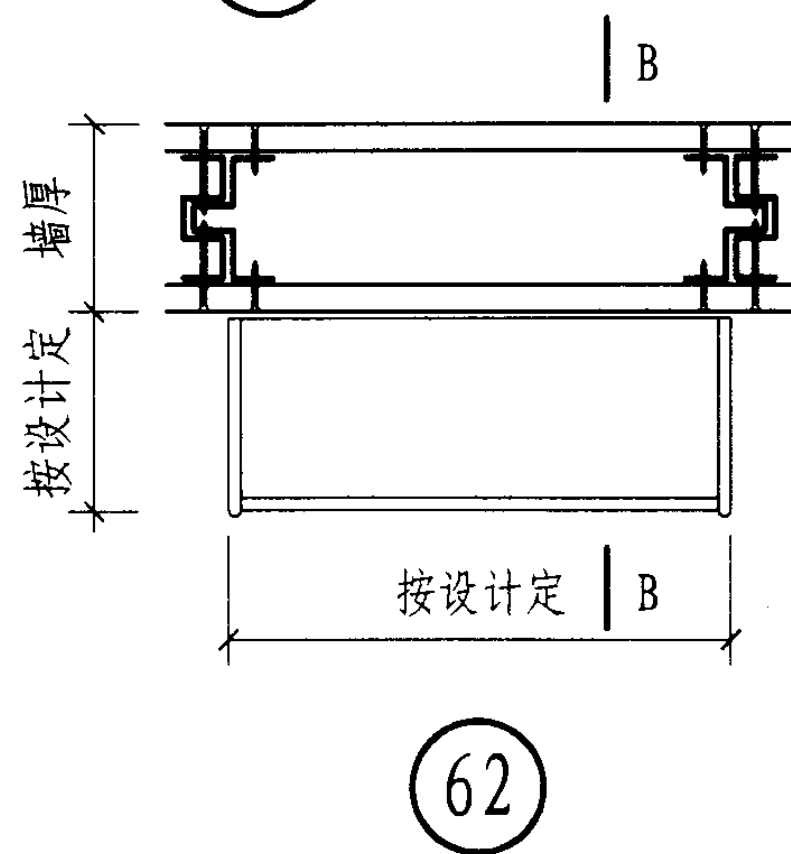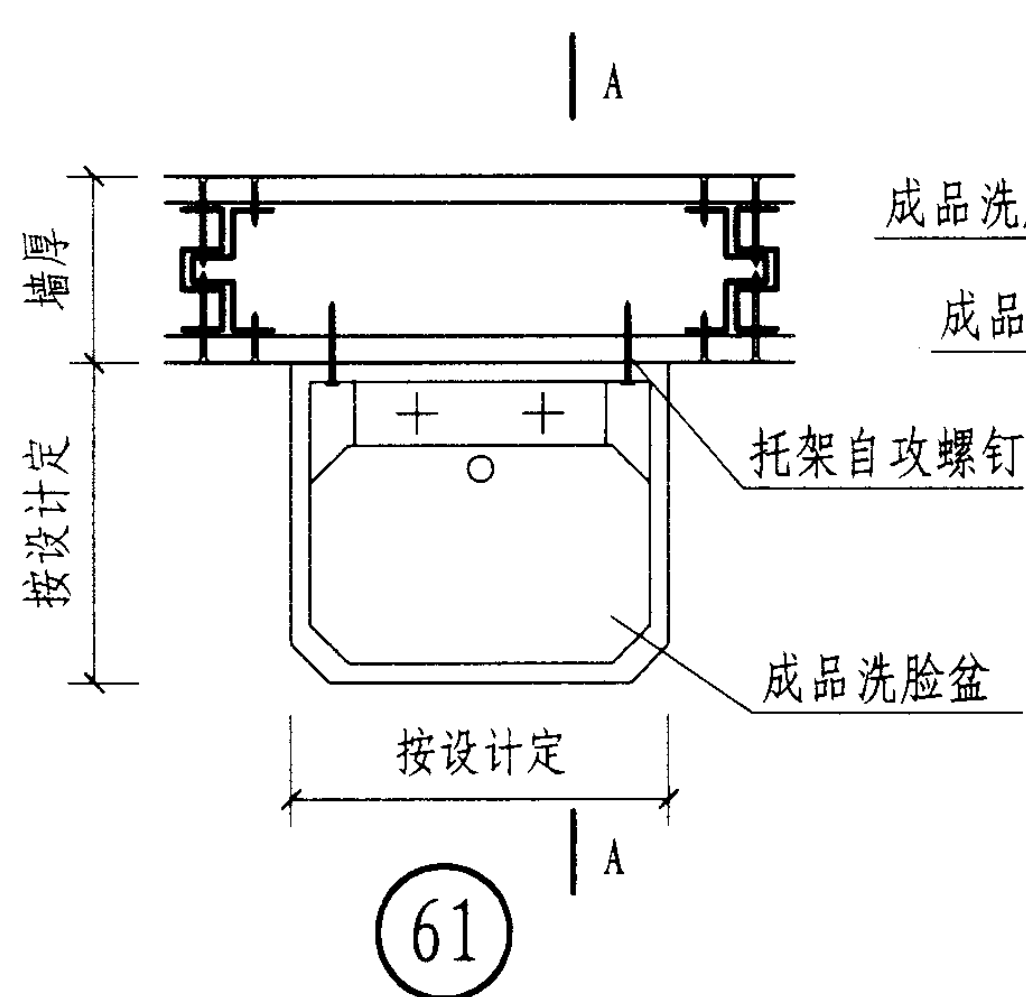

注：吊挂力根据物件轻重及吊挂位置，查阅
“预制轻钢龙骨内隔墙物理性能表”

脸盆、吊柜安装图								图集号	03J111-2
审核	李长发	徐畅	校对	徐畅	设计	熊火生	页	40	

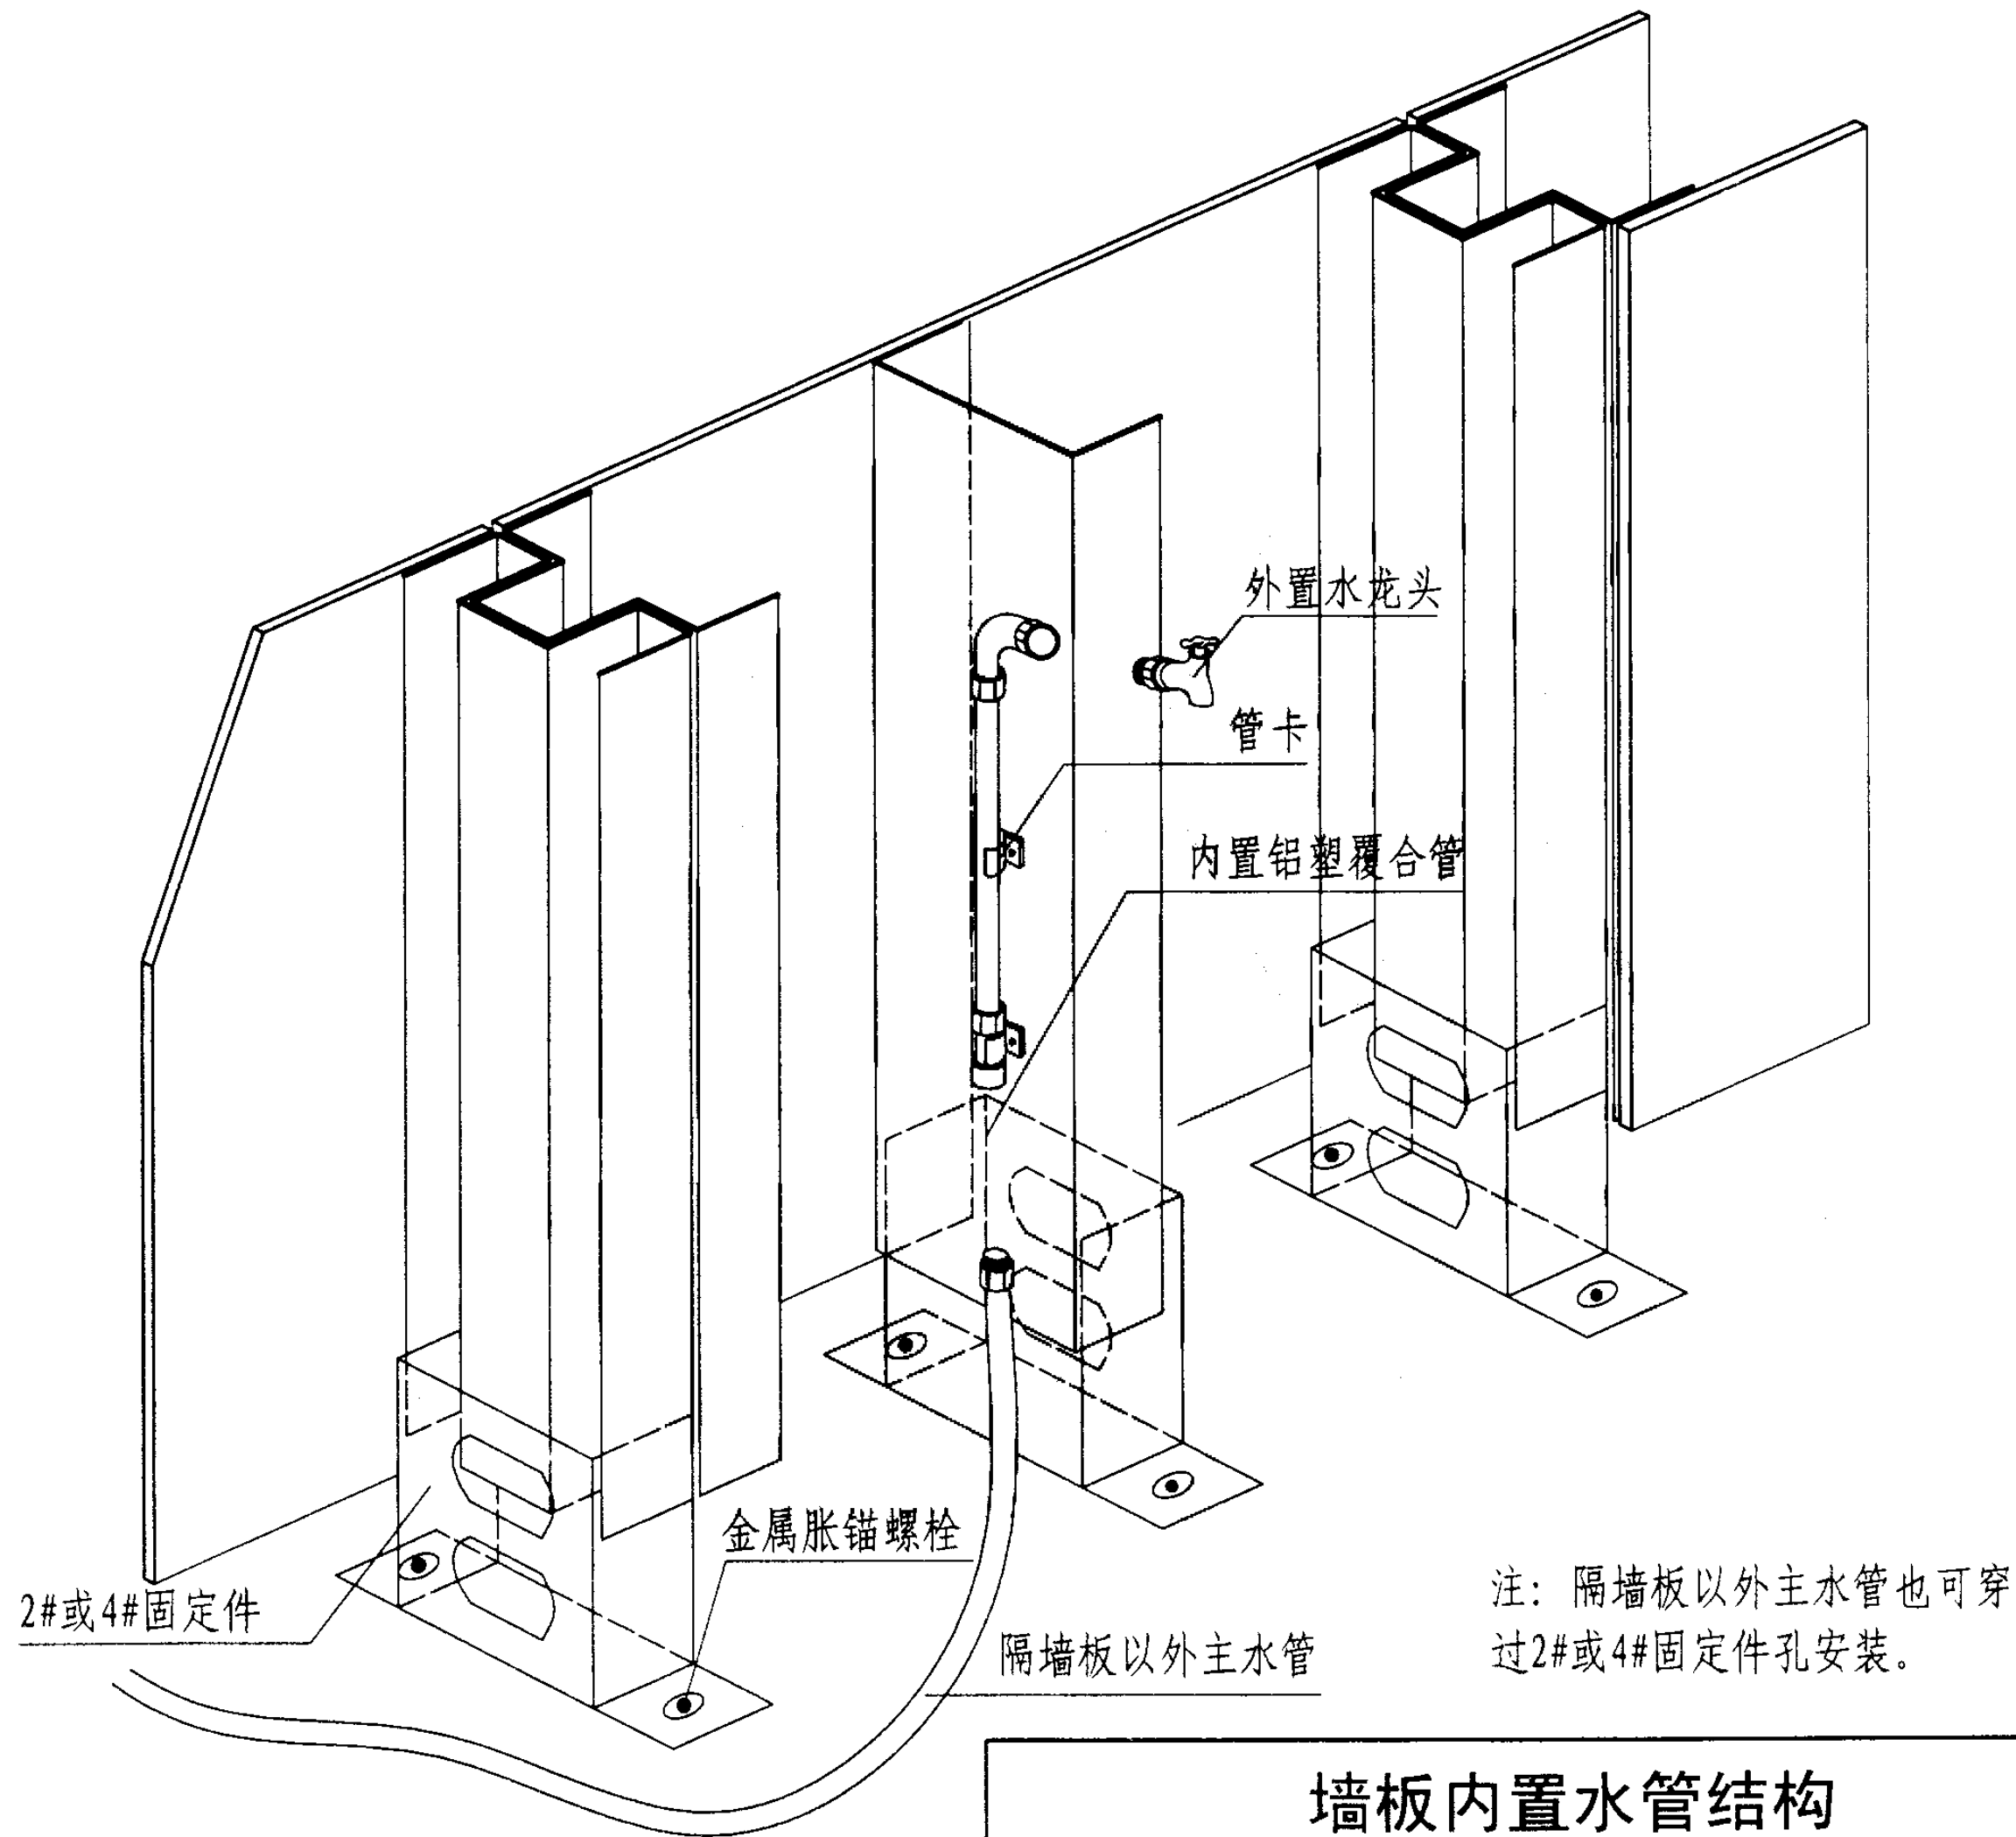

墙板内置水管结构

图集号

03J111-2

审核

李长发

校对

徐畅

设计

熊火生

页

41

附录一

预制轻钢龙骨内隔墙施工要求

1 墙板原材料

1.1 硅酸钙板

应符合JC/T564—2000《纤维增强硅酸钙板》的要求。

1.2 轻钢龙骨

应符合GB/T 11981-2001《建筑用轻钢龙骨》的要求。

1.3 填充材料

应符合GB/T17795—1999《建筑绝热用玻璃棉制品》和JC/T469-92(96)《吸声用玻璃棉制品》的要求。

2 施工程序

2.1 施工用辅助材料见附表1

2.2 作业条件

楼层封顶和主体结构施工验收完毕；与墙板接触部位的主体墙、柱面层应处理后方可进行预制墙板的安装。

2.3 施工步骤

2.3.1 清理结构墙面、地面、楼板底面

2.3.2 弹出墙板顶面相应墨线

2.3.3 标出门窗洞口位置

2.3.4 安装墙板

2.3.5 板缝处理

附表1 施工用辅助材料

辅助材料	用途	材料构成	型号	规格	常规包装
自攻螺钉	固定单层、双硅酸钙板	钢(特殊防锈处理)	-	4×20 4×30	1000枚/盒
钢钉	横穿硅酸钙板、龙骨、固定件		LB30	φ2.5	0.6kg/盒
金属胀锚螺栓	用于主体墙柱和梁板连接	-	-	M6~M10	100颗/盒
嵌缝膏	墙板间缝隙粘结、螺钉端头处理、表面破损修补。	石膏粉、水	PG180	-	20kg/桶
接缝带	与嵌缝膏一同使用，做墙板间、阴角、裂缝修补处理	玻璃纤维	ZD150	-	150m/卷
通长隔声带	做墙板与主体墙柱、角龙骨与楼板顶面隔声处理	橡胶	LB30	-	50m/卷

2.4 施工要点

2.4.1 安装前应检查内隔墙板，凡外形尺寸超出允许偏差或有严重缺陷的不合格产品不得使用。

附录一 预制轻钢龙骨内隔墙施工要求

图集号

03J111-2

审核

李长发

校对

徐畅

设计

熊火生

页

42

2.4.2 沿墨线将角龙骨、加强竖龙骨分别安装到楼板顶面和主体墙柱上；按排版图从一侧开始（包括窗、门顺序）。墙板（包括线管板、水管板）下端置于工字槽内，推墙板套住加强竖龙骨或墙板一侧龙骨，将撬棍塞进工字槽底部并撬起，直到墙板龙骨上端缺口对准角龙骨顶紧，用线锤吊线使墙板呈垂直状态。用两组木楔将工字槽底部塞紧。

2.4.3 将固定件塞进墙板竖龙骨底端并垂直楼地面，用金属胀锚螺栓固定。用钢钉横穿硅酸钙板、竖龙骨及固定件。

2.4.4 用钢钉每隔 600mm 横穿墙板。撤去木楔、工字槽。

2.4.5 用通长 PVC 线管或铝塑复合管穿过固定件孔。硅酸钙板安装在固定件上。将踢脚板安装在硅酸钙板上。

2.4.6 拼接缝处理

- a) 清洁接缝，在接缝口扫一道白乳胶用刮刀将嵌缝膏嵌入两板倒角区；
- b) 第一道腻子凝固后用 8#砂纸打磨，将接缝带对准缝口用白乳胶粘上；用刮刀顺接缝压实，刮去多余的乳胶和气泡；
- c) 干后用嵌缝膏覆在接缝带上。此次比第一道腻子覆盖钉孔宽约 25mm；
- d) 第二道腻子干后，再用嵌缝膏薄薄压上一层，此次比第二道腻子覆盖钉孔宽约 50mm；
- e) 最后一道腻子干后用 220#砂纸打磨。

2.4.7 转角处理

- a) 打磨硅酸钙板切割后不平整的边；
- b) 将嵌缝膏抹在转角线及转角的两面嵌实抹平；
- c) 将接缝带居中扣在转角处，用刀压实。

3 安装质量要求

- 3.1 安装好的内隔墙板面层不得有起皮、掉角、气鼓和出现裂缝，面层应平整。
- 3.2 接缝应填密实，不应出现干缩裂缝。
- 3.3 接缝带应沿板缝居中压贴紧密，不应有皱折翘边、外露现象。
- 3.4 在与门窗框连接的墙板一侧龙骨内置加强竖龙骨。
- 3.5 隔墙安装允许偏差见附表 2

附表 2 隔墙安装允许偏差

序号	项目	允许偏差 (mm)	检查方法及方法
1	轴线偏差	3	钢尺量
2	表面平整	2	2m 靠尺、塞尺检查
3	垂直偏差	2	2m 托线板或经纬仪
4	接缝高差	1~2	直尺、塞尺
5	转角偏差	3	200mm 方尺、特殊角尺、塞尺检查
6	门窗洞中心偏差	3	钢尺量
7	门窗洞口尺寸偏差	4	钢尺量

4 安装工具

安装工具见附表3

附表 3

类别	序号	名称	单位	数量/组	备注
电动工具	1	卷扬机	架	1	整个工地仅需数量
	2	手提切割机	台	1/2 组	用于切割过梁墙板
	3	电锤	把	1/2 组	若射钉枪可代替则不用
	4	手枪钻	把	2/组	每隔 600mm 位置钻眼
	5	空压机	台	1/4 组	限一个楼层供用
	6	风披	个	1/组	
非电动工具	1	扫把	把	1/组	用于时常清除地面墨线
	2	定高杆	根	1	每层数量
	3	卷尺	把	4/组	
	4	吊线锤	个	1/组	检查墙板及固定件呈垂直状态
	5	铅笔	支	4/组	
	6	墨斗	个	1/组	
	7	射枪	把	2/组	一人一把于墙板两面作业

续 附表 3

类别	序号	名称	单位	数量/组	备注
非电动工具	8	斧头	把	1/组	
	9	榔头	把	2/组	
	10	十字螺丝刀	把	4/组	
	11	撬棍或木杠	根	4/组	长度以 1200mm 为好
	12	工字槽	根	1/组	墙板底端置于槽内位移,木楔楔至槽底顶起楼板
	13	木楔	个	6/组	薄厚不一、杂木木质为好
	14	方木	根	4	用于塞进墙板内,切割时起靠尺作用
	15	工作台	个	1~2/层	装有云石园盘锯,工作台用于切割墙板
	16	梯子或凳子	个	2/组	

注: 墙板安装宜 4 人一组, 所需工具数量系指组、每层楼或整个工地。

附录二

预制轻钢龙骨内隔墙墙体选用表

1 墙体选用

预制墙体（专利号 ZL 99 2 42513.1、ZL 02 2 16936.9、ZL 02 2 16937.7）选用表见附表4。


1.1 墙板符合 GB50045-95《高层民用建筑设计防火规范》（2001版）的要求。

1.2 墙板可重复使用。








1.3 表中墙板以普通板为例。

1.4 建筑工程中所需板型由生产厂家按设计要求配备。

1.5 附表4中数据由南昌中环新型墙体装璜材料厂提供。

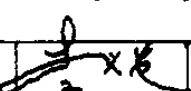附录二 墙体选用表								图集号	03J111-2
审核	李长发		校对	徐畅		设计	熊火生	页	45

附表 4

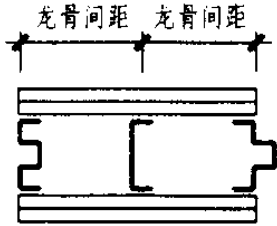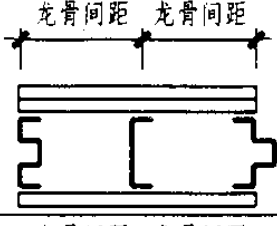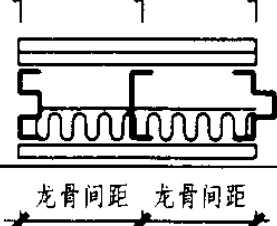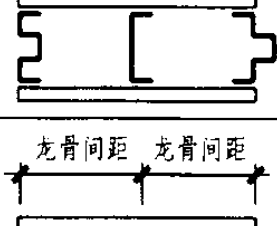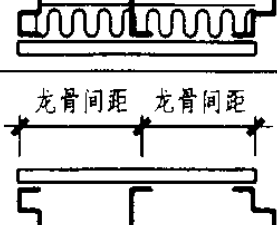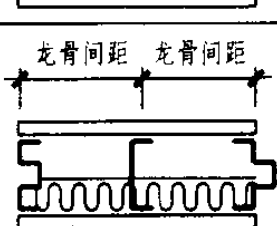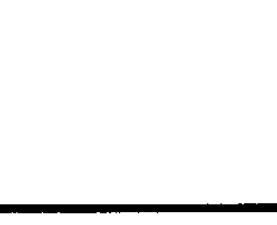产品 代号	图示	墙体尺寸 (mm)					墙体自重 (计算值)		墙体最大高度 m (计算值)			
		面板厚	面板排板方式	层数	龙骨宽度	墙厚	kN/m ²	kg/m ²	龙骨间距 (mm)			
									200	300	400	600
LB01		6	6+6+6+6	2+2	64	88	0.26	27	-	-	3.24	2.84
LB02		6, 8	6+6+8	2+1	64	84	0.23	23	-	-	3.24	2.84
LB03		6, 8	6+6+8	2+1	64	84	0.24	24	-	-	3.24	2.84
LB04		8	8+8	1+1	64	80	0.19	19	-	-	3.24	2.84
LB05		8	8+8	1+1	64	80	0.20	20	-	-	3.24	2.84
LB06		10	10+10	1+1	64	84	0.23	23	-	-	3.24	2.84
LB07		10	10+10	1+1	64	84	0.24	24	-	-	3.24	2.84

附录二 墙体选用表

图集号

03J111-2

审核

李长发

校对

徐畅






设计

熊火生

页

46

续 附表 4

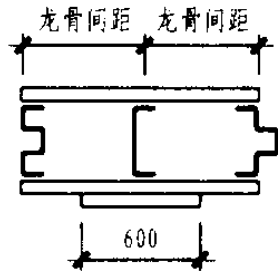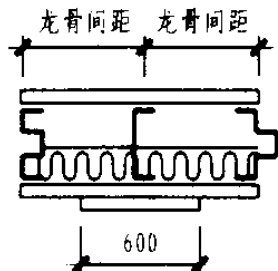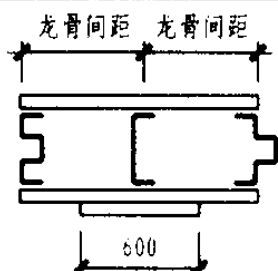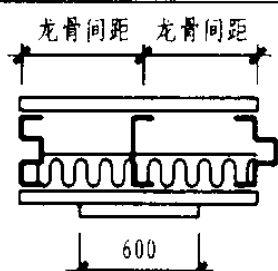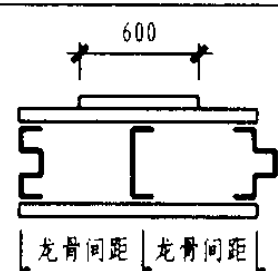产品 代号	图示	墙体尺寸 (mm)					墙体自重 (计算值)		墙体最大高度 m (计算值)			
		面板厚	面板排板方式	层数	龙骨宽度	墙厚	kN/m ²	kg/m ²	龙骨间距 (mm)			
									200	300	400	600
LB08		8	8+8+8	1+2	64	88	0.26	27	-	-	3.24	2.84
LB09		8	8+8+8	1+2	64	88	0.27	28	-	-	3.24	2.84
LB10		8, 6	8+8+6	1+2	64	86	0.25	25	-	-	3.24	2.84
LB11		8, 6	8+8+6	1+2	64	86	0.25	26	-	-	3.24	2.84
LB12		8, 10	8+8+10	2+1	64	90	0.28	29	-	-	3.24	2.84

附录二 墙体选用表

图集号

03J111-2

审核

李长发

校对

徐畅






设计

熊火生

页

47

续 附表 4

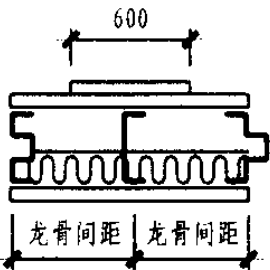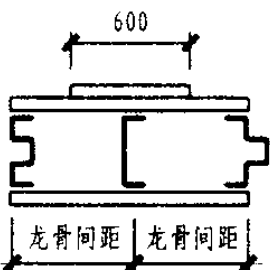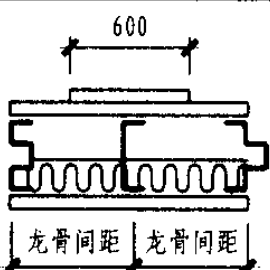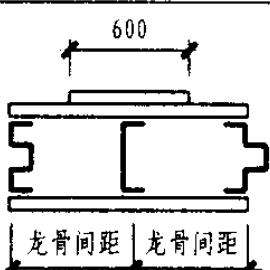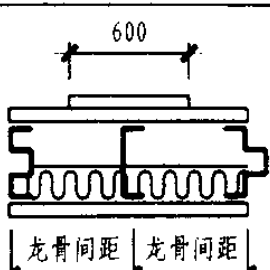产品 代号	图示	墙体尺寸 (mm)					墙体自重 (计算值)		墙体最大高度 m (计算值)			
		面板厚	面板排板方式	层数	龙骨宽度	墙厚	kN/m ²	kg/m ²	龙骨间距 (mm)			
									200	300	400	600
LB13		8, 10	8+8+10	2+1	64	90	0.29	30	-	-	3.24	2.84
LB14		10	10+10+10	2+1	64	94	0.32	33	-	-	3.24	2.84
LB15		10	10+10+10	2+1	64	94	0.33	34	-	-	3.24	2.84
LB16		8, 10	8+10+10	2+1	64	92	0.30	31	-	-	3.24	2.84
LB17		8, 10	8+10+10	2+1	64	92	0.31	32	-	-	3.24	2.84

附录二 墙体选用表

图集号

03J111-2

审核

李长发

校对

徐畅






设计

熊火生

页

48

续附表4

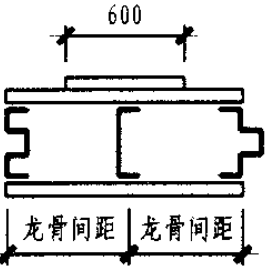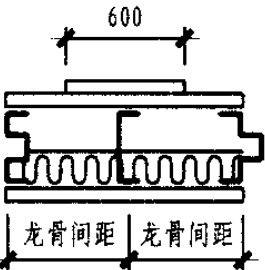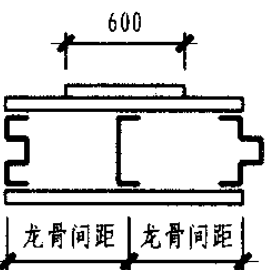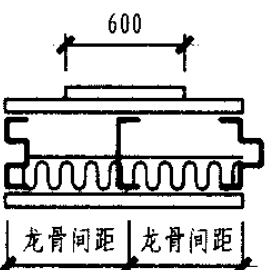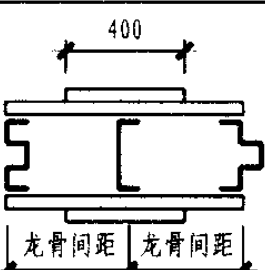产品 代号	图示	墙体尺寸 (mm)					墙体自重 (计算值)		墙体最大高度 m (计算值)			
		面板厚	面板排板方式	层数	龙骨宽度	墙厚	kN/m ²	kg/m ²	龙骨间距 (mm)			
									200	300	400	600
LB18		10, 8	10+10+8	2+1	64	92	0.30	31	-	-	3.24	2.84
LB19		10, 8	10+10+8	2+1	64	92	0.31	32	-	-	3.24	2.84
LB20		8, 10	8+10+8	2+1	64	90	0.28	29	-	-	3.24	2.84
LB21		8, 10	8+10+8	2+1	64	90	0.29	30	-	-	3.24	2.84
LB22		8	8+8+8+8	2+2	64	96	0.35	36	3.64	-	3.24	-

附录二 墙体选用表

图集号

03J111-2

审核

李长发

校对

徐畅






设计

熊火生

页

49

续 附表 4

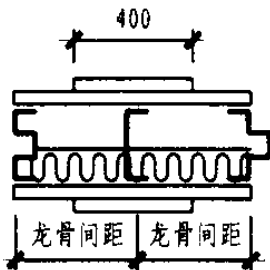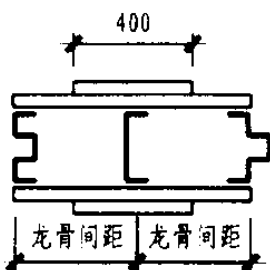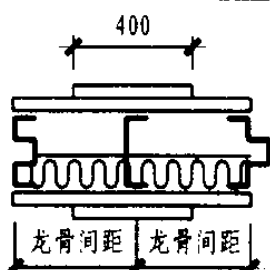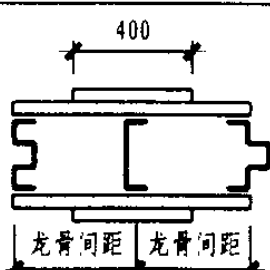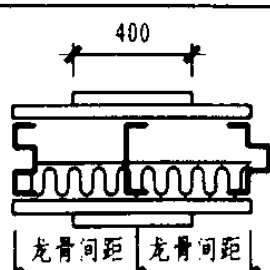产品 代号	图示	墙体尺寸 (mm)					墙体自重 (计算值)		墙体最大高度 m (计算值)			
		面板厚	面板排板方式	层数	龙骨宽度	墙厚	kN/m ²	kg/m ²	龙骨间距 (mm)			
									200	300	400	600
LB23		8	8+8+8+8	2+2	64	96	0.36	37	3.64	-	3.24	-
LB24		8, 10	8+8+10+10	2+2	64	100	0.39	40	3.64	-	3.24	-
LB25		8, 10	8+8+10+10	2+2	64	100	0.40	41	3.64	-	3.24	-
LB26		8, 10	8+10+8+10	2+2	64	100	0.39	40	3.64	-	3.24	-
LB27		8, 10	8+10+10+8	2+2	64	100	0.40	41	3.64	-	3.24	-

附录二 墙体选用表

图集号

03J111-2

审核

李长发

校对

徐畅







设计

熊火生

页

50

续 附表 4

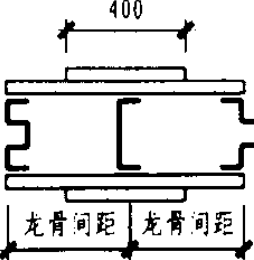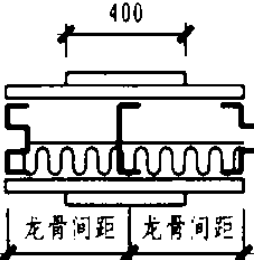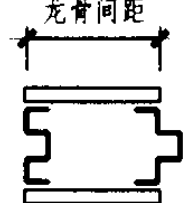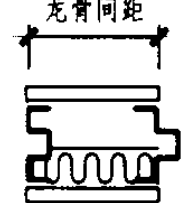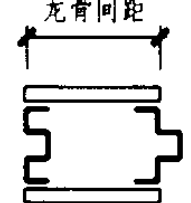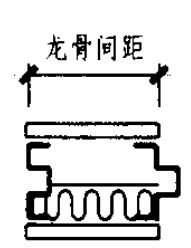产品 代号	图示	墙体尺寸 (mm)					墙体自重 (计算值)		墙体最大高度 m (计算值)			
		面板厚	面板排板方式	层数	龙骨宽度	墙厚	kN/m ²	kg/m ²	龙骨间距 (mm)			
									200	300	400	600
LB28		10	10+10+10+10	2+2	64	104	0.43	44	3.64	-	3.24	-
LB29		10	10+10+10+10	2+2	64	104	0.44	45	3.64	-	3.24	-
LB30		8	8+8	1+1	84	100	0.21	21	-	5.28	-	4.48
LB31		8	8+8	1+1	84	100	0.22	22	-	5.28	-	4.48
LB32		10	10+10	1+1	84	104	0.25	25	-	5.28	-	4.48
LB33		10	10+10	1+1	84	104	0.26	27	-	5.28	-	4.48

附录二 墙体选用表

图集号

03J111-2

审核

李长发

校对

徐畅







设计

熊火生

页

51

附表 4 (续)

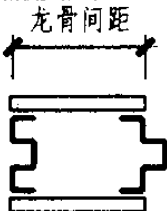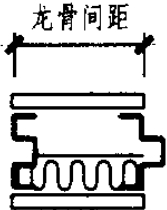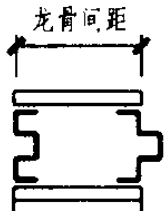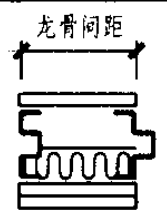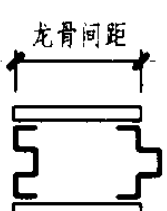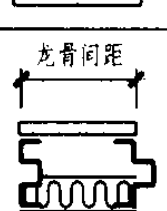产品 代号	图示	墙体尺寸 (mm)					墙体自重 (计算值)		墙体最大高度 m (计算值)			
		面板厚	面板排板方式	层数	龙骨宽度	墙厚	kN/m ²	kg/m ²	龙骨间距 (mm)			
									200	300	400	600
LB34		8, 10	8+10	1+1	84	102	0.24	24	—	5.28	—	4.48
LB35		8, 10	8+10	1+1	84	102	0.25	25	—	5.28	—	4.48
LB36		8, 6	8+6+6	1+2	84	104	0.25	25	—	5.28	—	4.48
LB37		8, 6	8+6+6	1+2	84	104	0.26	27	—	5.28	—	4.48
LB38		10, 6	10+6+6	1+2	84	106	0.27	28	—	5.28	—	4.48
LB39		10, 6	10+6+6	1+2	84	106	0.28	29	—	5.28	—	4.48
LB40		6	6+6+6+6	2+2	84	108	0.29	30	—	5.28	—	4.48

附录二 墙体选用表

图集号

03J111-2

审核

李长发

校对

徐畅






设计

熊火生

页

52

续 附表 4

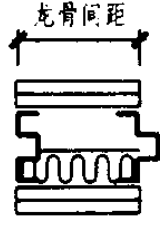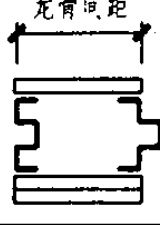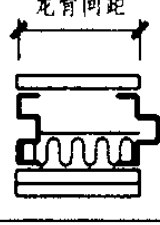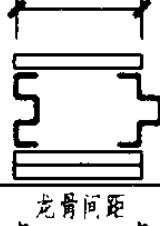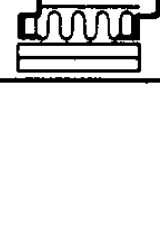产品 代号	图示	墙体尺寸 (mm)					墙体自重 (计算值)		墙体最大高度 m (计算值)			
		面板厚	面板排板方式	层数	龙骨宽度	墙厚	kN/m ²	kg/m ²	龙骨间距 (mm)			
									200	300	400	600
LB41		6	6+6+6+6	2+2	84	108	0.30	31	-	5.28	-	4.48
LB42		8, 10, 6	8+10+6	1+2	84	108	0.29	30	-	5.28	-	4.48
LB43		8, 10, 6	8+10+6	1+2	84	108	0.30	31	-	5.28	-	4.48
LB44		8, 10	8+10+10	1+2	84	112	0.33	34	-	5.28	-	4.48
LB45		8, 10	8+10+10	1+2	84	112	0.34	35	-	5.28	-	4.48
LB46		8, 10, 6	8+10+6	1+2	84	108	0.29	30	-	5.28	-	4.48
LB47		10, 6, 8	10+6+8	1+2	84	108	0.30	31	-	5.28	-	4.48

附录二 墙体选用表

图集号

03J111-2

审核

李长发

校对

徐畅








设计

熊火生






页

53




续 附表 4

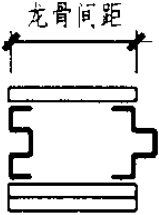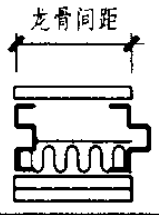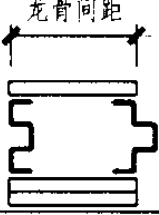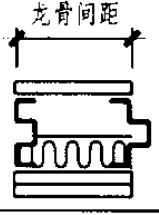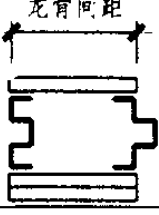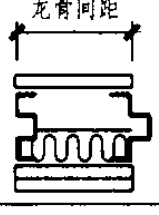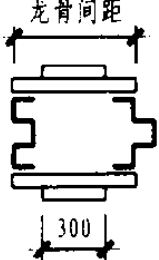产品 代号	图示	墙体尺寸 (mm)					墙体自重 (计算值)		墙体最大高度 m (计算值)			
		面板厚	面板排板方式	层数	龙骨宽度	墙厚	kN/m ²	kg/m ²	龙骨间距 (mm)			
									200	300	400	600
LB48		10, 8	10+8+8	1+2	84	110	0.30	31	-	5.28	-	4.48
LB49		10, 8	10+8+8	1+2	84	110	0.32	33	-	5.28	-	4.48
LB50		8	8+8+8	1+2	84	108	0.28	29	-	5.28	-	4.48
LB51		8	8+8+8	1+2	84	108	0.30	31	-	5.28	-	4.48
LB52		10	10+10+10	1+2	84	114	0.34	35	-	5.28	-	4.48
LB53		10	10+10+10	1+2	84	114	0.36	37	-	5.28	-	4.48
LB54		8, 10	8+10+10+8	2+2	84	120	0.40	41	-	5.28	-	4.48

续 附表 4

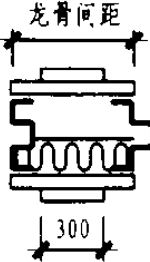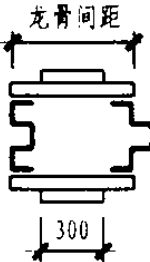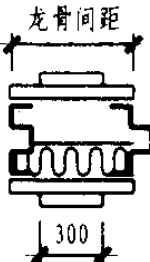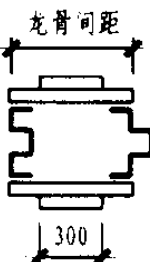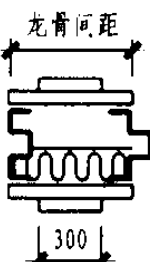产品 代号	图示	墙体尺寸 (mm)					墙体自重 (计算值)		墙体最大高度 m (计算值)			
		面板厚	面板排板方式	层数	龙骨宽度	墙厚	kN/m ²	kg/m ²	龙骨间距 (mm)			
									200	300	400	600
LB55		8, 10	8+10+10+8	2+2	84	120	0.41	42	-	5.28	-	4.48
LB56		8	8+8+8+8	2+2	84	116	0.36	37	-	5.28	-	4.48
LB57		8	8+8+8+8	2+2	84	116	0.37	38	-	5.28	-	4.48
LB58		10	10+10+10+10	2+2	84	124	0.44	45	-	5.28	-	4.48
LB59		10	10+10+10+10	2+2	84	124	0.45	46	-	5.28	-	4.48

续 附表 4

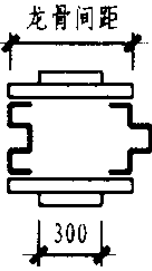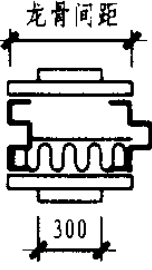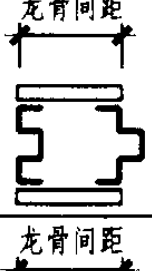产品 代号	图示	墙体尺寸 (mm)					墙体自重 (计算值)		墙体最大高度 m (计算值)			
		面板厚	面板排板方式	层数	龙骨宽度	墙厚	kN/m ²	kg/m ²	龙骨间距 (mm)			
									200	300	400	600
LB60		8, 10	8+8+10+10	2+2	84	120	0.40	41	-	5.28	-	4.48
LB61		8, 10	8+8+10+10	2+2	84	120	0.41	42	-	5.28	-	4.48
LB62		8	8+8	1+1	134	150	0.26	27	6.9	-	6.1	-
LB63		8	8+8	1+1	134	150	0.27	28	6.9	-	6.1	-
LB64		10	10+10	1+1	134	154	0.30	31	6.9	-	6.1	-
LB65		10	10+10	1+1	134	154	0.31	32	6.9	-	6.1	-

附录二 墙体选用表

图集号

03J111-2

审核

李长发

校对

徐畅








设计

熊火生

页




56

续 附表 4

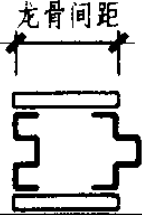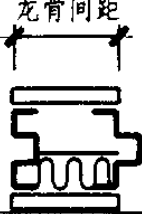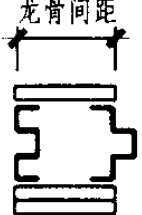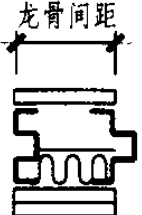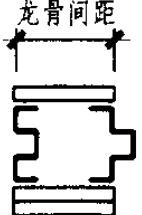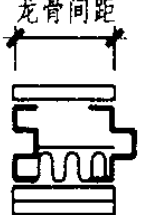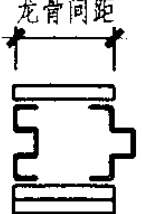产品 代号	图示	墙体尺寸 (mm)					墙体自重 (计算值)		墙体最大高度 m (计算值)			
		面板厚	面板排板方式	层数	龙骨宽度	墙厚	kN/m ²	kg/m ²	龙骨间距 (mm)			
									200	300	400	600
LB66		10, 8	10+8	1+1	134	152	0.28	29	6.9	-	6.1	-
LB67		10, 8	10+8	1+1	134	152	0.29	30	6.9	-	6.1	-
LB68		8	8+8+8	1+2	134	158	0.34	35	6.9	-	6.1	-
LB69		8	8+8+8	1+2	134	158	0.35	36	6.9	-	6.1	-
LB70		10	10+10+10	1+2	134	164	0.40	41	6.9	-	6.1	-
LB71		10	10+10+10	1+2	134	164	0.41	42	6.9	-	6.1	-
LB72		8, 10	8+10+8	1+2	134	160	0.36	37	6.9	-	6.1	-





附录二 墙体选用表

图集号 03J111-2

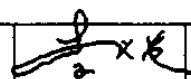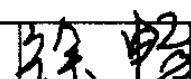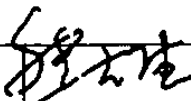审核 李长发  校对 徐畅  设计 熊火生 

页 57

续 附表 4

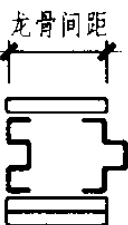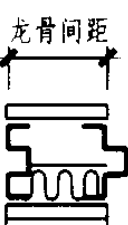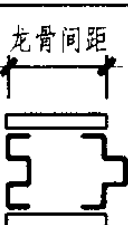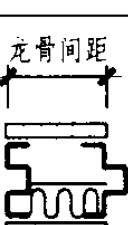产品 代号	图示	墙体尺寸 (mm)					墙体自重 (计算值)		墙体最大高度 m (计算值)			
		面板厚	面板排板方式	层数	龙骨宽度	墙厚	kN/m ²	kg/m ²	龙骨间距 (mm)			
									200	300	400	600
LB73		8, 10	8+10+8	1+2	134	160	0.37	38	6.9	-	6.1	-
LB74		10, 8	10+8+8	1+2	134	160	0.36	37	6.9	-	6.1	-
LB75		10, 8	10+8+8	1+2	134	160	0.37	38	6.9	-	6.1	-
LB76		10, 8	10+10+8	1+2	134	162	0.38	39	6.9	-	6.1	-
LB77		10, 8	10+10+8	1+2	134	162	0.39	40	6.9	-	6.1	-
LB78		8, 10	10+10+8+8	2+2	134	170	0.46	47	6.9	-	6.1	-


附录二 墙体选用表

图集号

03J111-2


审核

李长发

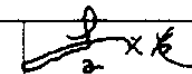


校对

徐畅

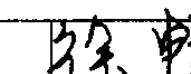

设计




熊火生

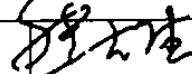

页

58

续 附表 4

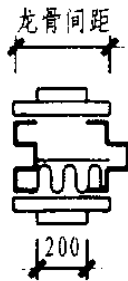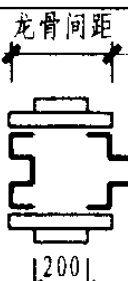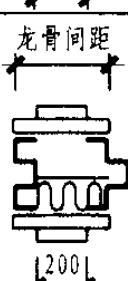产品 代号	图示	墙体尺寸 (mm)					墙体自重 (计算值)		墙体最大高度 m (计算值)			
		面板厚	面板排板方式	层数	龙骨宽度	墙厚	kN/m ²	kg/m ²	龙骨间距 (mm)			
									200	300	400	600
LB79		8, 10	8+8+10+10	2+2	134	170	0.47	48	6.9	-	6.1	-
LB80		8	8+8+8+8	2+2	134	166	0.42	43	6.9	-	6.1	-
LB81		8	8+8+8+8	2+2	134	166	0.43	44	6.9	-	6.1	-
LB82		10	10+10+10+10	2+2	134	174	0.50	51	6.9	-	6.1	-
LB83		10	10+10+10+10	2+2	134	174	0.51	52	6.9	-	6.1	-

附录二 墙体选用表

图集号

03J111-2

审核

李长发

校对

徐畅



设计

熊火生

页

59

续 附表 4

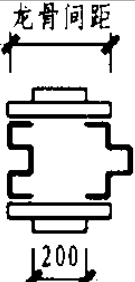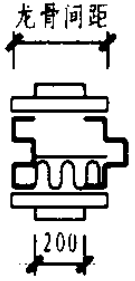产品 代号	图示	墙体尺寸 (mm)					墙体自重 (计算值)		墙体最大高度 m (计算值)			
		面板厚	面板排板方式	层数	龙骨宽度	墙厚	kN/m ²	kg/m ²	龙骨间距 (mm)			
									200	300	400	600
LB84		8, 10	8+10+8+10	2+2	134	170	0.45	46	6.9	-	6.1	-
LB85		8+10	8+10+8+10	2+2	134	170	0.46	47	6.9	-	6.1	-

主编单位、参编单位、联系人及电话

主编单位 中国建筑标准设计研究院

曹颖奇 010-88361155-210

胡 珊 010-88361155-212

参编单位 南昌中环新型墙体装璜材料厂

熊火生 0791-8326468 13870833811

主管单位、联系人及电话

中国建筑标准设计研究院

胡 珊 010-88361155-212

曹颖奇 010-88361155-210